


Abbrevation's:
WOW-Wall Opening Width
WOH-Wall Opening Height
CH- Clear Height
UC-Under Cut
FFL-Finished Floor Level

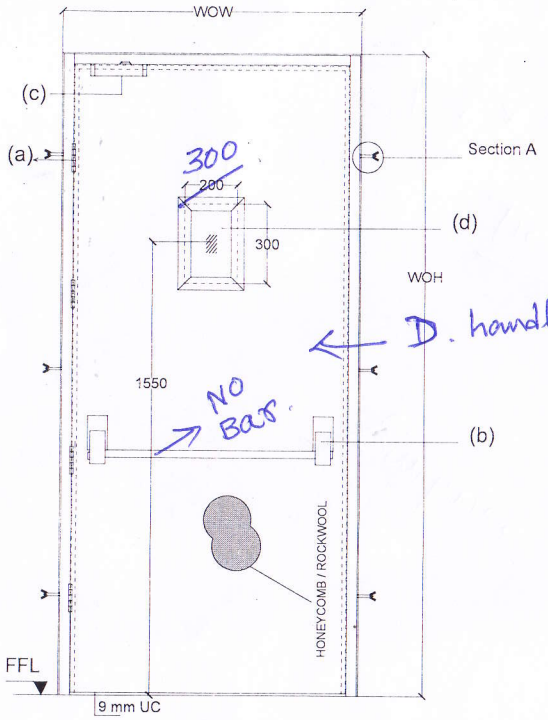

ELEVATION

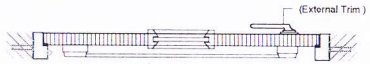

Top View

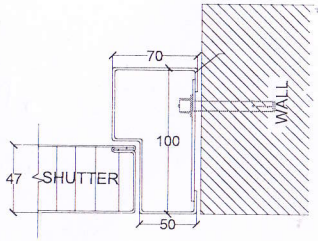

ASSESORIES DETALES

(a) HINGES: SS hinges 100x75x3mm

(b) LOCK : Panic Bar-Dorma single point latching PHA2000
Outer trim-Dorma for panic without cylinder PHT03

(c) DOOR CLOSER : TS68

(d) VISION PANEL- 5mm THK. FIRE GLASS SIZE- 200X300mm.

Shutter thickness : 47 mm
Frame Sheet thick : 1.20mm
Shutter sheet thick : 0.80mm
Fixing : On Soliid Brick plasterd wall with Anchors

NOTE:- *All Dimensions are in mm.
*Tolerance:-All Linear Dimensions ±3mm,Others ±0.5mm.
*The Drawing Is For Location of Hardware only. Drawing Does Not Represent The Hardware For More Clarity. Please Go Through Hardware Broucher.

Fire door size

	WOW (mm)	WOH (mm)	TYPE 1	TYPE 2	TYPE 3	TYPE 4	QUANTITY
1.	1200	2000			✓		01 nos
2.	1200	2000				✓	01 nos

Location
Tic Tac
Surprise

Note:- 1) Windo Size - 300mm x 300 mm
2) D-handle both sides with key Lock system.
3) Door closure. 4) Wall (RCC) mounted

22/11/18.

COLOR
1.TRAFFIC WHITE - RAL 9016
2.LIGHT GRAY - RAL 7035
3.GENTION BLUE - RAL 5010
4.SIGNAL RED - RAL 3001

NOTE- CLIENT SHOULD SELECT DOOR TYPE FROM DOOR HANDLING SHEET & COLOR OF DOOR.

This drawing & designing is the property of NIHVA TECHNOLOGIES. Not to be sold or copied to any other concern.

TITLE: SINGLE LEAF FIRE RATED DOORS

NIHVA TECHNOLOGIES PVT. LTD

NIHVA TECHNOLOGIES PVT. LTD. PUNE
Tel : 020 66304033
Email:- info@nihva.com
Website:- www.nihva.com

	SIGN	DATE	
DRAWN	SURAJ	15/10/17	CLIENT - FERRERO INDIA PVT. LTD
CHECK	SHEKHAR	15/10/17	PROJECT -
REV.	00		SITE - BARAMATI.
APPROVAL	SHEKHAR	15/10/17	DWG. NO. :

If any queries contact : projects@nihva.com | SCALE: NTS | WT: | SHEET: 01 OF 01

ALL DIMENSION ARE IN mm