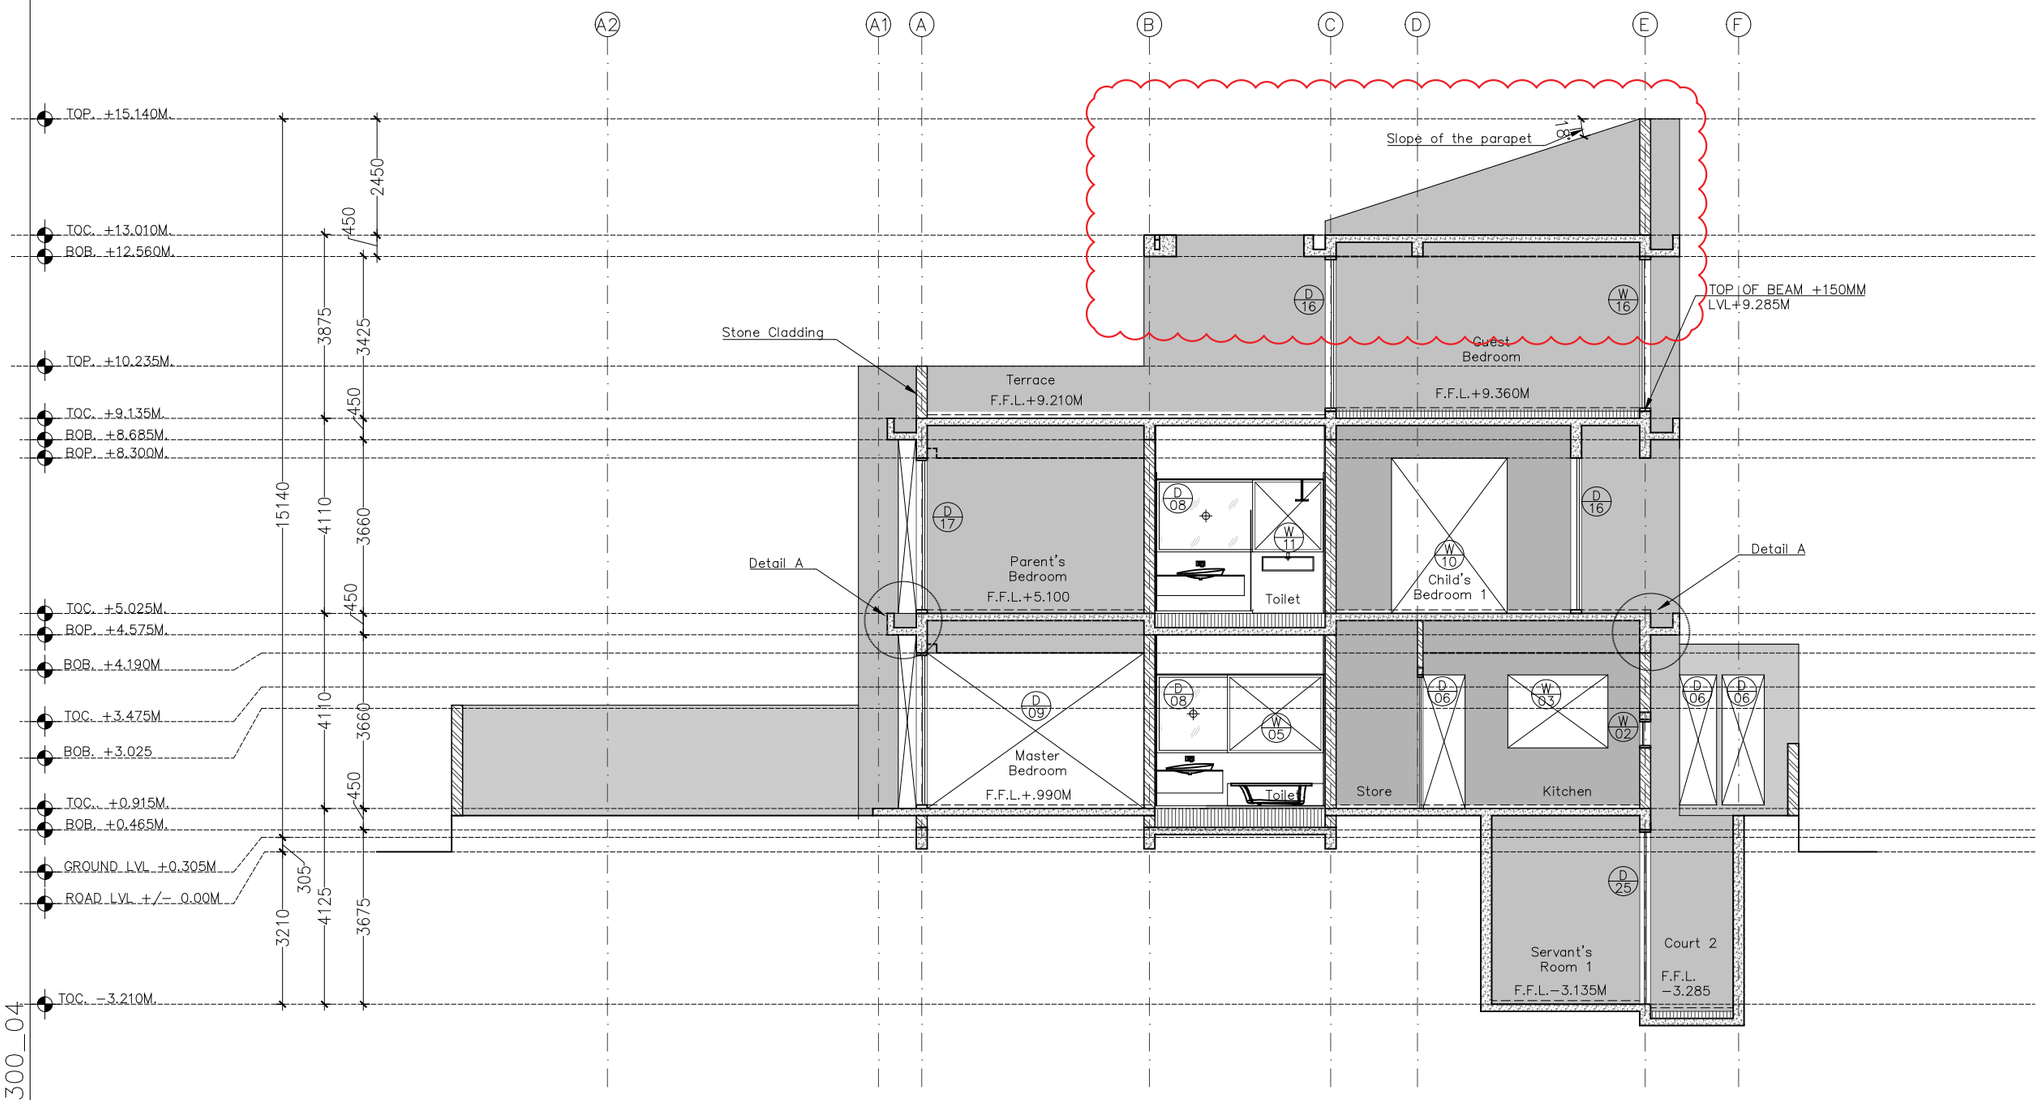


1 General Arrangement– Section A

Scale 1:125

PLOT DATE /TIME:

DESIGN FILE : 200908-A-300_04

Notes:

1. All dimensions are in MM. Do not scale
2. Contractor to Check all dimensions and report omissions and errors to the Architect
3. All levels are structural floor levels (top of concrete)

Drawing Revision Table

No	Revision	Date	Initial	Chkd
1	Updated Levels	27.1.21	HM	KV
2	For Construction	19.2.21	HM	KV
3	For Construction	24.08.21	HM	KV
4	As clouded	25.04.22	HM	KV

Drawing Issue Table

Date	Issued to	Mode	Purpose
13.01.21	Contractor	Email	Information
22.01.21	Contractor	Email	Information
19.02.21	Contractor	Email	Construction
24.08.21	Contractor	Email	Construction
25.04.21	Contractor	Email	Construction

LEGEND

TOC–Top of Concrete

TOB–Top of Beam

BOB–Bottom of Beam

TOP–Top of Parapet

BOP–Bottom of Projection

FFL–Finish Floor Level
FGL–Finish Ground Level

NOTE: This drawing and the design it covers is the property of PVDRS. It is merely loaned on the borrower's express agreement that it will not be reproduced, copied, loaned, exhibited nor used except in a limited way and private use as permitted by any written consent given by the lender to the borrower.

Firm Name
PVDRS

Project Name
Bhattacharya House

Project Location
Ahmedabad

Drawing Title
Section A

Purpose	25/04/2022
For Construction	Drg by: HM Chk by: KV

Drawing Number	Revision Number
200908-A-300	04