

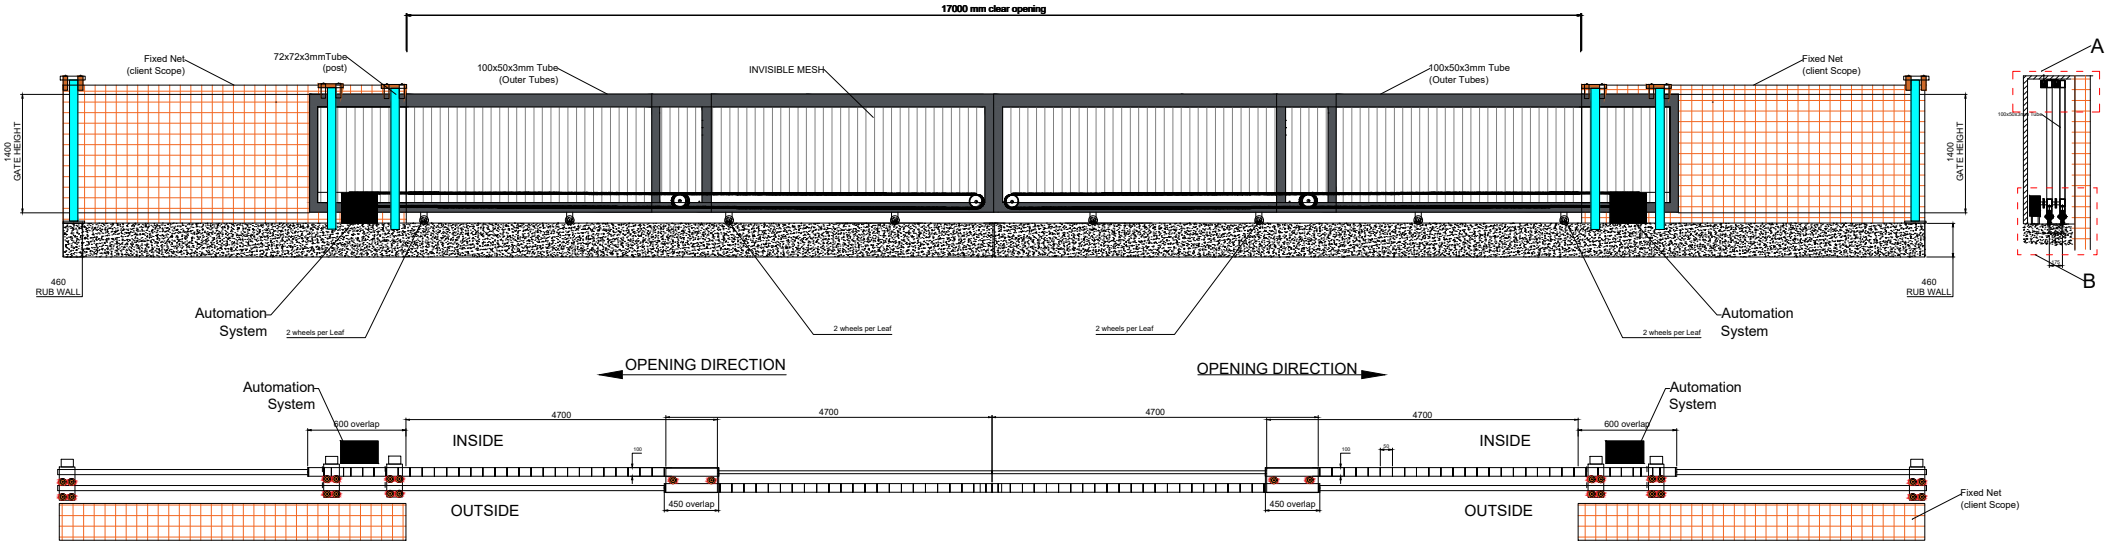


DETAIL "A"

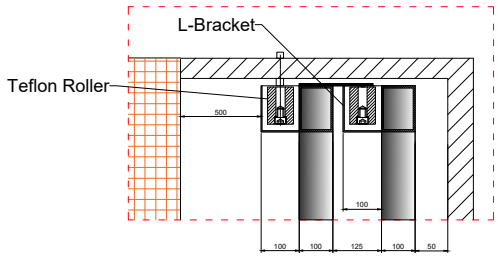

DETAIL "B"

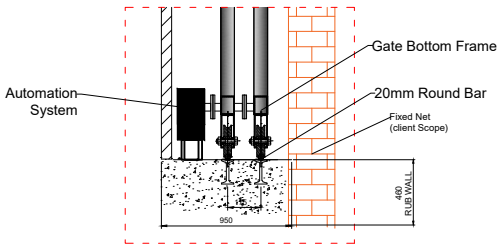

Clear Opening size - 17000mm x 1400mm
Total No. of Leaf - 4 Leaf
RAL Code code conform by client
NOTE :- *ALL REQ. CIVIL WORK WILL BE IN CLIENT SCOPE.

This drawing & designing is the property of NIHVA TECHNOLOGIES. Not be sold or copy to any other concern.

TITLE	TELESCOPIC SLIDING GATE	
	SIGN	DATE
DRAWN	J.P	15/10/25
CHECK	B.S	15/10/25
REV.	00	
APPROVAL		

NIHVA TECHNOLOGY PVT. LTD. PUNE
Tel : 020 66304033
Email :- info@nihva.com
Website:- www.nihva.com

CLIENT - KOHLI VILLA
PROJECT - TELESCOPIC SLIDING GATE
SITE -
DWG. NO. : NIHVA/15-16/178
SCALE: 01 | WT: | SHEET: 01 OF 01

If any queries contact : projects@nihva.com
ALL DIMENSION ARE IN mm