


# Prinzipzeichnung RapidProtect RP300


General drawing Rapid Protect RP300

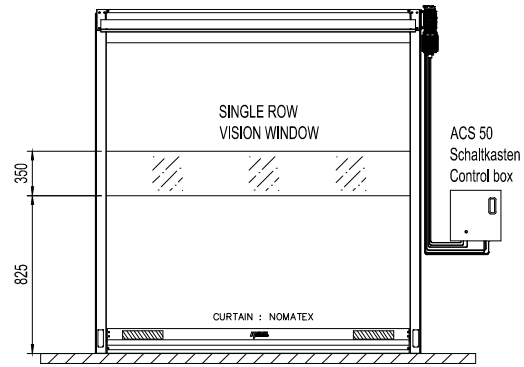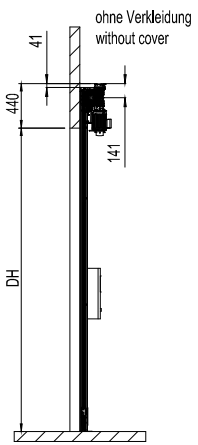


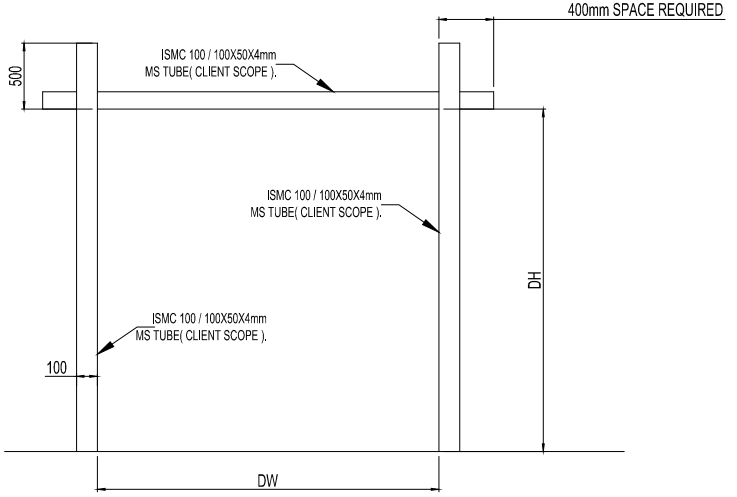



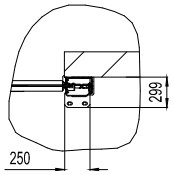



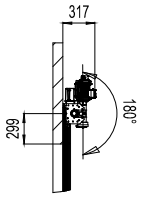

MS STRUCTURE

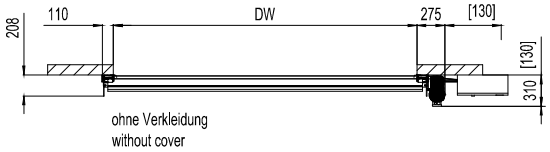

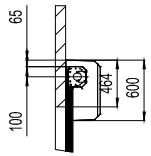
| DOOR SIZE | | |
|---|---|---|
| DW | DH | QUANTITY |
| 1400 | 2200 | 1 |
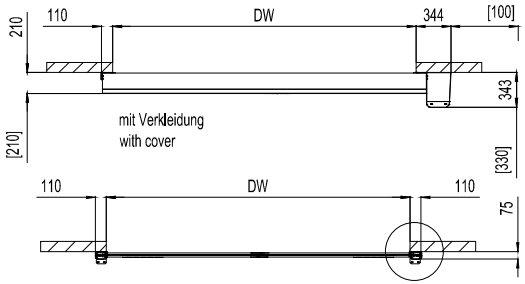
| | |
|---|---|
| RAL 1003 | |
| RAL 2004 | |
| RAL 3000 | |
| RAL 5002 | |
| RAL 6005 | |
| RAL 7035 | |
| RAL 9005 | |
| RAL 9010 | |

| |
|---|
| Toleranz ±3 mm (gültig für alle Maßangaben)<br>Tolerance ±3 mm (for all dimensions) |
| Maßangaben in [ ] ==> Montagefreiraum<br>Dimensions in [ ] ==> clearance for installation |

NOTE-
1. COLOR : RAL 5002 ( BLUE ).
2. CURTAIN : NOMATEX.
3. REQUIRED STRUCTURE FOR HSD WILL BE IN CLIENT'S SCOPE.

| REV.NO | DESCRIPTION | DRAWN | DATE | SIGN |
|---|---|---|---|---|
| R01 | 2.WINDOW SIZE CHANGED.<br>1.ADDED RAL COLOUR. | SURAJ | 22-10-2018 | |

This drawing & designing is the property of NIHVA TECHNOLOGIES. Not be sold or copy to any other concern.

TITLE: HIGH SPEED DOOR RP 300 & STRUCTURE

NIHVA TECHNOLOGIES PVT. LTD.
NIHVA TECHNOLOGIES PVT. LTD. PUNE
Tel : 020 66304033
Website:- www.nihva.com
Email :- info@nihva.com

| | NAME | SIGN | DATE |
|---|---|---|---|
| DRAWN | P.A | | 21.10.2018 |
| CHECK | R.D | | 21.10.2018 |
| REV. | V.T | | 21.10.2018 |
| APPROVAL | | | |

If any queries contact : sales@nihva.com

ALL DIMENSIONS ARE IN mm

CLIENT - FINEARC SYSTEMS LTD
PROJECT -
SITE - PUNE
DWG. NO. : NIHVA/18-19/0157/R01 REV:- 01
SCALE: NTS WT: SHEET: 01 OF 01