

DRAWING

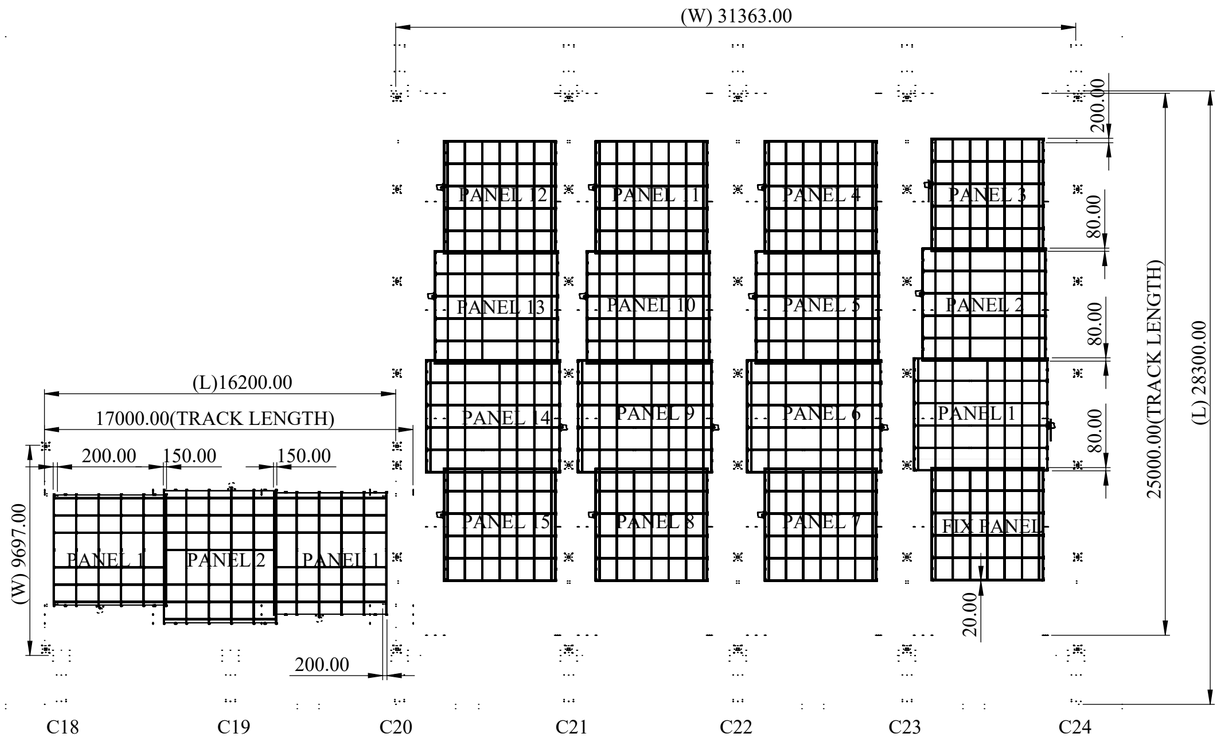


SPA SHOP UNIT

VWM & HWM SHOP UNIT


T.V.

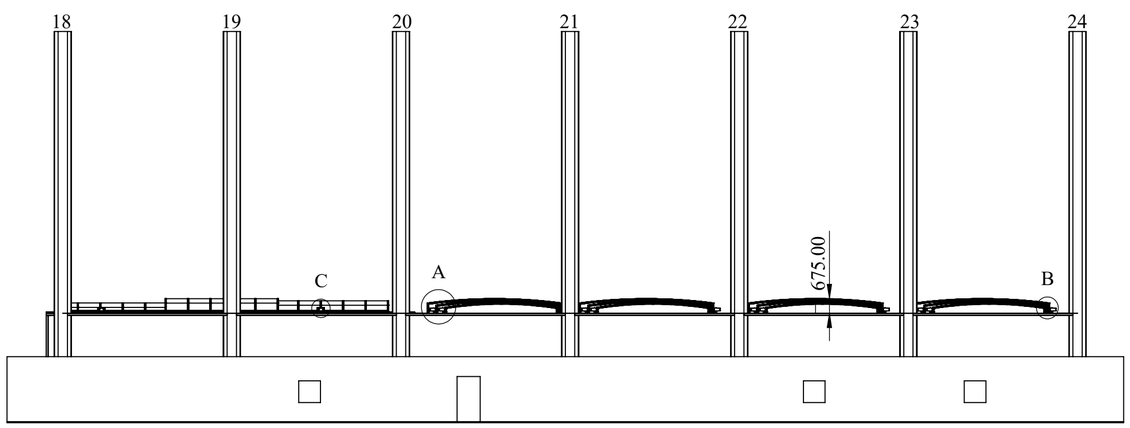


F.V.

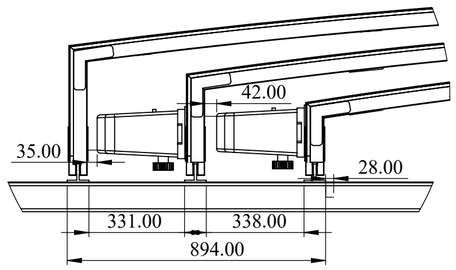

DETAIL A
SCALE 1 : 15

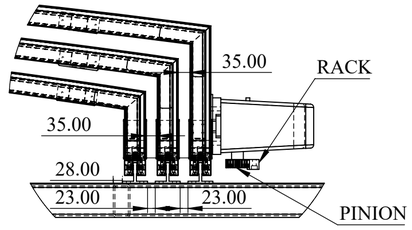

DETAIL B
SCALE 1 : 13

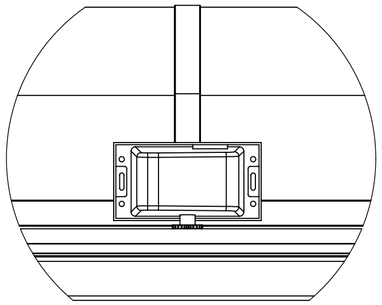

DETAIL C
SCALE 1 : 10

MOTOR

REV DESCRIPTION	DATE	REV NO
	11-06-2026	REV 00
1.		

NOTE :

SPECIAL INSTRUCTION'S :

This drawing & design is the property of NIHVA TECHONOLOGIES PVT. LTD. Not to be sold or copied to any other concern.

TITLE - ROOF AUTOMATION

DWG NO - NTPL-401-PM-01

NIHVA TECHNOLOGIES PVT.LTD.PUNE
Website - www.nihva.com

	NAME	SIGNATURE	DATE
DRAWN	V.W.		11-06-2026
CHK'D	S.P.		13-06-2026
APPV'D	V.T.		13-06-2026

PRODUCT - C-SHAPE RETRACTABLE ROOF

PROJECT NO - NTPL-000-PM | REVISION - 00

SITE LOCATION-HYDRABAD | WEIGHT -

MATRIAL - | QTY - 1


If any queries contact - design2@nihva.com

ALL DIMENSION ARE IN mm | A2

PROJECTION METHOD:

SCALE :


DRAWING

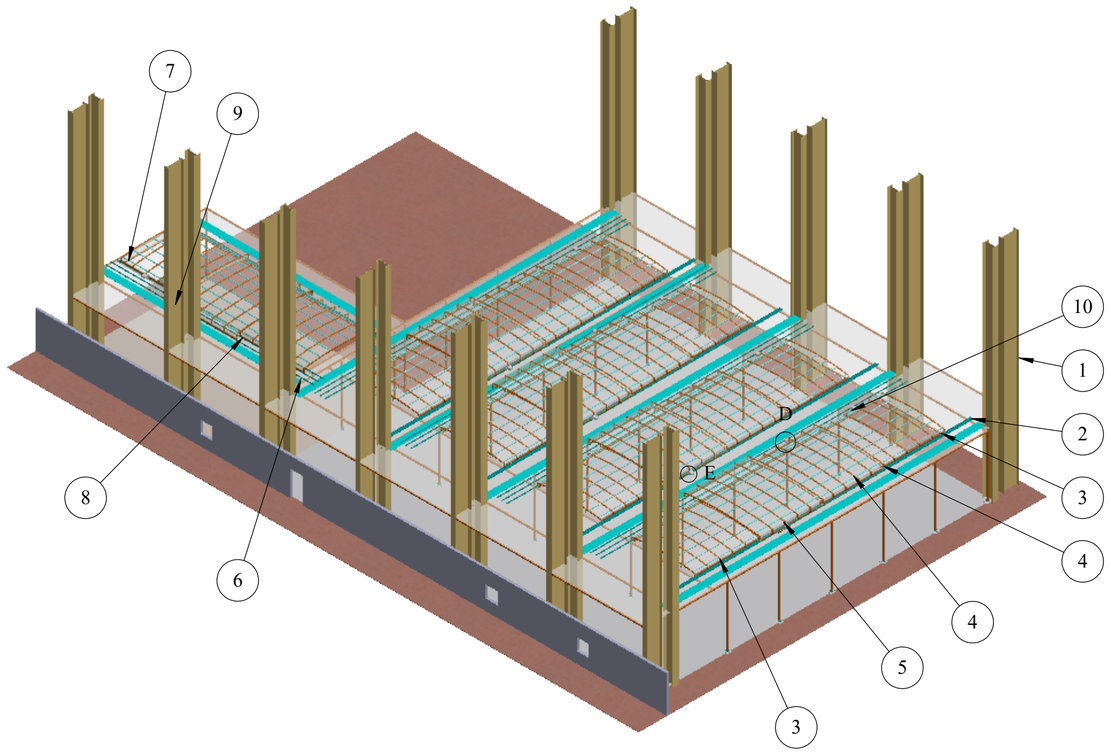

ISO VIEW


ITEM NO.	PART NUMBER	DESCRIPTION	QTY.
1	BASE STRUCTURE ASSEMBLY VWM & HWM UNIT & SPA SHOP UNIT	CLIENT SCOPE	1
2	GUIDE RAILS-T75-1B	STD (5 M LENGTH)	120
3	PANEL ASM NO - 1	AL FRAME	8
4	PANEL ASM NO - 2	AL FRAME	4
5	PANEL ASM NO - 3	AL FRAME	4
6	GUIDE RAILS-T75-1B	STD (5 M LENGTH)	22
7	PANEL ASM NO - 1 SPA	AL FRAME	1
8	PANEL ASM NO - 2 - SPA	AL FRAME	1
9	PANEL ASM NO - 3- SPA	AL FRAME	1
10	RACK	STD (1 M LENGTH)	225

REV DESCRIPTION	DATE	REV NO
	11-06-2026	REV 00
1.		

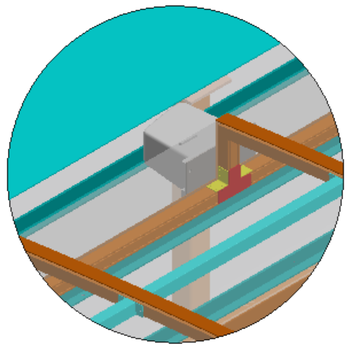

DETAIL D
SCALE 1 : 15

MOTOR MOUNTING

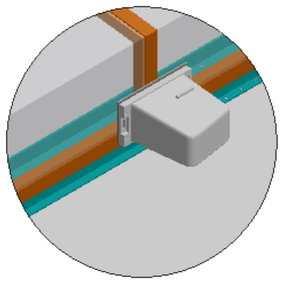

DETAIL E
SCALE 1 : 15

MOTOR MOUNTING

NOTE :

SPECIAL INSTRUCTION'S :

This drawing & design is the property of NIHVA TECHONOLOGIES PVT. LTD. Not to be sold or copied to any other concern.

TITLE - ROOF AUTOMATION

DWG NO - NTPL-401-PM-01

NIHVA Technologies Pvt. Ltd.


NIHVA TECHNOLOGIES PVT.LTD.PUNE
Website - www.nihva.com

	NAME	SIGNATURE	DATE
DRAWN	V.W.		11-06-2026
CHK'D	S.P.		13-06-2026
APPV'D	V.T.		13-06-2026

PRODUCT - C-SHAPE RETRACTABLE ROOF
PROJECT NO - NTPL-000-PM
REVISION - 00
SITE LOCATION-HYDRABAD
WEIGHT -
MATRIAL -
QTY - 1
SCALE :


If any queries contact - design2@nihva.com
ALL DIMENSION ARE IN mm
A2
PROJECTION METHOD:

DRAWING

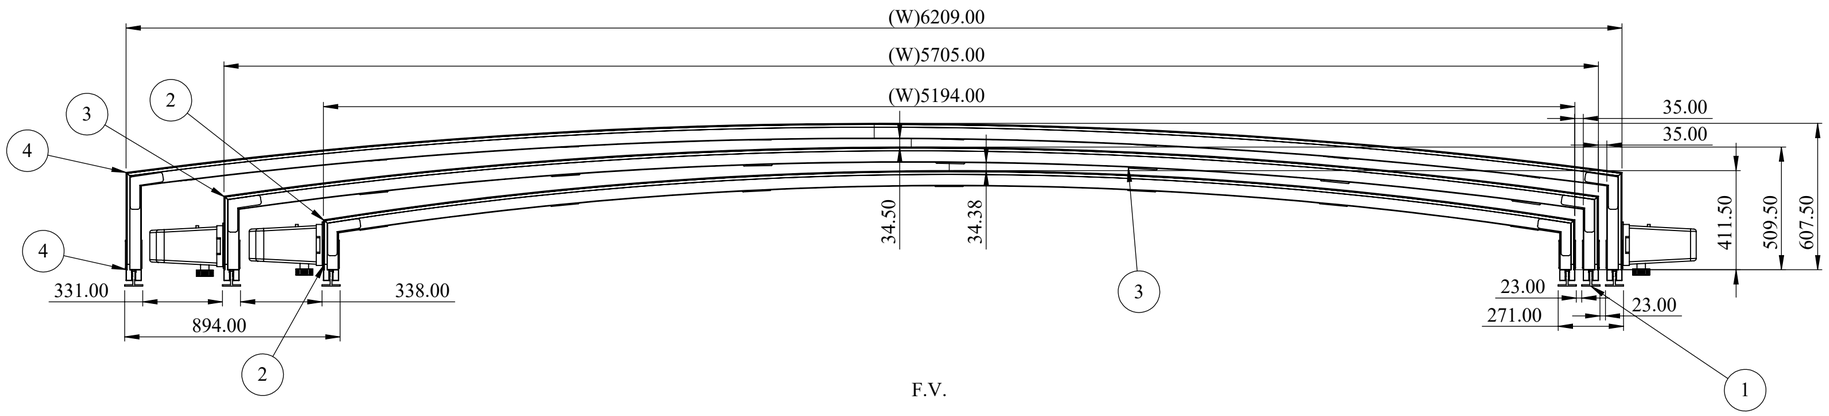

F.V.

REV DESCRIPTION	DATE	REV NO
	11-06-2026	REV 00
1.		

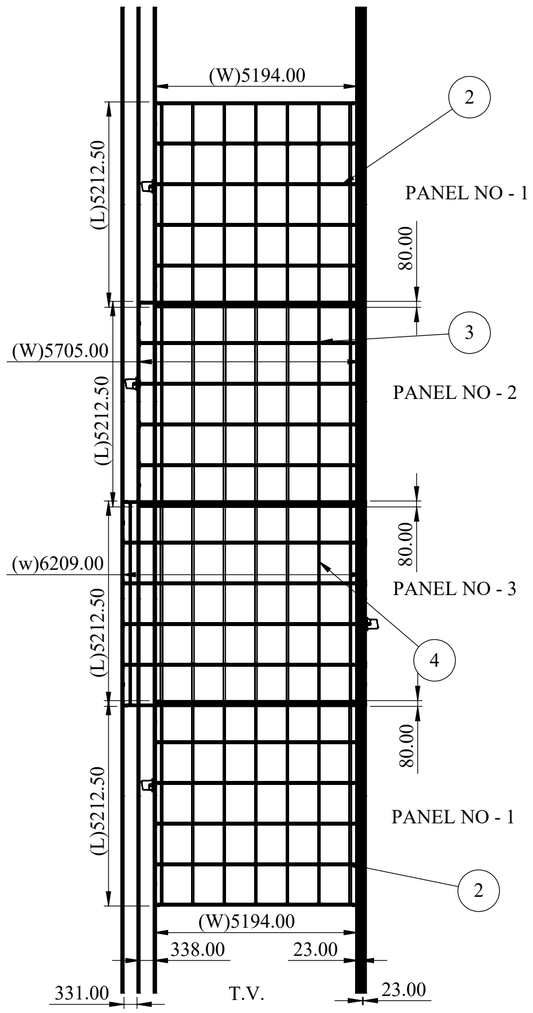

ITEM NO.	PART NUMBER	DESCRIPTION	QTY.
1	GUIDE RAILS-T75-1B	STD (5 M LENGTH)	30
2	PANEL ASM NO - 1	AL FRAME	2
3	PANEL ASM NO - 2	AL FRAME	1
4	PANEL ASM NO - 3	AL FRAME	1

NOTE :

FOUR PANEL ASSEMBLY

SPECIAL INSTRUCTION'S :

This drawing & design is the property of NIHVA TECHONOLOGIES PVT. LTD. Not to be sold or copied to any other concern.

TITLE - ROOF AUTOMATION

DWG NO - NTPL-401-PM-01

NIHVA TECHNOLOGIES PVT.LTD.PUNE
Website - www.nihva.com

	NAME	SIGNATURE	DATE
DRAWN	V.W.		11-06-2026
CHK'D	S.P.		13-06-2026
APPV'D	V.T.		13-06-2026

PRODUCT - C-SHAPE RETRACTABLE ROOF

PROJECT NO - NTPL-000-PM | REVISION - 00

SITE LOCATION-HYDRABAD | WEIGHT -

MATRIAL - | QTY - 1


If any queries contact - design2@nihva.com

ALL DIMENSION ARE IN mm | A2

PROJECTION METHOD:

SCALE :


DRAWING

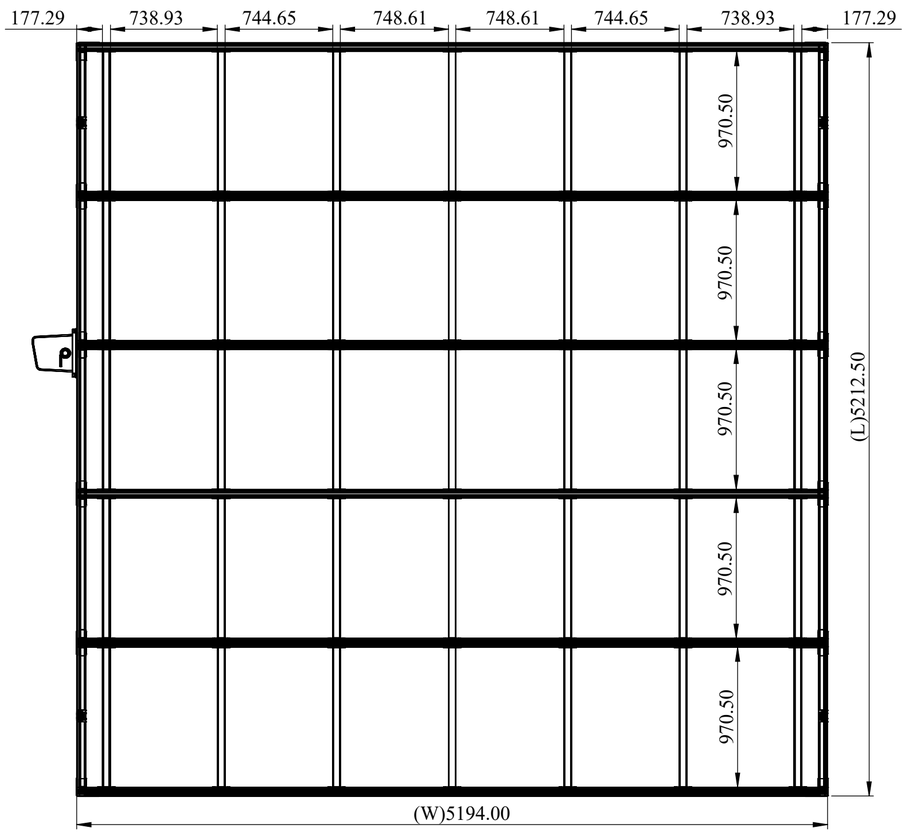


T.V.

ITEM NO.	PART NUMBER	DESCRIPTION	QTY.
1	PANEL 1	AL PROFILE	1
2	BEARING BLOCK ASM _ T75_1B.	AL	4
3	INTERMEDIATE SUPPORT TUBE ASM .	SQ TUBE - 50X50X1.5MM THK	35
4	MOTOR BASE PLATE	AL	1
5	NICE RB 1T	MOTOR	1
6	T PLATE	SS304 -117.5X156X3 MM THK	16
7	L PLATE	SS304- 91X106X3 MM THK	8
8	L ANGLE PLATE	SS304 - 60X60X3 MM	20
9	L ANGLE WELDING CORNER JOINING PLATE	AL WELDING JOINING PLATE	24

REV DESCRIPTION	DATE	REV NO
	11-06-2026	REV 00
1.		

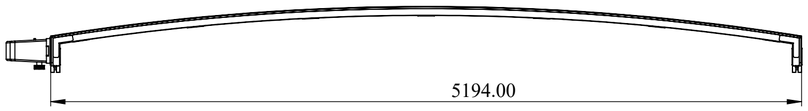

F.V.

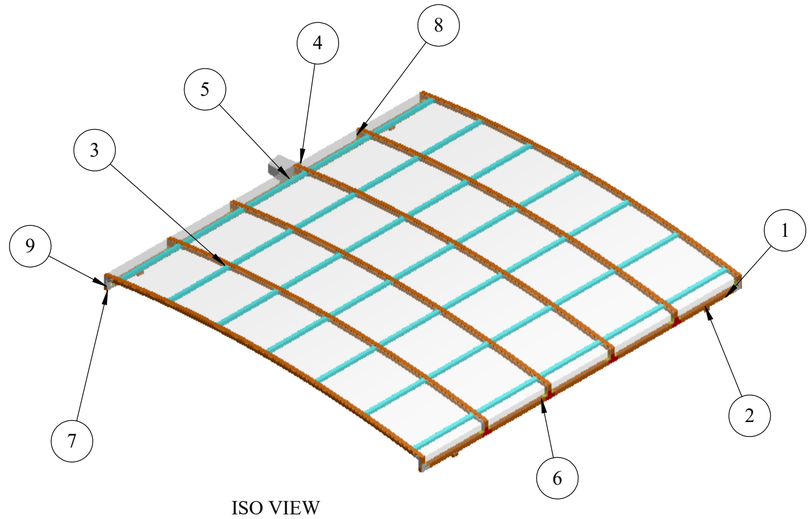

ISO VIEW
PANEL NO - 01 ASM

NOTE :

NAME : PANEL NO - 1 ASM
PROFILE : AL GNTOO6
QTY : 08 NOS.

SPECIAL INSTRUCTION'S :

This drawing & design is the property of NIHVA TECHONOLOGIES PVT. LTD. Not to be sold or copied to any other concern.

TITLE - ROOF AUTOMATION


DWG NO - NTPL-401-PM-01

NIHVA TECHNOLOGIES PVT.LTD.PUNE
Website - www.nihva.com

	NAME	SIGNATURE	DATE
DRAWN	V.W.		11-06-2026
CHK'D	S.P.		13-06-2026
APPV'D	V.T.		13-06-2026


PRODUCT - C-SHAPE RETRACTABLE ROOF
PROJECT NO - NTPL-000-PM
REVISION - 00
SITE LOCATION-HYDRABAD
WEIGHT -
MATRIAL -
QTY - 1
SCALE :
PROJECTION METHOD:
If any queries contact - design2@nihva.com
ALL DIMENSION ARE IN mm
A2

DRAWING

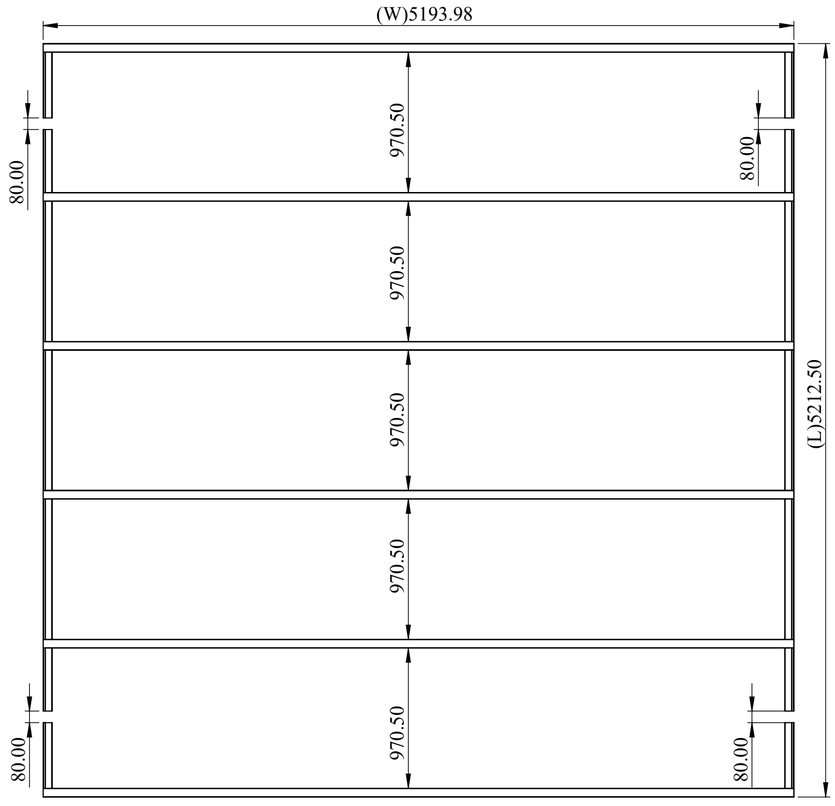


T.V.

ITEM NO.	PART NUMBER	DESCRIPTION	QTY.
1	PANEL 1	AL PROFILE	08

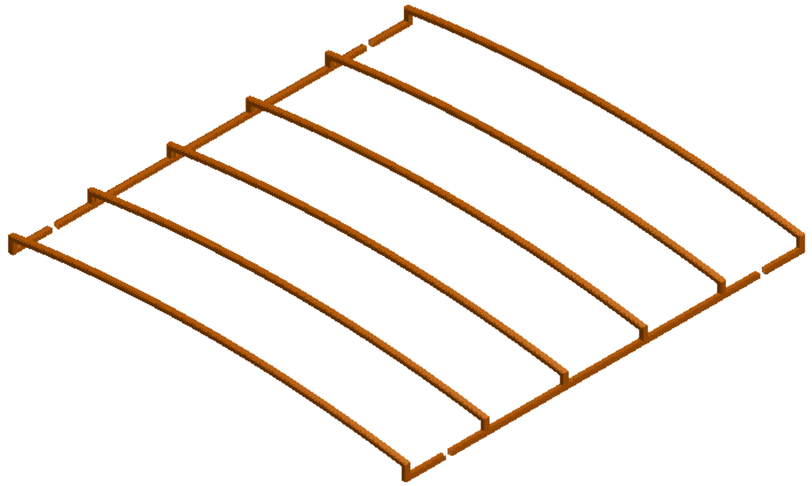


ISO VIEW OF PANEL


REV DESCRIPTION	DATE	REV NO
	11-06-2026	REV 00
1.		

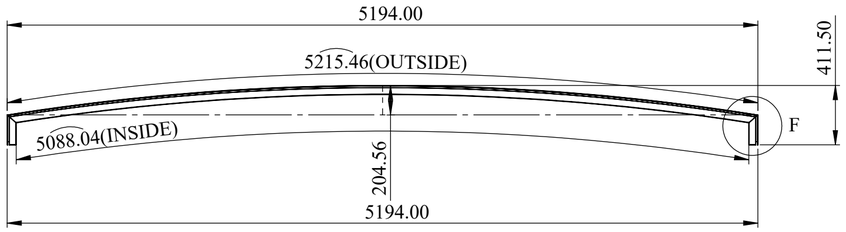


F.V.

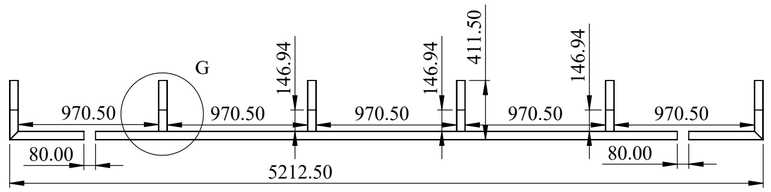

SIDE VIEW

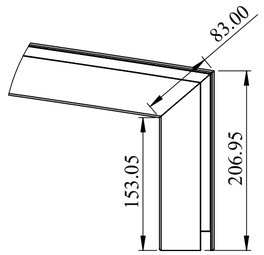

DETAIL F
SCALE 1 : 5

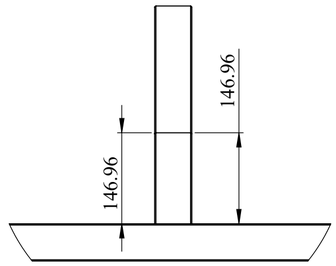

DETAIL G
SCALE 1 : 7

NOTE :

NAME : PANEL NO - 1
PROFILE : AL GNTOO6 (60X63)
QTY : 08 NOS

SPECIAL INSTRUCTION'S :

This drawing & design is the property of NIHVA TECHONOLOGIES PVT. LTD. Not to be sold or copied to any other concern.

TITLE - ROOF AUTOMATION

DWG NO - NTPL-401-PM-01


NIHVA TECHNOLOGIES PVT.LTD.PUNE
Website - www.nihva.com

	NAME	SIGNATURE	DATE
DRAWN	V.W.		11-06-2026
CHK'D	S.P.		13-06-2026
APPV'D	V.T.		13-06-2026


PRODUCT - C-SHAPE RETRACTABLE ROOF
PROJECT NO - NTPL-000-PM
REVISION - 00
SITE LOCATION-HYDRABAD
WEIGHT -
MATRIAL -
QTY - 1
SCALE :
PROJECTION METHOD:
SHEET 5 OF 20

If any queries contact - design2@nihva.com
ALL DIMENSION ARE IN mm
A2


DRAWING

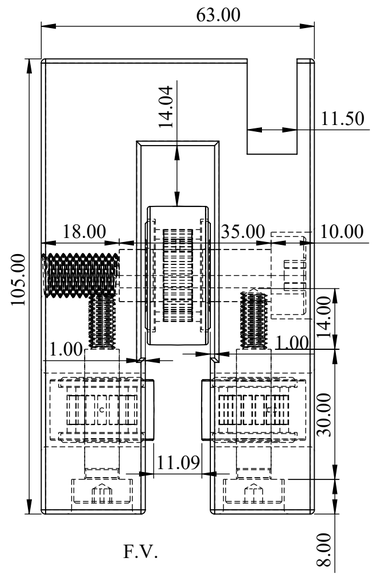

F.V.

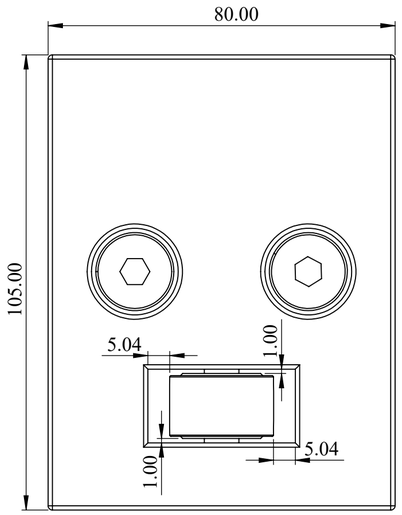


S.V.

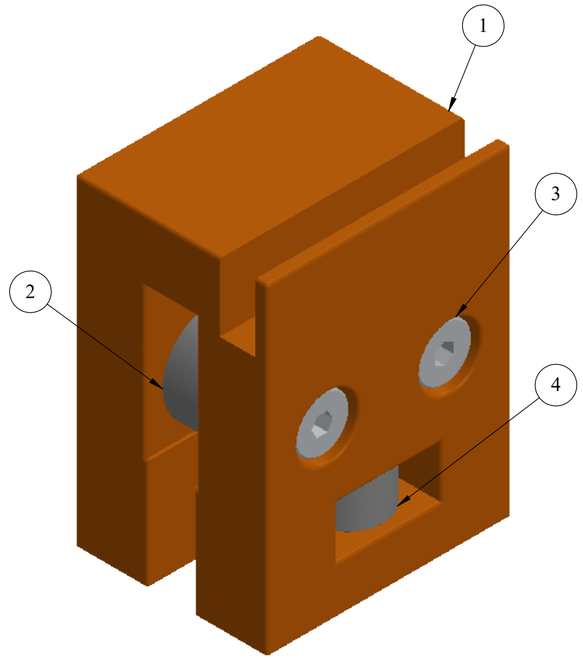

ISO VIEW

REV DESCRIPTION	DATE	REV NO
	11-06-2026	REV 00
1.		

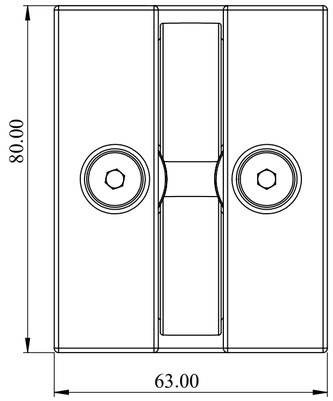

B.V.

ITEM NO.	PART NUMBER	DESCRIPTION	QTY.
1	BEARING BLOCK (T75-1B)	80X105X63 MM (VMC PART)	1
2	BEARING SKF_NATR 12	SKF (STD)	2
3	SHOULDER BOLT NATR 12.	SS	2
4	BEARING SKF_NATR 8	SKF(STD)	2
5	SHOULDER BOLT NATR - 8 x 30 --- N	SS	2

NOTE :

NAME : BEARING BLOCK HOUSING ASSEMBLY
SIZE : W63 X L80 X H105 MM
QTY FOR 1 PANEL : 4 NOS
QTY FOR 16 PANEL : 64 NOS

SPECIAL INSTRUCTION'S :

This drawing & design is the property of NIHVA TECHONOLOGIES PVT. LTD. Not to be sold or copied to any other concern.

TITLE - ROOF AUTOMATION


DWG NO - NTPL-401-PM-01


NIHVA TECHNOLOGIES PVT.LTD.PUNE
Website - www.nihva.com

	NAME	SIGNATURE	DATE
DRAWN	V.W.		11-06-2026
CHK'D	S.P.		13-06-2026
APPV'D	V.T.		13-06-2026

PRODUCT - C-SHAPE RETRACTABLE ROOF
PROJECT NO - NTPL-000-PM
REVISION - 00
SITE LOCATION-HYDRABAD
WEIGHT -
MATRIAL -
QTY - 1
If any queries contact - design2@nihva.com
ALL DIMENSION ARE IN mm
A2
PROJECTION METHOD:
SCALE :


DRAWING

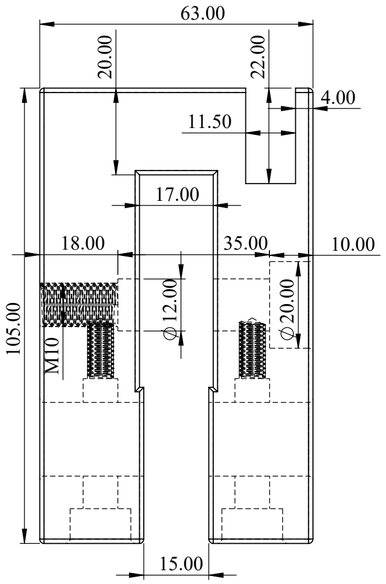


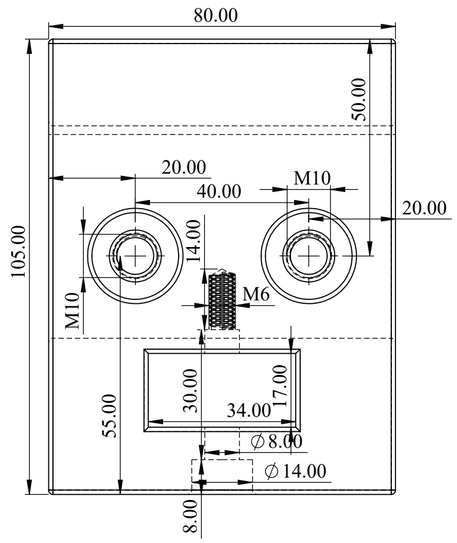

ITEM NO.	PART NUMBER	DESCRIPTION	QTY.
1	BEARING BLOCK (T75-1B)	80X105X63 MM (VMC PART)	1

REV DESCRIPTION	DATE	REV NO
	11-06-2026	REV 00
1.		

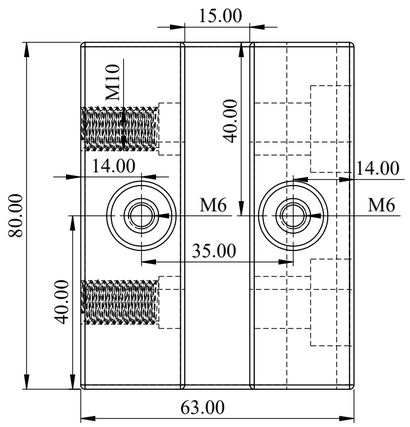

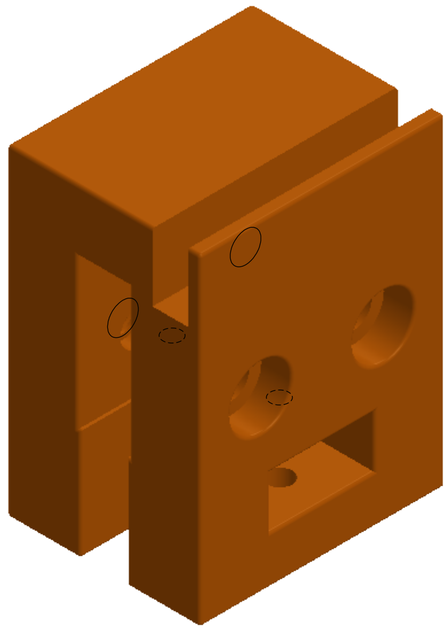

NOTE :

NAME : BEARING BLOCK HOUSING
SIZE : W63 X L80 X H105 MM
MTL : AL
QTY FOR 1 PANEL : 4 NOS
QTY FOR 16 PANEL : 64 NOS
OPERATION : VMC MACHINING

SPECIAL INSTRUCTION'S :

This drawing & design is the property of NIHVA TECHONOLOGIES PVT. LTD. Not to be sold or copied to any other concern.

TITLE - ROOF AUTOMATION

DWG NO - NTPL-401-PM-01

NIHVA Technologies Pvt. Ltd.


NIHVA TECHNOLOGIES PVT.LTD.PUNE
Website - www.nihva.com


	NAME	SIGNATURE	DATE
DRAWN	V.W.		11-06-2026
CHK'D	S.P.		13-06-2026
APPV'D	V.T.		13-06-2026

PRODUCT - C-SHAPE RETRACTABLE ROOF
PROJECT NO - NTPL-000-PM
REVISION - 00
SITE LOCATION-HYDRABAD
WEIGHT -
MATRIAL -
QTY - 1


If any queries contact - design2@nihva.com
ALL DIMENSION ARE IN mm
A2
PROJECTION METHOD:
SCALE :
SHEET 7 OF 20

DRAWING

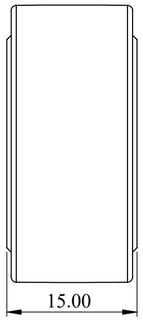

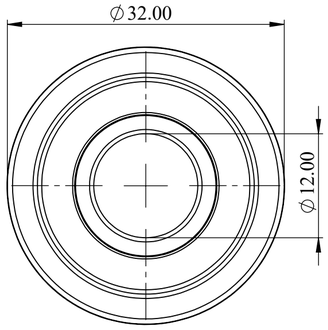


ITEM NO.	PART NUMBER	DESCRIPTION	QTY.
1	BEARING SKF_NATR 12	SKF (STD)	1

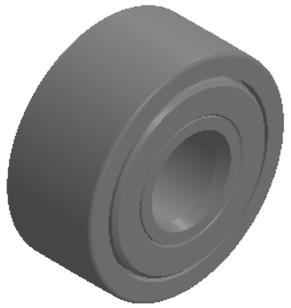



NAME : BEARING SKF NATR 12
SIZE : ID12 X OD32 X W15 MM
MTL : BEARING STEEL
QTY FOR 1 BLOCK : 2 NOS
QTY FOR 64 BLOCK : 128 NOS
DYANAMIC LOAD RATING : 7.04 KN

REV DESCRIPTION	DATE	REV NO
	11-06-2026	REV 00
1.		

ITEM NO.	PART NUMBER	DESCRIPTION	QTY.
1	BEARING SKF_NATR 8	SKF(STD)	1

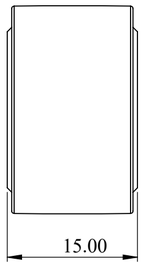

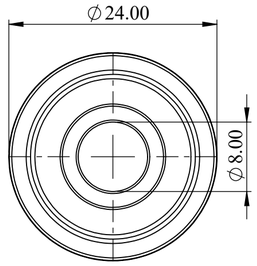

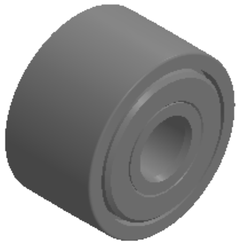

NAME : BEARING SKF NATR 8
SIZE : ID8 X OD24 X W15 MM
MTL : BEARING STEEL
QTY FOR 1 BLOCK : 2 NOS
QTY FOR 64 BLOCK : 128 NOS
DYANAMIC LOAD RATING : 4.57 KN

NOTE :

SPECIAL INSTRUCTION'S :

This drawing & design is the property of NIHVA TECHONOLOGIES PVT. LTD. Not to be sold or copied to any other concern.

TITLE - ROOF AUTOMATION


DWG NO - NTPL-401-PM-01


NIHVA TECHNOLOGIES PVT.LTD.PUNE
Website - www.nihva.com

	NAME	SIGNATURE	DATE
DRAWN	V.W.		11-06-2026
CHK'D	S.P.		13-06-2026
APPV'D	V.T.		13-06-2026


PRODUCT - C-SHAPE RETRACTABLE ROOF
PROJECT NO - NTPL-000-PM
REVISION - 00
SITE LOCATION-HYDRABAD
WEIGHT -
MATRIAL -
QTY - 1
SCALE :
PROJECTION METHOD:
If any queries contact - design2@nihva.com
ALL DIMENSION ARE IN mm
A2

DRAWING

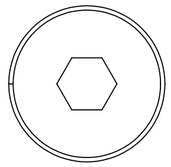

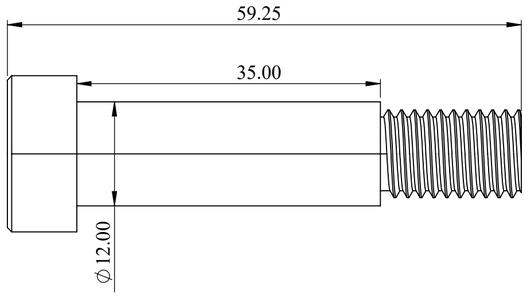



ITEM NO.	PART NUMBER	DESCRIPTION	QTY.
1	SHOULDER BOLT NATR 12.	SS	1

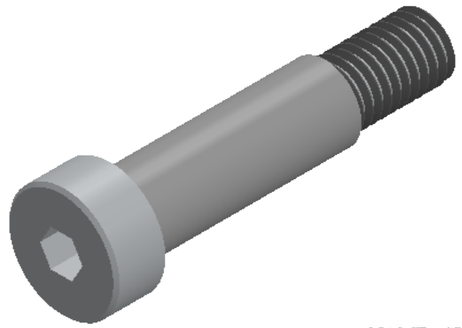

NAME : SHOULDER BOLT NATR 12
SIZE : M12X35 MM
MTL : SS
QTY FOR 1 BLOCK : 2 NOS
QTY FOR 64 BLOCK : 128 NOS

REV DESCRIPTION	DATE	REV NO
	11-06-2026	REV 00
1.		

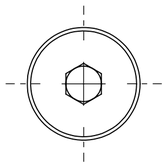

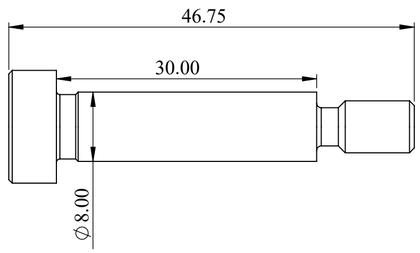

ITEM NO.	PART NUMBER	DESCRIPTION	QTY.
1	ISO 7379 - 8 x 30 --- N	SS	1



NAME : SHOULDER BOLT NATR 8
SIZE : M8X30 MM
MTL : SS
QTY FOR 1 BLOCK : 2 NOS
QTY FOR 64 BLOCK : 128 NOS

NOTE :

SPECIAL INSTRUCTION'S :

This drawing & design is the property of NIHVA TECHONOLOGIES PVT. LTD. Not to be sold or copied to any other concern.

TITLE - ROOF AUTOMATION

DWG NO - NTPL-401-PM-01

NIHVA TECHNOLOGIES PVT.LTD.PUNE
Website - www.nihva.com


	NAME	SIGNATURE	DATE
DRAWN	V.W.		11-06-2026
CHK'D	S.P.		13-06-2026
APPV'D	V.T.		13-06-2026

PRODUCT - C-SHAPE RETRACTABLE ROOF
PROJECT NO - NTPL-000-PM
REVISION - 00
SITE LOCATION-HYDRABAD
WEIGHT -
MATRIAL -
QTY - 1
SCALE :
PROJECTION METHOD:
If any queries contact - design2@nihva.com
ALL DIMENSION ARE IN mm
A2


DRAWING

ITEM NO.	PART NUMBER	DESCRIPTION	QTY.
1	INTERMIDEATE TUBE 50X50x1.5MM .		1
2	INTERMEDIATE SUPPORT WELDING PLATE .		2


REV DESCRIPTION	DATE	REV NO
	05-06-2026	REV 00
1.		

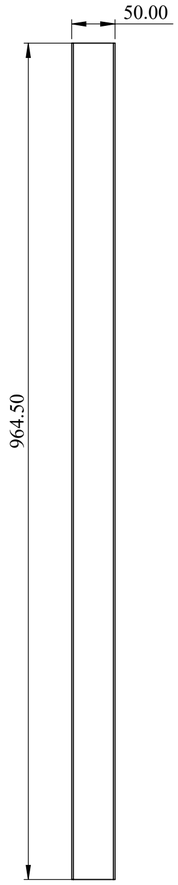


NAME : INTERMEDIATE SUPPORT TUBE
SIZE : 50X50X1.5 MM THK
MTL : AL
QTY FOR 1 PANEL : 36 NOS
QTY FOR 16 PANEL : 576 NOS
OPERATION : CUTTING

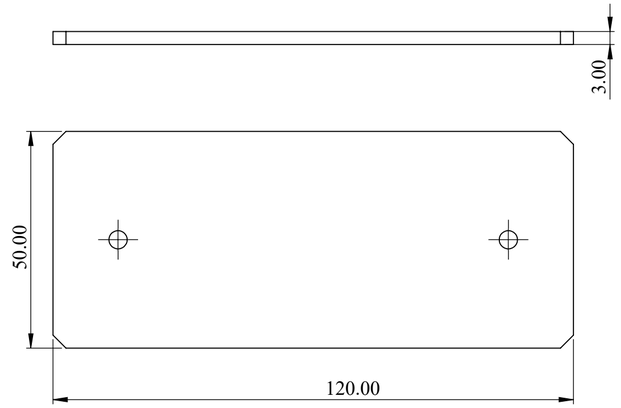

NAME : INTERMEDIATE SUPPORT TUBE WELDING PLATE
SIZE : 50X120X3 MM THK
MTL : AL
QTY FOR 1 PANEL : 72 NOS
QTY FOR 16 PANEL : 1152 NOS
OPERATION : LASER CUTTING

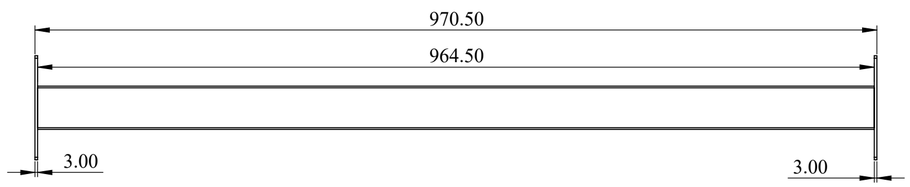

NAME : INTERMEDIATE SUPPORT TUBE
SIZE : 50X50X1.5 MM THK
MTL : AL
QTY FOR 1 PANEL : 36 NOS
QTY FOR 16 PANEL : 576 NOS
OPERATION : CUTTING

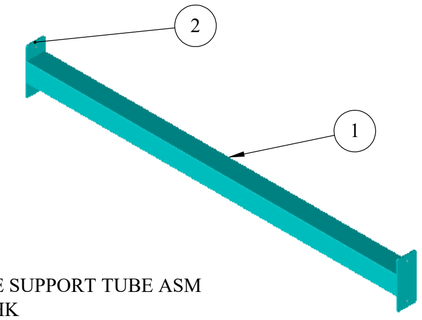

ISO VIEW

NAME : INTERMEDIATE SUPPORT TUBE ASM
SIZE : 50X50X1.5 MM THK
MTL : AL
QTY FOR 1 PANEL : 36 NOS
QTY FOR 16 PANEL : 576 NOS
OPERATION : CUTTING

NOTE :

SPECIAL INSTRUCTION'S :

This drawing & design is the property of NIHVA TECHONOLOGIES PVT. LTD. Not to be sold or copied to any other concern.

TITLE - ROOF AUTOMATION

DWG NO - NTPL-401-PM-01

NIHVA Technologies Pvt. Ltd.

NIHVA TECHNOLOGIES PVT.LTD.PUNE
Website - www.nihva.com


	NAME	SIGNATURE	DATE
DRAWN	V.W.		11-06-2026
CHK'D	S.P.		13-06-2026
APPV'D	V.T.		13-06-2026

PRODUCT - C-SHAPE RETRACTABLE ROOF
PROJECT NO - NTPL-000-PM
REVISION - 00
SITE LOCATION-HYDRABAD
WEIGHT -
MATRIAL -
QTY - 1
SCALE :
PROJECTION METHOD:
If any queries contact - design2@nihva.com
ALL DIMENSION ARE IN mm
A2


DRAWING


ITEM NO.	PART NUMBER	DESCRIPTION	QTY.
1	T PLATE	SS304 -117.5X156X3 MM THK	256

REV DESCRIPTION	DATE	REV NO
	11-06-2026	REV 00
1.		

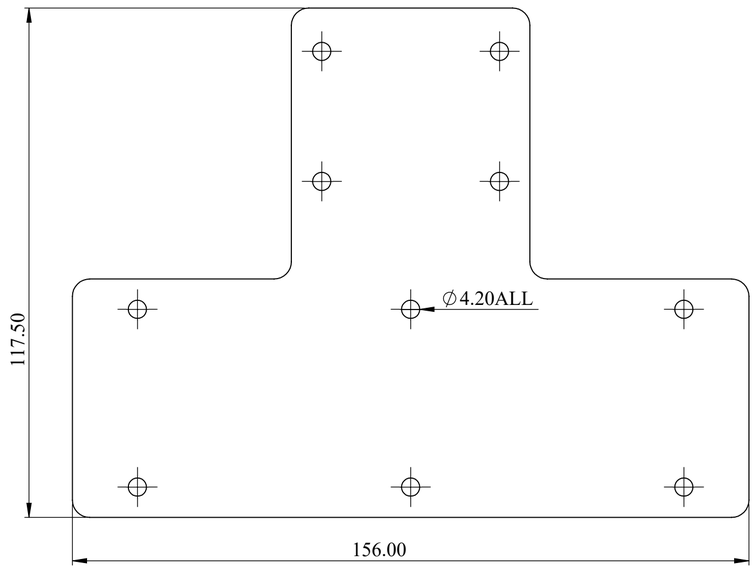

DEVELOPMENT VIEW

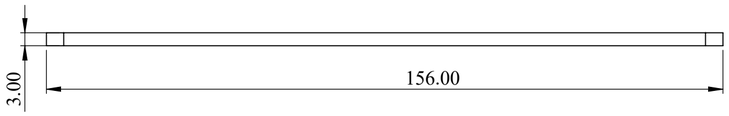

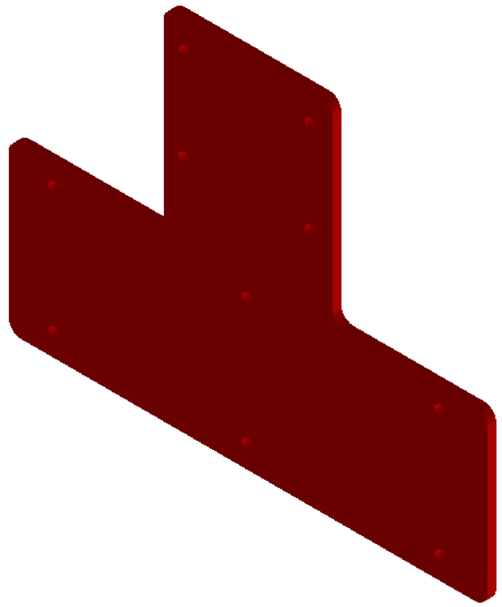

ISO VIEW

NAME : SS T PLATE
SIZE : 117.5X156X3 MM THK
THK : 3MM
MTL : SS
QTY REQ FOR 1 PANEL : 16 NOS
QTY REQ FOR 16 PANEL : 256 NOS.

NOTE :

SPECIAL INSTRUCTION'S :

This drawing & design is the property of NIHVA TECHONOLOGIES PVT. LTD. Not to be sold or copied to any other concern.

TITLE - ROOF AUTOMATION

DWG NO - NTPL-401-PM-01

NIHVA TECHNOLOGIES PVT.LTD.PUNE
Website - www.nihva.com


	NAME	SIGNATURE	DATE
DRAWN	V.W.		11-06-2026
CHK'D	S.P.		13-06-2026
APPV'D	V.T.		13-06-2026

PRODUCT - C-SHAPE RETRACTABLE ROOF
PROJECT NO - NTPL-000-PM
REVISION - 00
SITE LOCATION-HYDRABAD
WEIGHT -
MATRIAL -
QTY - 1
SCALE :
PROJECTION METHOD:
If any queries contact - design2@nihva.com
ALL DIMENSION ARE IN mm
A2


DRAWING


ITEM NO.	PART NUMBER	DESCRIPTION	QTY.
1	L PLATE	SS304- 91X106X3 MM THK	128

REV DESCRIPTION	DATE	REV NO
	11-06-2026	REV 00
1.		

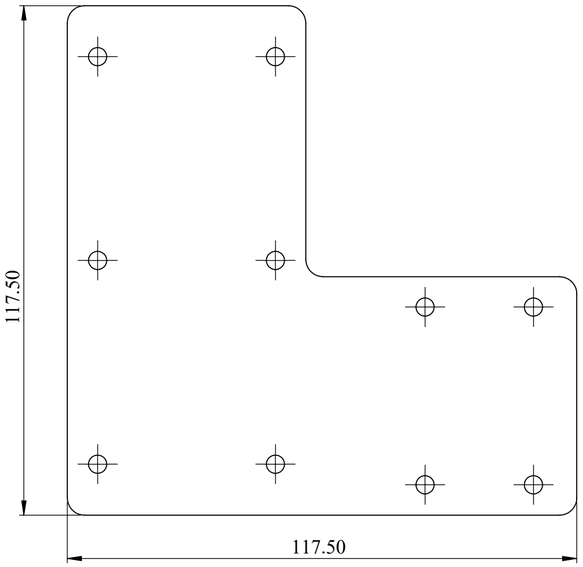

DEVELOPMENT VIEW

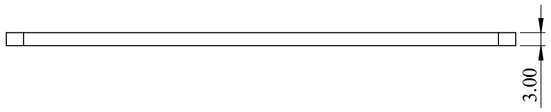

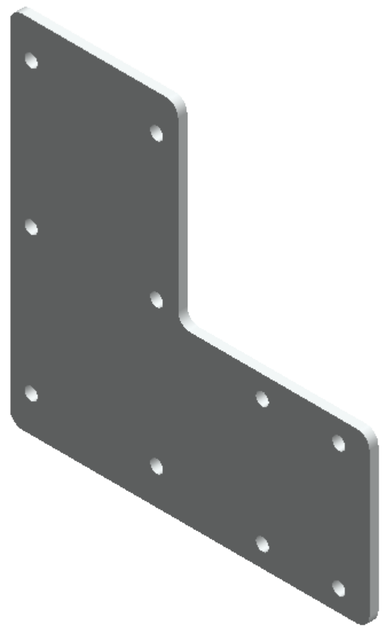

NAME : SS L PLATE
SIZE : 117.5X117.5X3 MM THK
THK : 3MM
MTL : SS
QTY REQ FOR 1 PANEL : 8 NOS
QTY REQ FOR 16 PANEL : 128 NOS.

NOTE :

SPECIAL INSTRUCTION'S :

This drawing & design is the property of NIHVA TECHONOLOGIES PVT. LTD. Not to be sold or copied to any other concern.

TITLE - ROOF AUTOMATION


DWG NO - NTPL-401-PM-01

NIHVA TECHNOLOGIES PVT.LTD.PUNE
Website - www.nihva.com


	NAME	SIGNATURE	DATE
DRAWN	V.W.		11-06-2026
CHK'D	S.P.		13-06-2026
APPV'D	V.T.		13-06-2026

PRODUCT - C-SHAPE RETRACTABLE ROOF
PROJECT NO - NTPL-000-PM
REVISION - 00
SITE LOCATION-HYDRABAD
WEIGHT -
MATRIAL -
QTY - 1
SCALE :
PROJECTION METHOD:
If any queries contact - design2@nihva.com
ALL DIMENSION ARE IN mm
A2

DRAWING

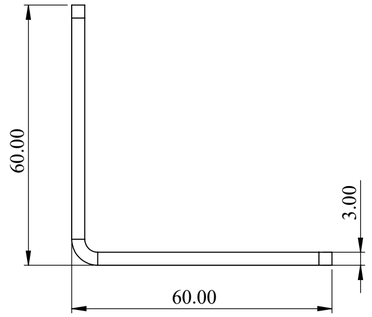


F.V.

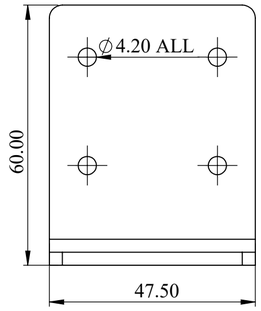


R.S.V

ITEM NO.	PART NUMBER	DESCRIPTION	QTY.
1	L ANGLE PLATE	SS304 - 60X60X3 MM	1

REV DESCRIPTION	DATE	REV NO
	11-06-2026	REV 00
1.		

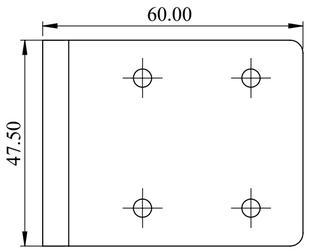


B.V

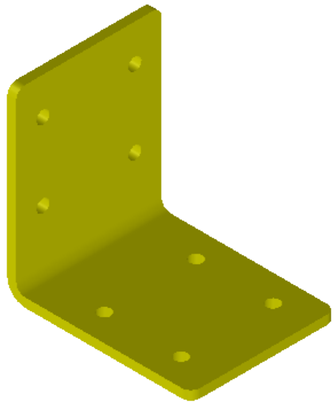

ISO VIEW

NAME : SS L ANGLE PLATE
SIZE : 60X60X3 MM THK
THK : 3MM
MTL : SS
QTY REQ FOR 1 PANEL : 20 NOS
QTY REQ FOR 16 PANEL : 320 NOS.

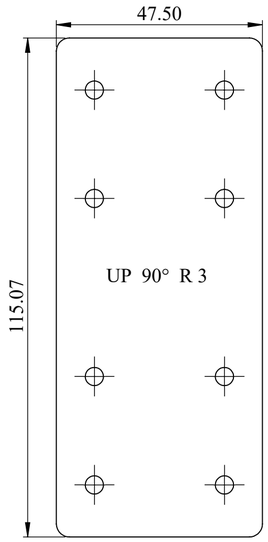

DEVELOPMENT VIEW

NOTE :

SPECIAL INSTRUCTION'S :

This drawing & design is the property of NIHVA TECHONOLOGIES PVT. LTD. Not to be sold or copied to any other concern.

TITLE - ROOF AUTOMATION

DWG NO - NTPL-401-PM-01

NIHVA Technologies Pvt. Ltd.

NIHVA TECHNOLOGIES PVT.LTD.PUNE
Website - www.nihva.com


	NAME	SIGNATURE	DATE
DRAWN	V.W.		11-06-2026
CHK'D	S.P.		13-06-2026
APPV'D	V.T.		13-06-2026


PRODUCT - C-SHAPE RETRACTABLE ROOF
PROJECT NO - NTPL-000-PM
REVISION - 00
SITE LOCATION-HYDRABAD
WEIGHT -
MATRIAL -
QTY - 1
SCALE :
SHEET 13 OF 20
PROJECTION METHOD:
If any queries contact - design2@nihva.com
ALL DIMENSION ARE IN mm
A2


DRAWING

ITEM NO.	PART NUMBER	DESCRIPTION	QTY.
1	L ANGLE WELDING CORNER JOINING PLATE	AL WELDING JOINING PLATE	1

REV DESCRIPTION	DATE	REV NO
	05-06-2026	REV 00
1.		

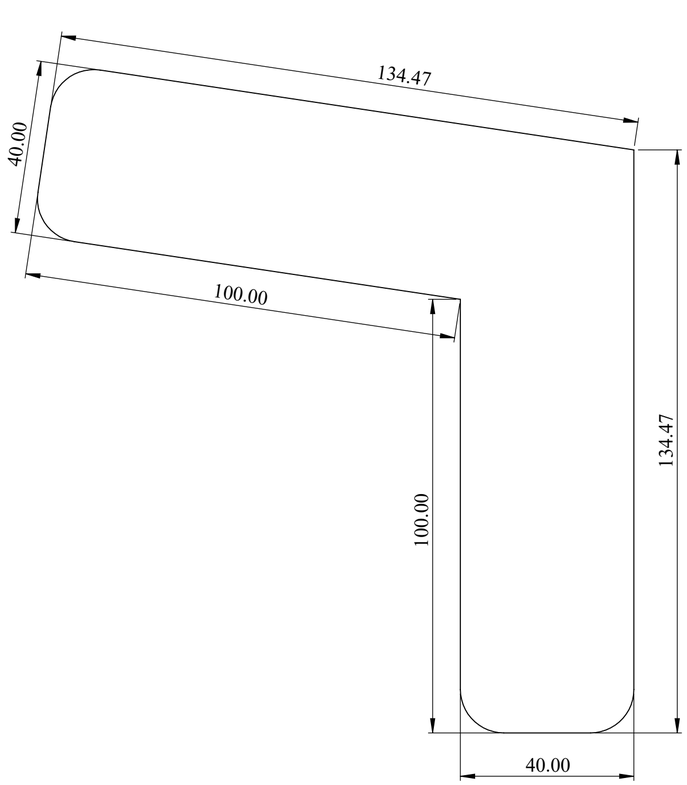

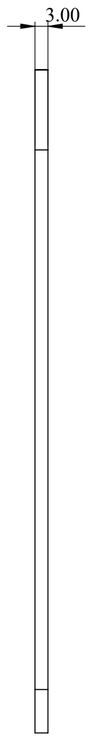

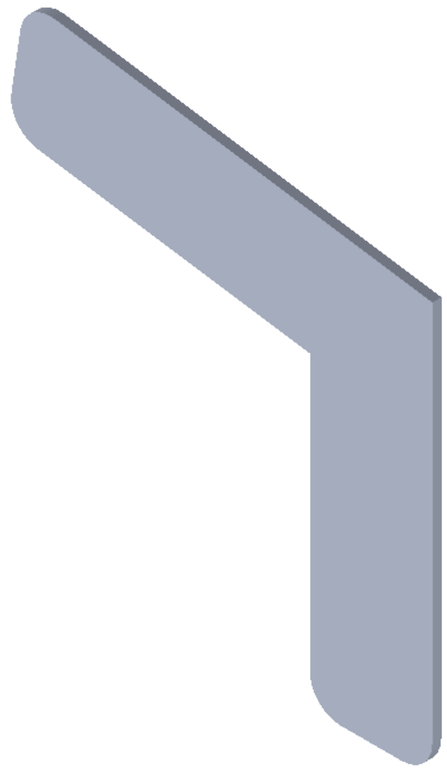

NAME : AL L ANGLE WELDING PLATE
SIZE : 40X100X3 MM THK
THK : 3MM
MTL : AL
QTY REQ FOR 1 PANEL : 24 NOS
QTY REQ FOR 16 PANEL : 384 NOS.

NOTE :

SPECIAL INSTRUCTION'S :

This drawing & design is the property of NIHVA TECHONOLOGIES PVT. LTD. Not to be sold or copied to any other concern.

TITLE - ROOF AUTOMATION


DWG NO - NTPL-401-PM-01

NIHVA TECHNOLOGIES PVT.LTD.PUNE
Website - www.nihva.com


	NAME	SIGNATURE	DATE
DRAWN	V.W.		11-06-2026
CHK'D	S.P.		13-06-2026
APPV'D	V.T.		13-06-2026

PRODUCT - C-SHAPE RETRACTABLE ROOF
PROJECT NO - NTPL-000-PM
REVISION - 00
SITE LOCATION-HYDRABAD
WEIGHT -
MATRIAL -
QTY - 1
SCALE :
PROJECTION METHOD:
If any queries contact - design2@nihva.com
ALL DIMENSION ARE IN mm
A2

DRAWING

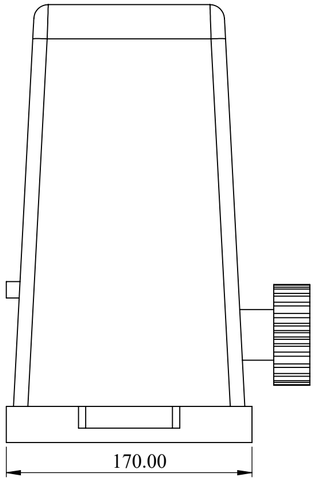


F.V.

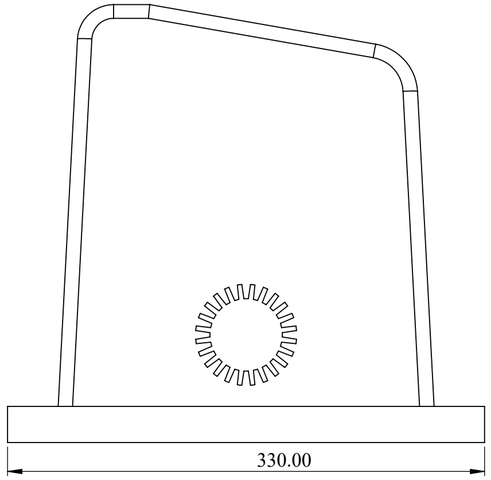


S.V.

ITEM NO.	PART NUMBER	DESCRIPTION	QTY.
1	NICE RB 1T	MOTOR	15

REV DESCRIPTION	DATE	REV NO
	11-06-2026	REV 00
1.		

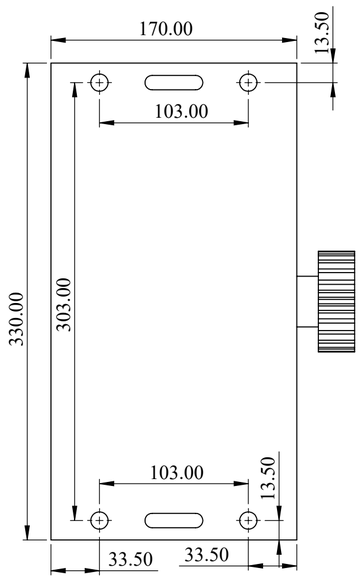

B.V.

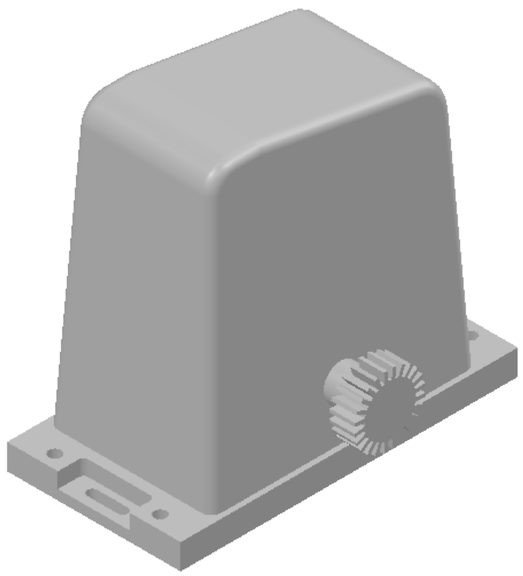

ISO VIEW

NAME : NICE MOTOR
SIZE : 1T
QTY REQ FOR 1 PANEL : 1 NOS
QTY REQ FOR 15 PANEL : 15 NOS.
NOTE : 1 PANEL IS FIX

NOTE :

SPECIAL INSTRUCTION'S :

This drawing & design is the property of NIHVA TECHONOLOGIES PVT. LTD. Not to be sold or copied to any other concern.

TITLE - ROOF AUTOMATION


DWG NO - NTPL-401-PM-01

NIHVA TECHNOLOGIES PVT.LTD.PUNE
Website - www.nihva.com


	NAME	SIGNATURE	DATE
DRAWN	V.W.		11-06-2026
CHK'D	S.P.		13-06-2026
APPV'D	V.T.		13-06-2026

PRODUCT - C-SHAPE RETRACTABLE ROOF
PROJECT NO - NTPL-000-PM
REVISION - 00
SITE LOCATION-HYDRABAD
WEIGHT -
MATRIAL -
QTY - 1
If any queries contact - design2@nihva.com
ALL DIMENSION ARE IN mm
A2
PROJECTION METHOD:
SCALE :
SHEET 15 OF 20


DRAWING

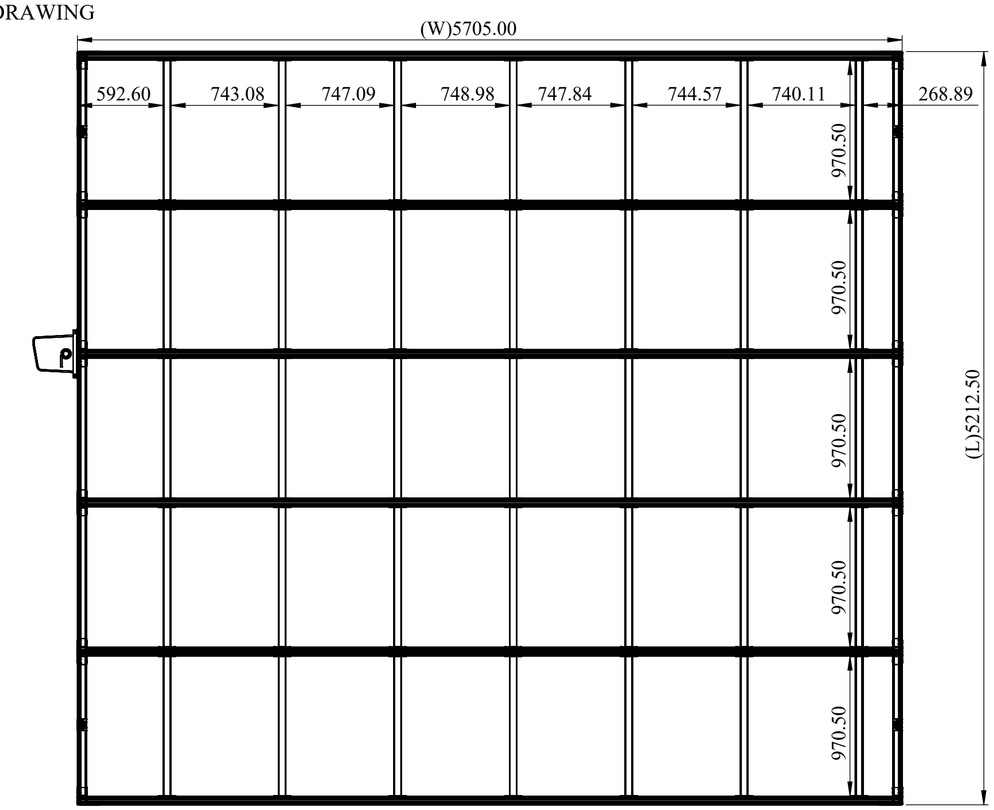

T.V.

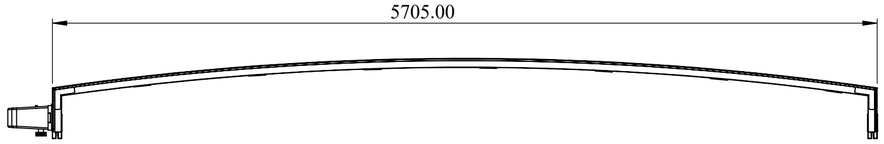

F.V.

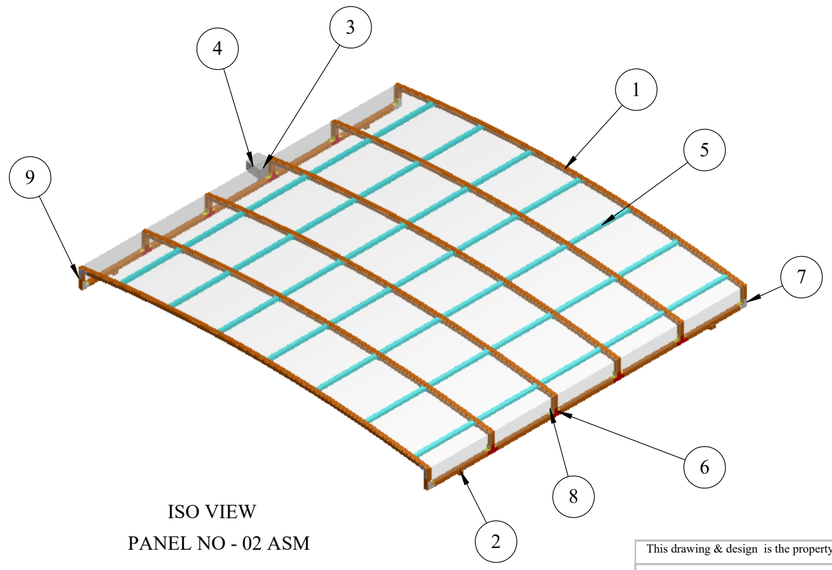

ISO VIEW

PANEL NO - 02 ASM

ITEM NO.	PART NUMBER	DESCRIPTION	QTY.
1	PANEL - 2		1
2	BEARING BLOCK ASM _ T75_1B. - 2		4
3	MOTOR BASE PLATE	AL	1
4	NICE RB 1T	MOTOR	1
5	INTERMEDIATE SUPPORT TUBE ASM . - 2		35
6	T PLATE	SS304 -117.5X156X3 MM THK	16
7	L PLATE	SS304- 91X106X3 MM THK	8
8	L ANGLE PLATE	SS304 - 60X60X3 MM	20
9	L ANGLE WELDING CORNER JOINING PLATE	AL WELDING JOINING PLATE	24

REV DESCRIPTION	DATE	REV NO
	11-06-2026	REV 00
1.		

NOTE :

NAME : PANEL NO - 02 ASM
PROFILE : AL GNTOO6
QTY : 04 NOS

SPECIAL INSTRUCTION'S :

This drawing & design is the property of NIHVA TECHONOLOGIES PVT. LTD. Not to be sold or copied to any other concern.

TITLE - ROOF AUTOMATION


DWG NO - NTPL-401-PM-01

NIHVA Technologies Pvt. Ltd.

NIHVA TECHNOLOGIES PVT.LTD.PUNE
Website - www.nihva.com


	NAME	SIGNATURE	DATE		
DRAWN	V.W.		11-06-2026	PRODUCT - C-SHAPE RETRACTABLE ROOF	
CHK'D	S.P.		13-06-2026	PROJECT NO - NTPL-000-PM	REVISION - 00
APPV'D	V.T.		13-06-2026	SITE LOCATION-HYDRABAD	WEIGHT -
				MATRIAL -	QTY - 1
If any queries contact - design2@nihva.com				PROJECTION METHOD:	SCALE :
ALL DIMENSION ARE IN mm		A2			SHEET 16 OF 20

DRAWING

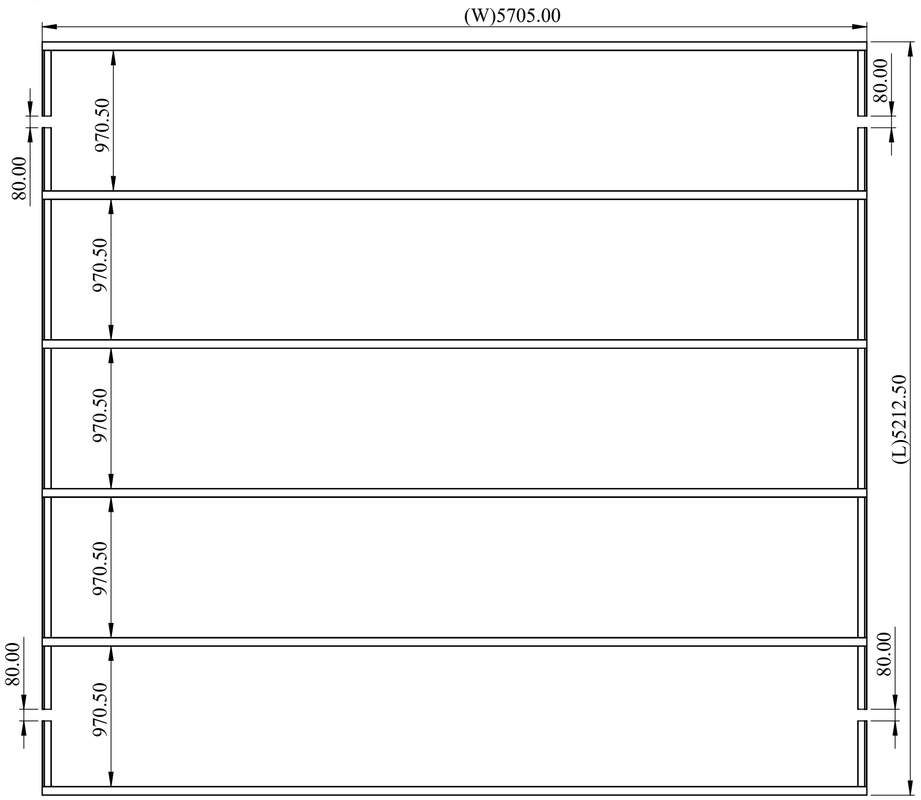


T.V.

ITEM NO.	PART NUMBER	DESCRIPTION	QTY.
1	PANEL - 2		04

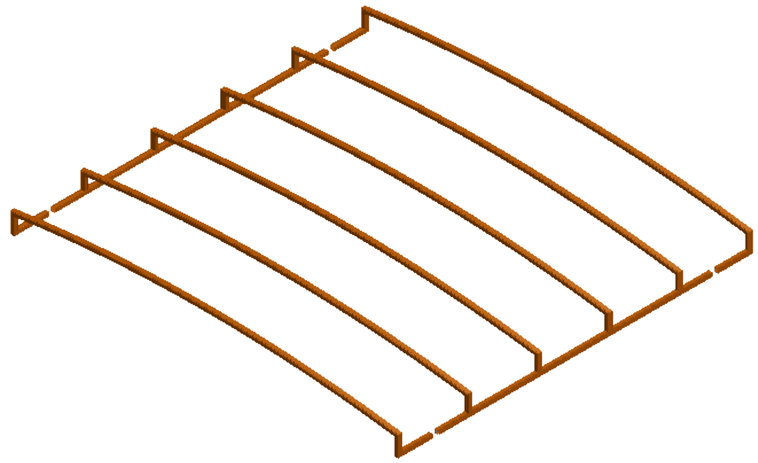


ISO VIEW
PANEL NO - 02


REV DESCRIPTION	DATE	REV NO
	11-06-2026	REV 00
1.		

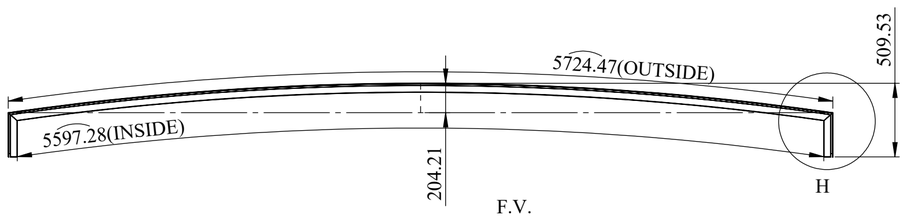


F.V.

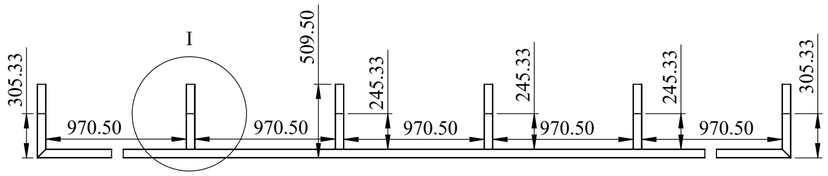

R.S.V.

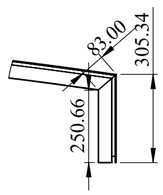

DETAIL H
SCALE 1 : 15

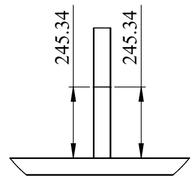

DETAIL I
SCALE 1 : 15

NOTE :


NAME : PANEL NO - 02
PROFILE : AL GNTOO6 (60X63)
QTY : 04 NOS.

SPECIAL INSTRUCTION'S :

This drawing & design is the property of NIHVA TECHONOLOGIES PVT. LTD. Not to be sold or copied to any other concern.

TITLE - ROOF AUTOMATION				NIHVA TECHNOLOGIES PVT.LTD.PUNE Website - www.nihva.com	
DWG NO - NTPL-401-PM-01					
	NAME	SIGNATURE	DATE	PRODUCT - C-SHAPE RETRACTABLE ROOF	
DRAWN	V.W.		11-06-2026	PROJECT NO - NTPL-000-PM	REVISION - 00
CHK'D	S.P.		13-06-2026	SITE LOCATION-HYDRABAD	WEIGHT -
APPV'D	V.T.		13-06-2026	MATRIAL -	QTY - 1
If any queries contact - design2@nihva.com				PROJECTION METHOD:	SCALE :
ALL DIMENSION ARE IN mm			A2		SHEET 17 OF 20

DRAWING

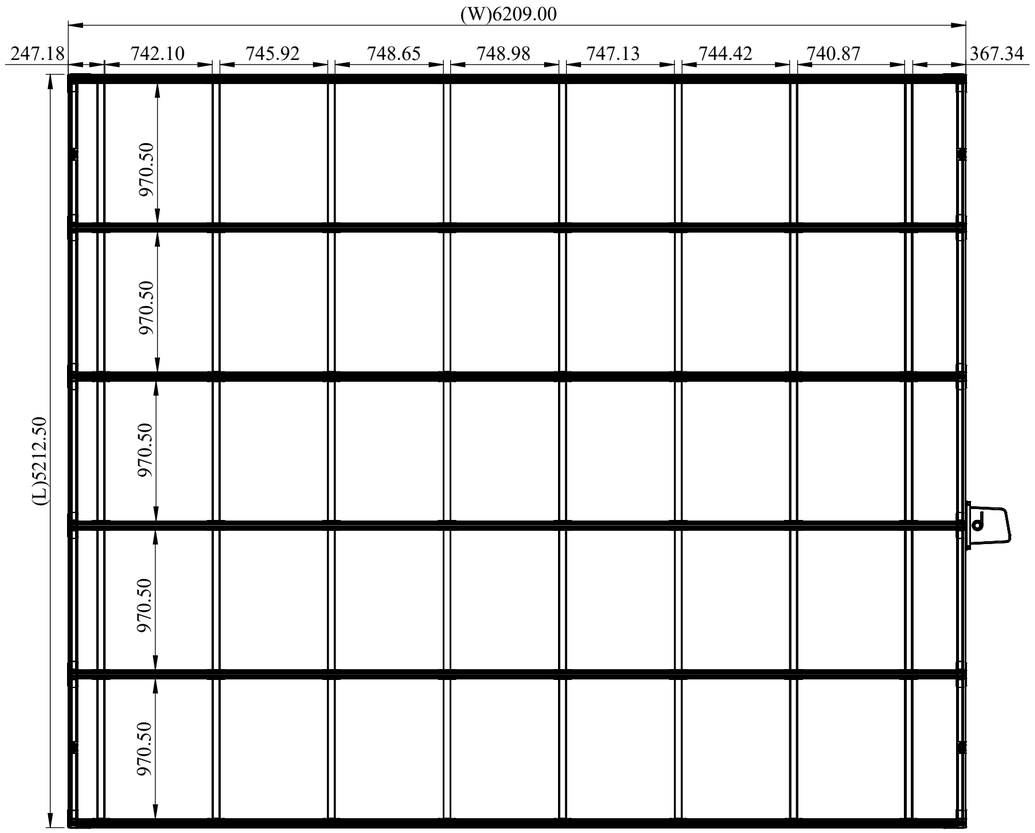


T.V.

ITEM NO.	PART NUMBER	DESCRIPTION	QTY.
1	PANEL - 3		1
2	BEARING BLOCK ASM _ T75_1B. - 3		4
3	MOTOR BASE PLATE	AL	1
4	NICE RB 1T	MOTOR	1
5	INTERMEDIATE SUPPORT TUBE ASM . - 3		40
6	T PLATE	SS304 -117.5X156X3 MM THK	16
7	L PLATE	SS304- 91X106X3 MM THK	8
8	L ANGLE PLATE	SS304 - 60X60X3 MM	20
9	L ANGLE WELDING CORNER JOINING PLATE	AL WELDING JOINING PLATE	24

REV DESCRIPTION	DATE	REV NO
	11-06-2026	REV 00
1.		



F.V.

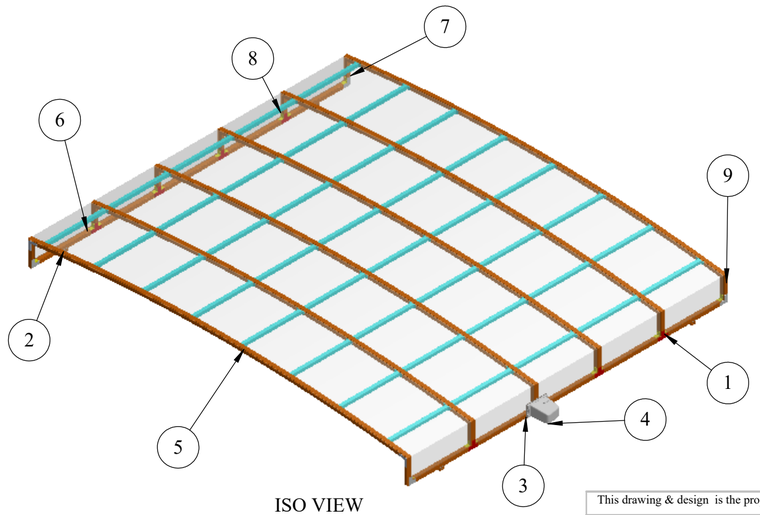

ISO VIEW
PANEL NO - 03 ASM

NOTE :

NAME : PANEL NO - 03 ASM
PROFILE : AL GNTOO6
QTY : 04 NOS

SPECIAL INSTRUCTION'S :

This drawing & design is the property of NIHVA TECHONOLOGIES PVT. LTD. Not to be sold or copied to any other concern.

TITLE - ROOF AUTOMATION


DWG NO - NTPL-401-PM-01

NIHVA TECHNOLOGIES PVT.LTD.PUNE
Website - www.nihva.com


	NAME	SIGNATURE	DATE
DRAWN	V.W.		11-06-2026
CHK'D	S.P.		13-06-2026
APPV'D	V.T.		13-06-2026

PRODUCT - C-SHAPE RETRACTABLE ROOF
PROJECT NO - NTPL-000-PM
REVISION - 00
SITE LOCATION-HYDRABAD
WEIGHT -
MATRIAL -
QTY - 1
SCALE :
PROJECTION METHOD:
If any queries contact - design2@nihva.com
ALL DIMENSION ARE IN mm
A2

DRAWING

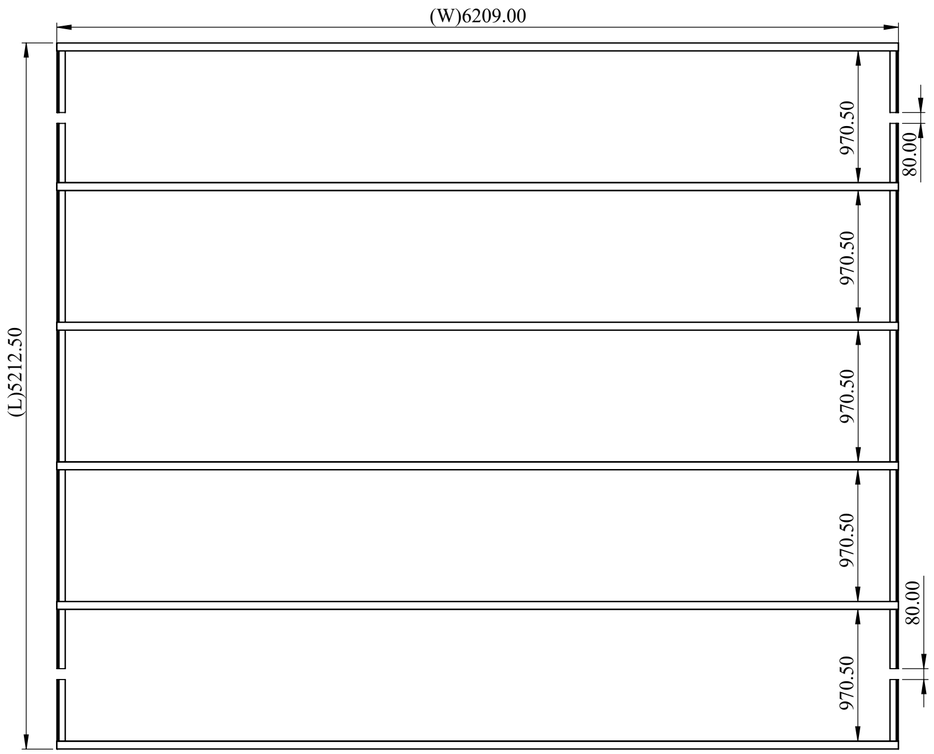


ITEM NO.	PART NUMBER	DESCRIPTION	QTY.
1	PANEL - 3		04

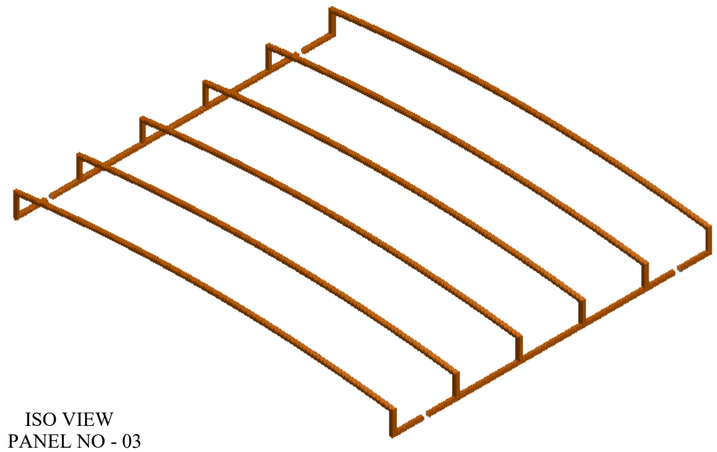


ISO VIEW
PANEL NO - 03


REV DESCRIPTION	DATE	REV NO
	11-06-2026	REV 00
1.		

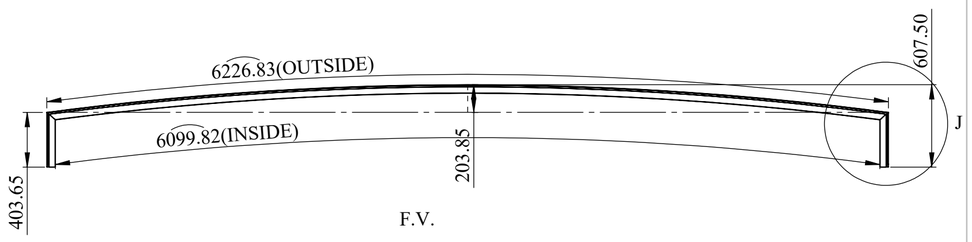

F.V.

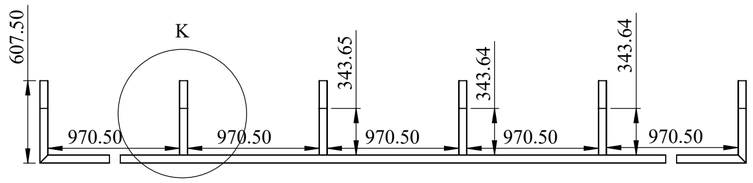


R.S.V.

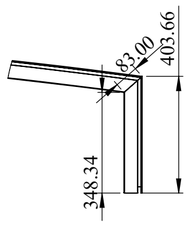

DETAIL J
SCALE 1 : 15

T.V.

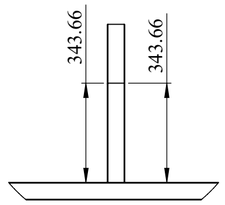

DETAIL K
SCALE 1 : 15

NOTE :

NAME : PANEL NO - 03
PROFILE : AL GNTOO6 (60X63)
QTY : 04 NOS.

SPECIAL INSTRUCTION'S :

This drawing & design is the property of NIHVA TECHONOLOGIES PVT. LTD. Not to be sold or copied to any other concern.

TITLE - ROOF AUTOMATION

DWG NO - NTPL-401-PM-01


NIHVA TECHNOLOGIES PVT.LTD.PUNE
Website - www.nihva.com


	NAME	SIGNATURE	DATE
DRAWN	V.W.		11-06-2026
CHK'D	S.P.		13-06-2026
APPV'D	V.T.		13-06-2026

PRODUCT - C-SHAPE RETRACTABLE ROOF
PROJECT NO - NTPL-000-PM
REVISION - 00
SITE LOCATION-HYDRABAD
WEIGHT -
MATRIAL -
QTY - 1
If any queries contact - design2@nihva.com
PROJECTION METHOD:
SCALE :
ALL DIMENSION ARE IN mm
A2

DRAWING

ITEM NO.	PART NUMBER	DESCRIPTION	QTY.
1	RACK	STD (1 M LENGTH)	225

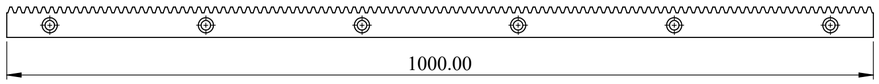

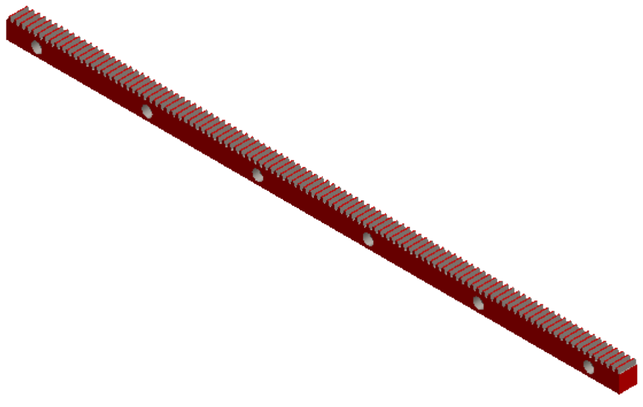

NAME : RACK
SIZE : M6 MODULE (30X30X8 MM)
QTY REQUIRED FOR 1 PANEL : 15 NOS
QTY REQUIRED FOR 15 PANEL : 225 NOS

REV DESCRIPTION	DATE	REV NO
	11-06-2026	REV 00
1.		

NOTE :

SPECIAL INSTRUCTION'S :

This drawing & design is the property of NIHVA TECHONOLOGIES PVT. LTD. Not to be sold or copied to any other concern.

TITLE - ROOF AUTOMATION

DWG NO - NTPL-401-PM-01

NIHVA TECHNOLOGIES PVT.LTD.PUNE
Website - www.nihva.com

	NAME	SIGNATURE	DATE
DRAWN	V.W.		11-06-2026
CHK'D	S.P.		13-06-2026
APPV'D	V.T.		13-06-2026

PRODUCT - C-SHAPE RETRACTABLE ROOF
PROJECT NO - NTPL-000-PM
REVISION - 00
SITE LOCATION-HYDRABAD
WEIGHT -
MATRIAL -
QTY - 1
If any queries contact - design2@nihva.com
PROJECTION METHOD:
SCALE :
ALL DIMENSION ARE IN mm
A2