
Revision		Date	By
A	Customer steel and measurements added.	2022-01-18	MA



SECTION A-A

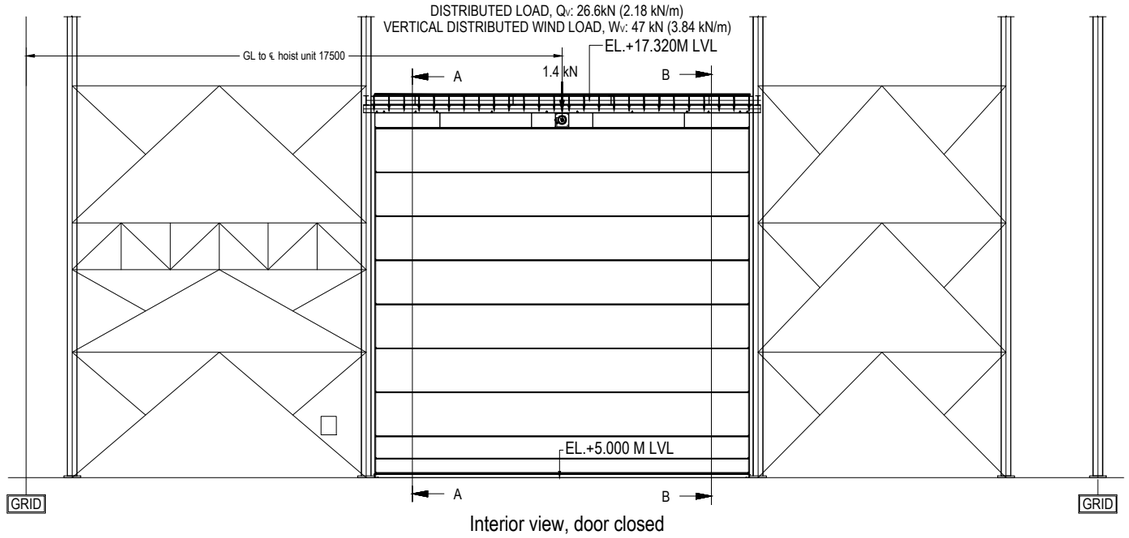

Interior view, door closed

ELEVATION VIEW - EAST SIDE MEGA DOOR ARRANGEMENT

(SCALE 1:100)

LOAD DIAGRAM
Nominal static vertical loads are indicated. Values within brackets { }
include dynamic surload factor 1.25 for door leaf loads in open position.
Includes items provided by ASSA ABLOY only.



SECTION B-B


NOT INCLUDED IN DOOR SUPPLY:
1. Design and supply of all door supporting structural components.
2. Design and supply of all closure between door and adjacent steel.
3. Design and supply of coverage, such as roofing or enclosure, for door components at door head.
4. Door jambs adjustable for overall door width and true to plumb.
5. Paint job after completed door installation.
6. Any frameworks being provided by ASSA ABLOY will be clearly indicated as "by ASSA ABLOY".

REQUIREMENTS ON BUILDING:
7. Door head support must be straight within 1/600 of span in the in/out direction and free from protrusions of any kind.
8. For a single door leaf, door head support should be horizontal and straight within 1/600 of span at distributed full door load.
9. Door side jambs must be smooth, straight and parallel, out of plumb must not exceed 2mm/m (total deviation at full length 5 mm) in any direction.
10. Any footings at bottom of jamb columns must not interfere with installation of guide rails at floor level.
11. At time of installation, finished floor, free from obstructions, out to a distance of 2 m on each side of door centreline must be available.
12. Header box must be accessible from both sides during installation.

DOOR PROPERTIES:
13. The door is designed to withstand a differential pressure of 1.2kPa.
14. Guide rails, top- and intermediate beams in extruded aluminium with natural finish.
15. Environmental category: C5 according to ISO 12944-2
16. Bottom beam in carbon steel painted: Light grey (RAL7047)
17. Colored clamp strips on both sides: Grey
18. Door header box enclosed on both sides.
19. Color of header box: BLACK (NCS 9000-N. RAL 9005)
20. The door fabric is a UV stabilized, flame retardant, self-extinguishing, PVC coated polyester fabric with fire technical properties Euroclass B-s2, d0 (according to EN 13501-1:2007).
21. Colour of fabric: GREY (NCS 3500, RAL 7004)

ELECTRICAL:
22. One main control panel provided of PLC type.
23. Control mode : Impulse up / Constant contact down.
24. Cables are included.
25. Back-up power socket & switch.
26. Audible & visual alarm.
27. Wind-lock indication.
28. Approx. size of main control panel: WxHxD (500x600x250mm),
29. Location of main control panel: Please specify location.
30. Aux. Voltage 24VDC
31. Power supply: 415V /3Ph /50Hz
32. Power: 5.0kW
33. Nom. current: 11.3A
34. Start current: 65.0A
(max. allowed voltage drop at start: 5%)

BELT HOIST UNITS:
RE 513 TK ME112 Dual brake
75mm wide polyester belt.

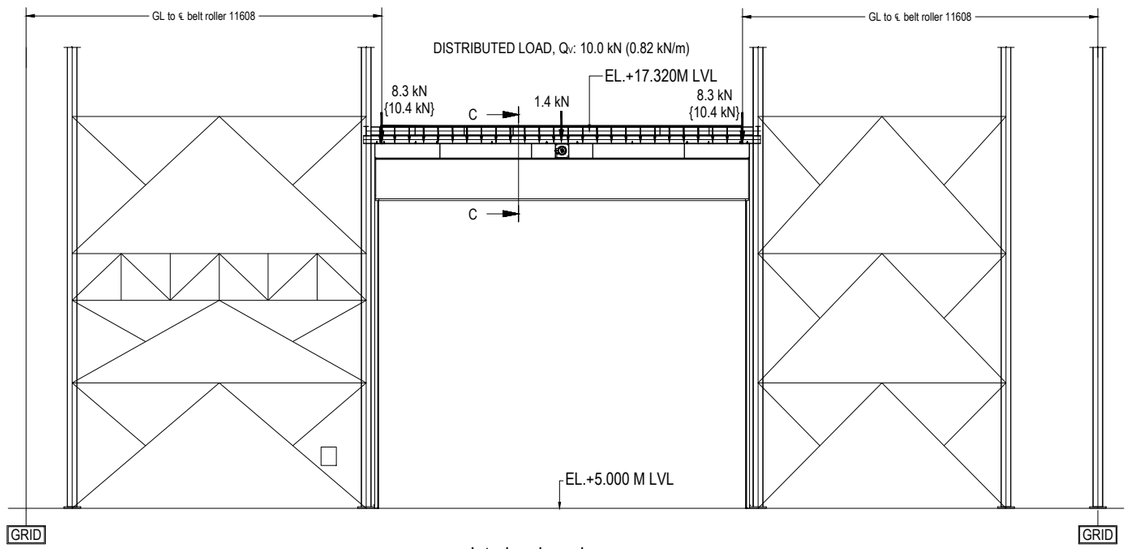

Interior view, door open

ELEVATION VIEW - EAST SIDE MEGA DOOR ARRANGEMENT

(SCALE 1:100)



SECTION C-C
(1 : 50)

DOOR IDENTITY NUMBER: 84705001-004

INTERFACE, ref. to drwng. no. 74450

DESIGNED FV	SIZE A1	SCALE 1:100	Seabird Karwar
CODE 84705	If not otherwise stated: Tolerances ISO 2768-m EN ISO 13920-B		India
ITEM NO	Cutting class ISO 9013-442		Megadoor 12000 x 10000
DATE 2022-01-14	Weld class ISO 5817-C		Load diagram & notes
ASSA ABLOY	Surface finish Smooth raw surface	DRAWING NO 74451	REVISION A

PLOT DATE

This document is the property of ASSA ABLOY Entrance Systems AB and shall not be reproduced or copied without permission. It is not to be imparted to a third party or used for any other unauthorized purpose.