

WALL MOUNTED DOUBLE WALL ROLLING SHUTTER FITTED FROM INSIDE

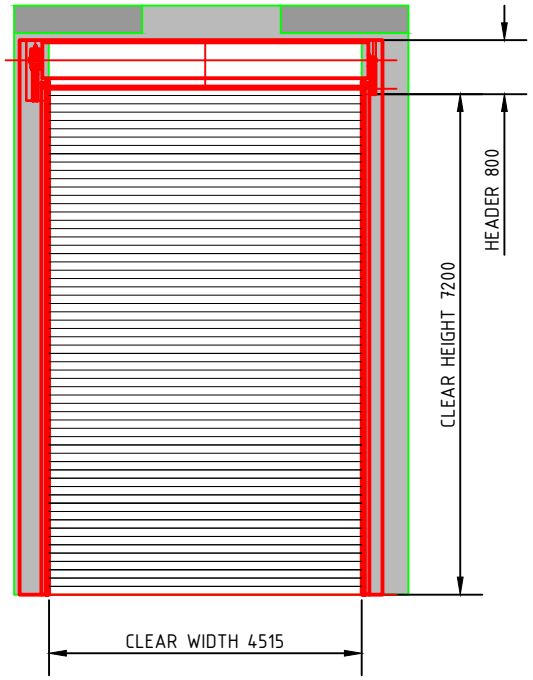


REQUIRED CLEAR SIZE 4515 X 8000
ACTUAL CLEAR SIZE 4515 X 7200

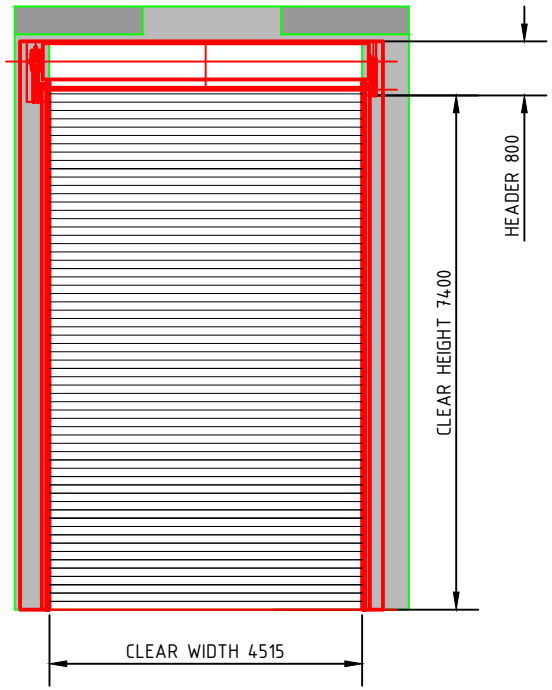

REQUIRED CLEAR SIZE 4515 X 8200
ACTUAL CLEAR SIZE 4515 X 7400



Main Slats
Double Wall Rolling Shutter

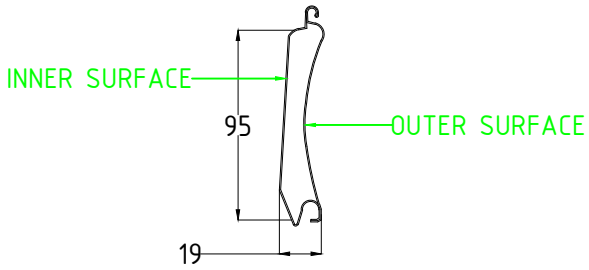

DIMENSION :

CLEAR WIDTH	CLEAR HEIGHT	QUANTITY
4515 mm	7400 mm	
4515 mm	7200 mm	

MATERIAL :

THICKNESS :

NOTE:-
1. THIS IS A REFERENCE DRAWING.
2. THIS DRAWING REPRESENTS THE FITMENT OF ROLLING ON INNER WALL.
3. CLEAR HEIGHT WILL BE REDUCED BY 800 MM BECAUSE OF THE UNAVAILABILITY OF THE STRUCTURE FOR HEADER MOUNTING.

NIHVA TECHNOLOGIES PVT. LTD.
NIHVA TECHNOLOGIES PVT. LTD. PUNE
Email:- info@nihva.com
Website:- www.nihva.com

TITLE:

DOUBLE WALL ROLLING SHUTTER FITTED FROM INSIDE

CLIENT'S APPROVAL :

CLIENT - SEZ BIOTECH

PROJECT -

SITE LOCATION - PUNE

DWG. NO. : NIHVA/20-21/0205/ REF-IN

SCALE: NTS	WT:	SHEET:1 OF 1
DRAWN BY: G.P.		DATE: 09-09-2021
CHECKED BY: A.K.		DATE: 09-09-2021
APPROVED BY : V.T.		DATE: 09-09-2021

If any queries contact : design@nihva.com

NOTE: ALL DIMENSIONS ARE IN mm

THIS DRAWING & DESIGN IS THE PROPERTY OF NIHVA TECHNOLOGIES. NOT TO BE SOLD OR COPIED TO ANY OTHER CONCERN.