6000MM WIDE CANOPY(TYP.)
230MM THK. 3500MM HEIGHT BRICK WALL ABOVE CLADDING SHEET (TYP.)
600X1800MM WIDE DOOR CANOPY (TYP.)
WORKER FACILITY
JANITOR
pantry
store
PACKING, FINISH GOODS & DISPATCH
-0.450 F.F.L
+0.900 F.F.L
± 0.000 F.F.L
RAMP UP
UP
15 TON HOOK HT. 07.50 MT.
4500MM WIDE CANOPY
2000MM WIDE CANOPY (TYP.)
04
SLITTING SHED
D101 A.4.201
D102 A.4.201
RS101 A.4.201
RS102 A.4.201
W101 A.4.201
G
F
E
D
C
B
A
11000
11000
7650
7650
7650
7640
53540
±54040
705
7500
120000
±121450
1
2
3
4
5
6
7
8
9
10
11
12
13
14
15
16
17

1 GROUND FLOOR PLAN
SCALE 1:150

THIS DRAWING & DESIGN IS THE SOLE PROPERTY OF VMS & SHALL NOT BE COPIED, TRACED OR REPRODUCED BY ANY MEANS WITHOUT PRIOR WRITTEN CONSENT OF THE FIRM.

GENERAL NOTES :

1. ALL THE DIMENSIONS ARE UNFINISHED DIMENSIONS.
2. ALL DIMENSIONS ARE IN MM AND LEVELS ARE IN MT, UNLESS OTHERWISE MENTIONED.
3. ALL THE DIMENSIONS SHALL BE READ & NOT TO BE MEASURED.
4. IN CASE OF ANY DISCREPANCY, BRING IT TO THE NOTICE OF THE ARCHITECT IMMEDIATELY.
5. DETAIL DRAWING PRECEDES THE GENERAL DRAWING

SCHEDULE OF OPENINGS:

MKD.	SIZE	SILL HT.	LINTEL HT.	TOTAL NO.	REMARKS
D101	1200x2400	----	2400	15	FIRE DOOR
RS101	4000x4500	----	4500	2	ROLLING SHUTTER
RS102	3500x4500	----	4500	4	ROLLING SHUTTER
W101	3000x1500	900	2400	32	ALU. FRAME WITH FIXED ALU. LOUVERS WINDOW

FOR TENDER

NO.	DATE	DESCRIPTION	DRAWN BY	CHECKED BY
R0	-	-	-	-

REVISION HISTORY

KEY PLAN
SCALE : N.T.S.

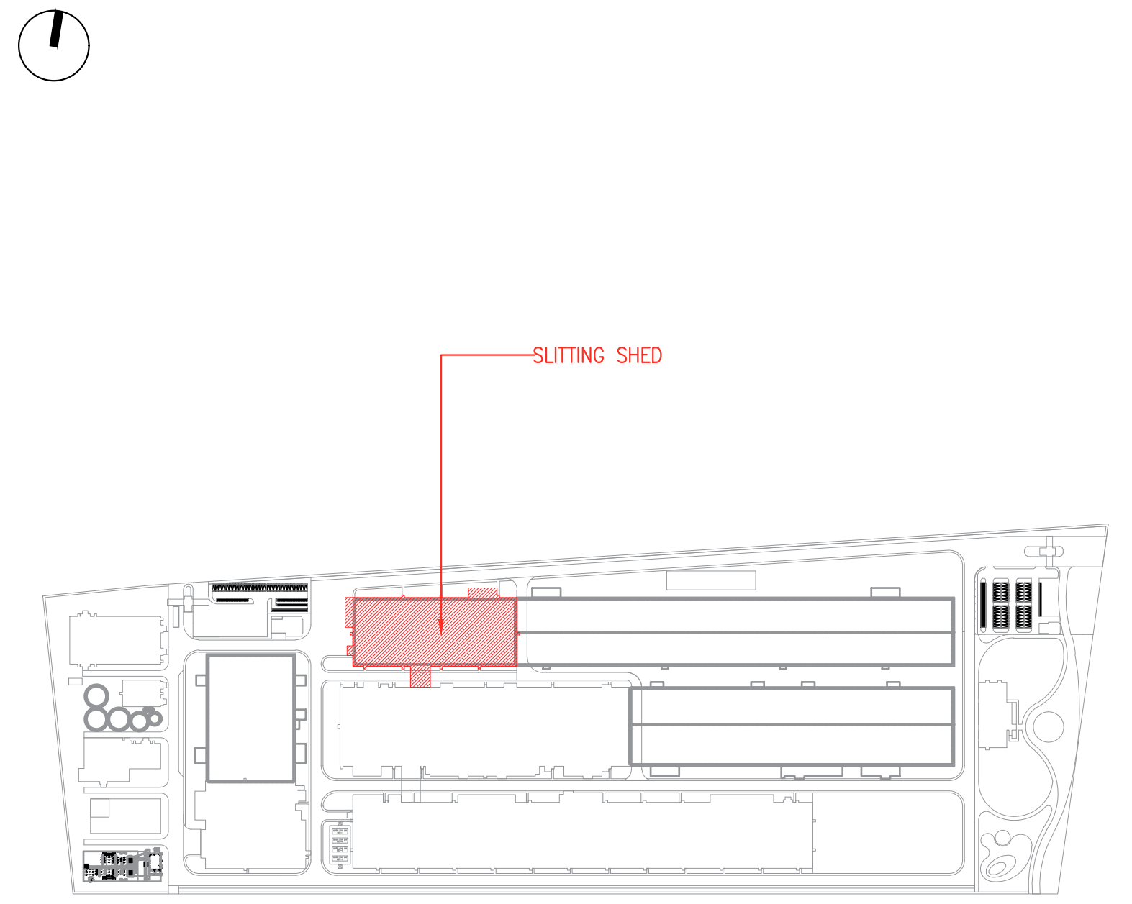
SLITTING SHED

REFERENCE DRAWINGS :

01. ARCHITECTURAL : -
02. STRUCTURAL : -
03. HVAC : -
04. ELECTRICAL : -
05. UTILITIES : -

GROUND FLOOR PLAN

SLITTING SHED

AGRAWAL METAL WORKS(P) LTD.

PROJECT NO.	SCALE :	DRAWN :	SURENDER Y.
3824	AS SHOWN	CHECKED:	BHAKTI B.
	DATE : 03-12-2024	APPROVED:	DARSH D.
		COORDINATION CHECKED:	DARSH D.

VMS
ENGINEERING + ARCHITECTURE
VMS ENGINEERING & DESIGN SERVICES (P) LTD.
CHITRAKOOT FLATS, B/H TIMES OF INDIA, OFF ASHRAM ROAD,
AHMEDABAD-380 009. PHONE: +91 (079) 2658-8829, 4023-6236
WWW.VMSCONSULTANTS.COM

SHEET SIZE	DRAWING NO.	TENDER	REVISION:
600x 1200	T.A.4.101	T	R0