
BOM			
SL NO.	DESCRIPTION	SPECIFICATION	QTY
1	MS SQ. TUBE	72X72X3.2X1650L	2NOS
2	MS SQ. TUBE	72X72X3.2X1430L	2NOS
3	MS SQ. TUBE	30X30X2.6X1506L	3 NOS

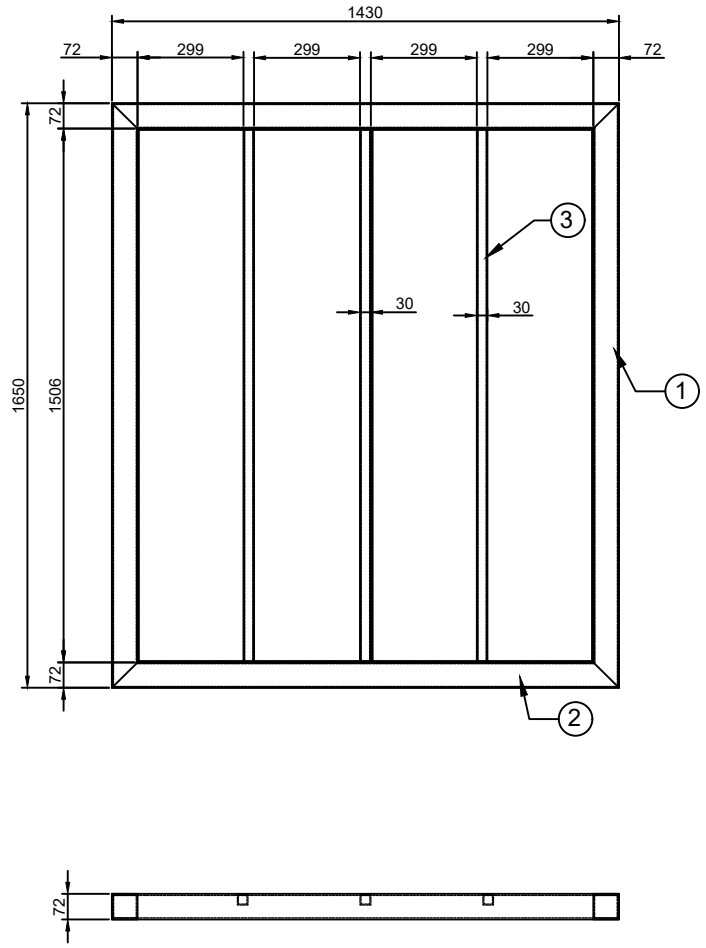

Note:-

1.All Dimension are in MM

2.Kindly Mentain the given Dimensions

Rev No.	Revision	Date	Revised By

This drawing & design is the property of NIHVA TECHNOLOGIES. Not to be sold or copied to any other concern.

TITLE:- WICKET GATE

	NAME	DATE	SIGN
DRAWN	SUJATA.B	11/08/2022	
CHECK			
APPRD.	AMIT.K	11/08/2022	

If any queries contact : design@nihva.com

ALL DIMENSION ARE IN mm

NIHVA TECHNOLOGIES PVT. LTD.
NIHVA TECHNOLOGIES PVT. PUNE
Tel : 020 66304033
Email:- info@nihva.com
Website:- www.nihva.com

CLIENT -

LOCATION -

PRODUCT - WICKET GATE | QTY:00

DWG NO:-NIHVA/22-23/MFG/0108 | REV- 0

SCALE: NTS | SCALE:-- 1:1 | SHEET: 01 OF 01