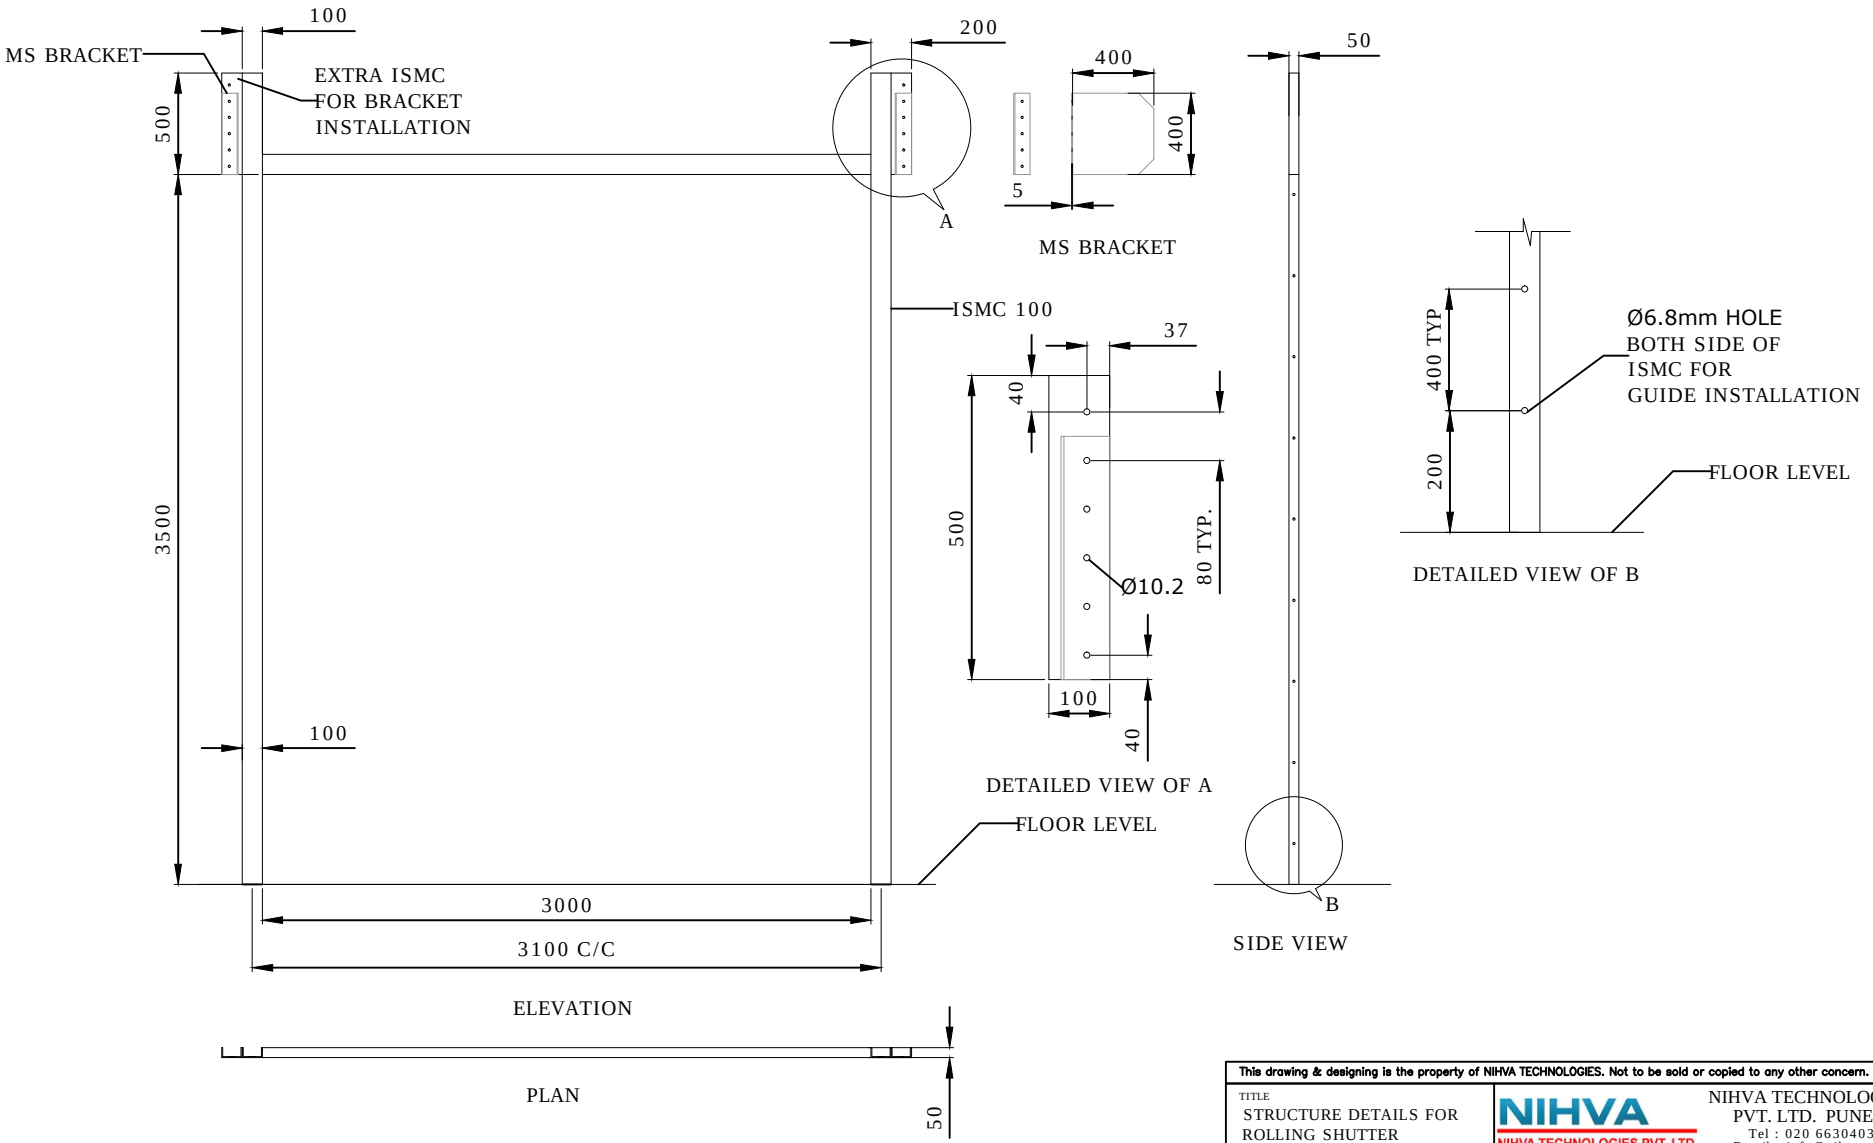

CLEAR WIDTH (CW)	CLEAR HEIGHT (CH)	QUANTITY
3000	3500	7

REV NO	DATE	DESCRIPTION
REV 0	21-11-2017	INITIAL DRAWING
REV 1	22-11-2017	HOLE SIZE 12 CHANGED TO 10.2mm HOLE SIZE 10 CHANGED TO 6.8mm HOLE C/C DISTANCE 200 CHANGED 400mm

This drawing & designing is the property of NIHVA TECHNOLOGIES. Not to be sold or copied to any other concern.

TITLE
STRUCTURE DETAILS FOR ROLLING SHUTTER

	SIGN	DATE
DRAWN	OMKAR	21/11/17
CHECK	SHEKHAR	21/11/17
APPROVAL	SHEKHAR	21/11/17
MFG.		

If any queries contact : design@nihva.com

ALL DIMENSION ARE IN mm

NIHVA
NIHVA TECHNOLOGIES PVT. LTD.
NIHVA TECHNOLOGIES PVT. LTD. PUNE
Tel : 020 66304033
Email:- info@nihva.com
Website:- www.nihva.com

CLIENT - MITTAL PRECISION HITECH STEEL PVT.LTD

PROJECT -

SITE - CHAKAN,PUNE

DWG. NO. : NIHVA/17-18/0285/R01 | REV-1

SCALE: NTS | WT: | SHEET: 01 OF 01