
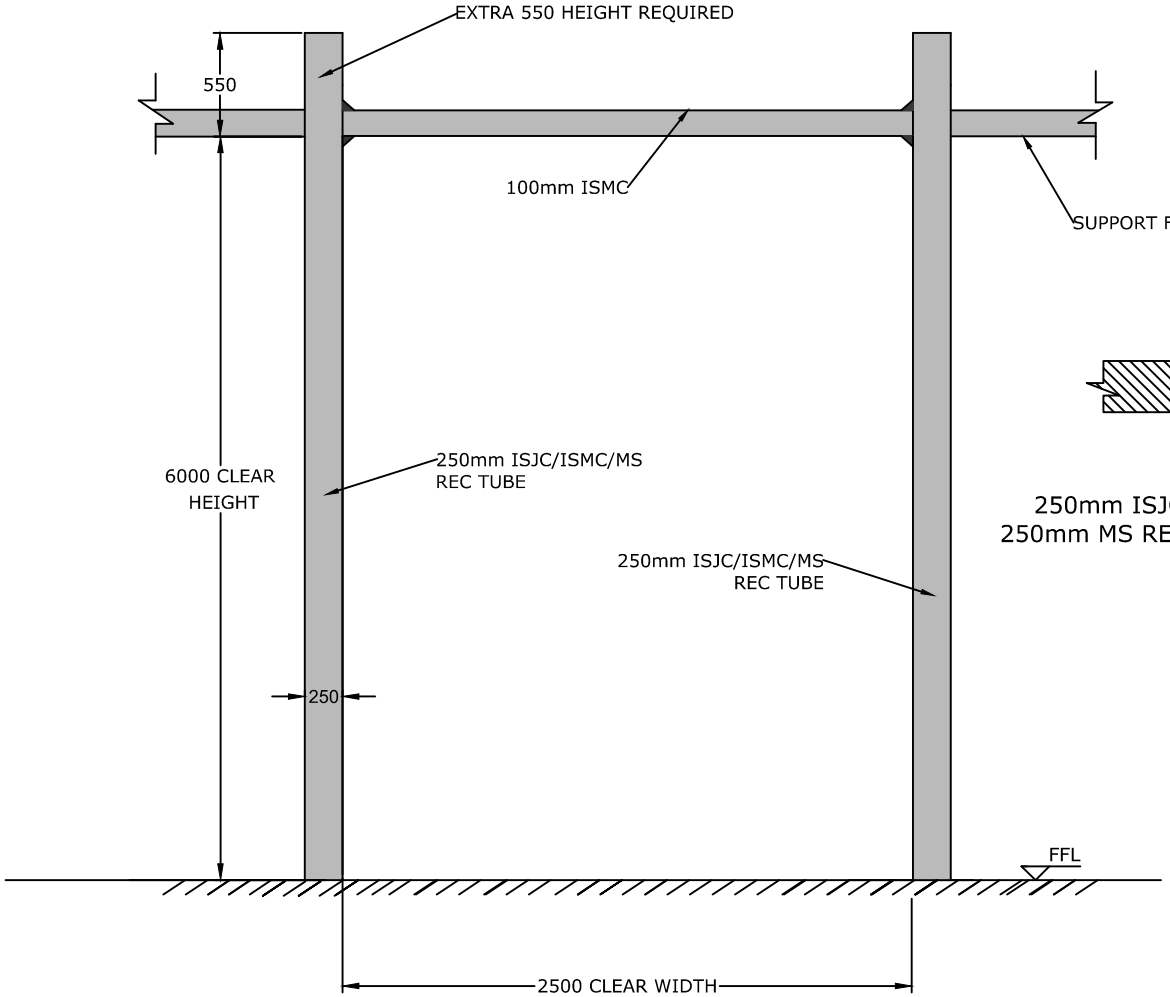


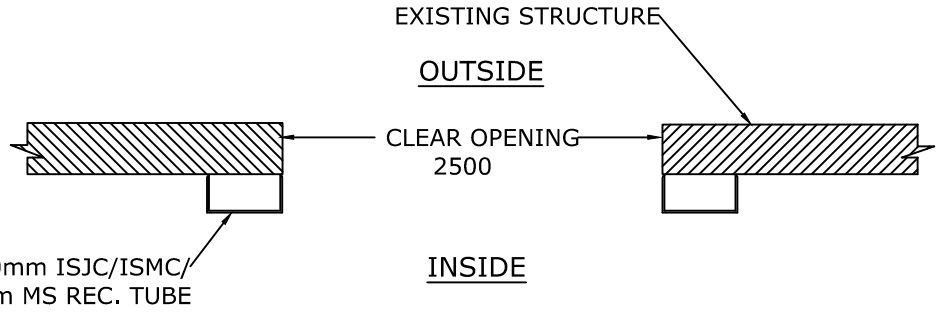

PLAN

CLEAR WIDTH (CW)	CLEAR HEIGHT (CH)	QUANTITY
2500	6000	4

This drawing & designing is the property of NIHVA TECHNOLOGIES. Not be sold or copy to any other concern.

TITLE

STRUCTURE FOR HIGH SPEED DOOR (RR 392)

CLIENT APPROVAL

ALL DIMENSION ARE IN mm

	SIGN	DATE
DRAWN	OMKAR	29/12/16
CHECK	SAGAR P.	29/12/16
ENG		
APPRD.		
MFG		
Ref. No.		

NIHVA TECHNOLOGIES PVT. LTD.

NIHVA TECHNOLOGY PVT. LTD. PUNE
Tel : 020 66304033
Email:- info@nihva.com
Website:- www.nihva.com

CLIENT - FERERRO INDIA PVT. LTD.

PROJECT-

SITE - BARAMATI

DWG. NO. - NIHVA/16-17/0056/R01

SCALE: NTS | WT: | SHEET: 01

If any queries contact : projects@nihva.com

REVISION 1- STRUCTURE SPECIFICATION ARE REVISED WITH STANDARD AVAILABLE MS CHANNEL/ MS TUBE.