


UPDATED DRAWING FOR MOIFICATION OF OVERLAP PPGI DOOR 1

CRM DOOR 1
QTY - 16 NOS

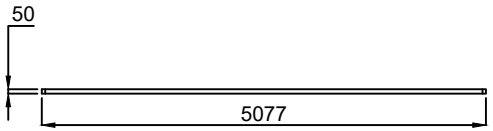

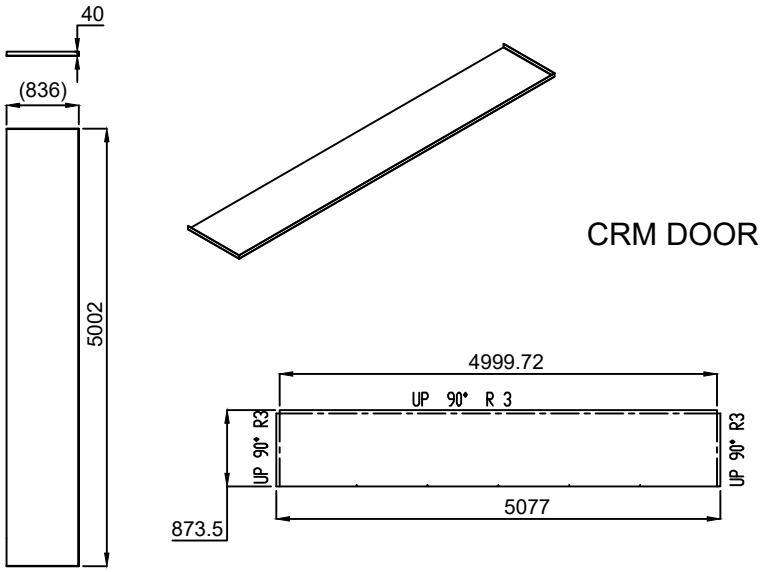

CRM DOOR 1

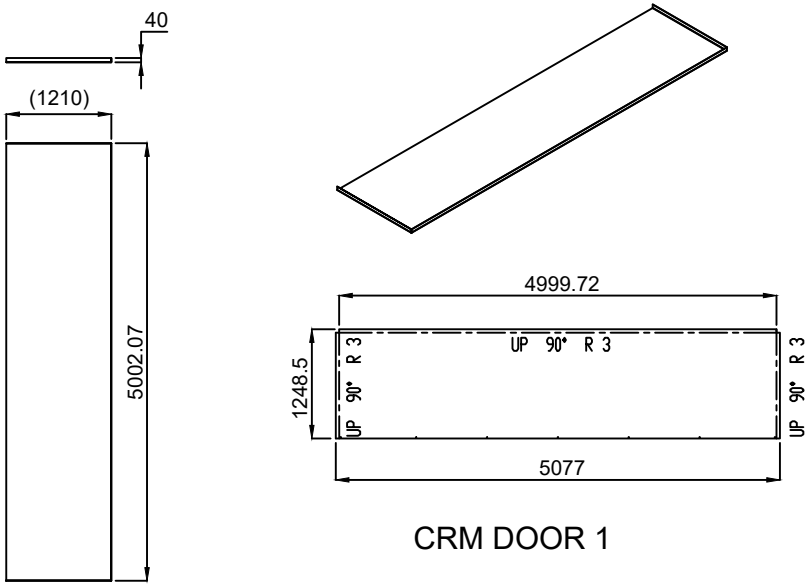

CRM DOOR 1

NOTE: DURING BENDING CRITICAL DIMENSION SHOULD BE MANDETORY

PPGI SHEET 0.8 MM

This drawing & design is the property of NIHVA TECHNOLOGIES. Not to be sold or copied to any other concern.

	Date	Revised By

TITLE:- 4 LEAF CRM DOOR 01

NIHVA TECHNOLOGIES PVT. LTD.

NIHVA TECHNOLOGIES PVT. LTD. PUNE
Tel : 020 66304033
Email:- info@nihva.com
Website:- www.nihva.com

	NAME	DATE	SIGN
DRAWN	M.SUTAR	14/05/2022	
CHECK	M.SUTAR	14/05/2022	
APPRD.			

CLIENT - NIHVA TECHNOLOGIES PVT.LTD
LOCATION -
PRODUCT - SLIDING DOOR

If any queries contact : design@nihva.com
DWG NO:-NIHVA/22-23/VDR/0015 REV- 0
ALL DIMENSION ARE IN mm
SCALE: NTS SCALE:-- 1:1 SHEET: 01 OF 01