
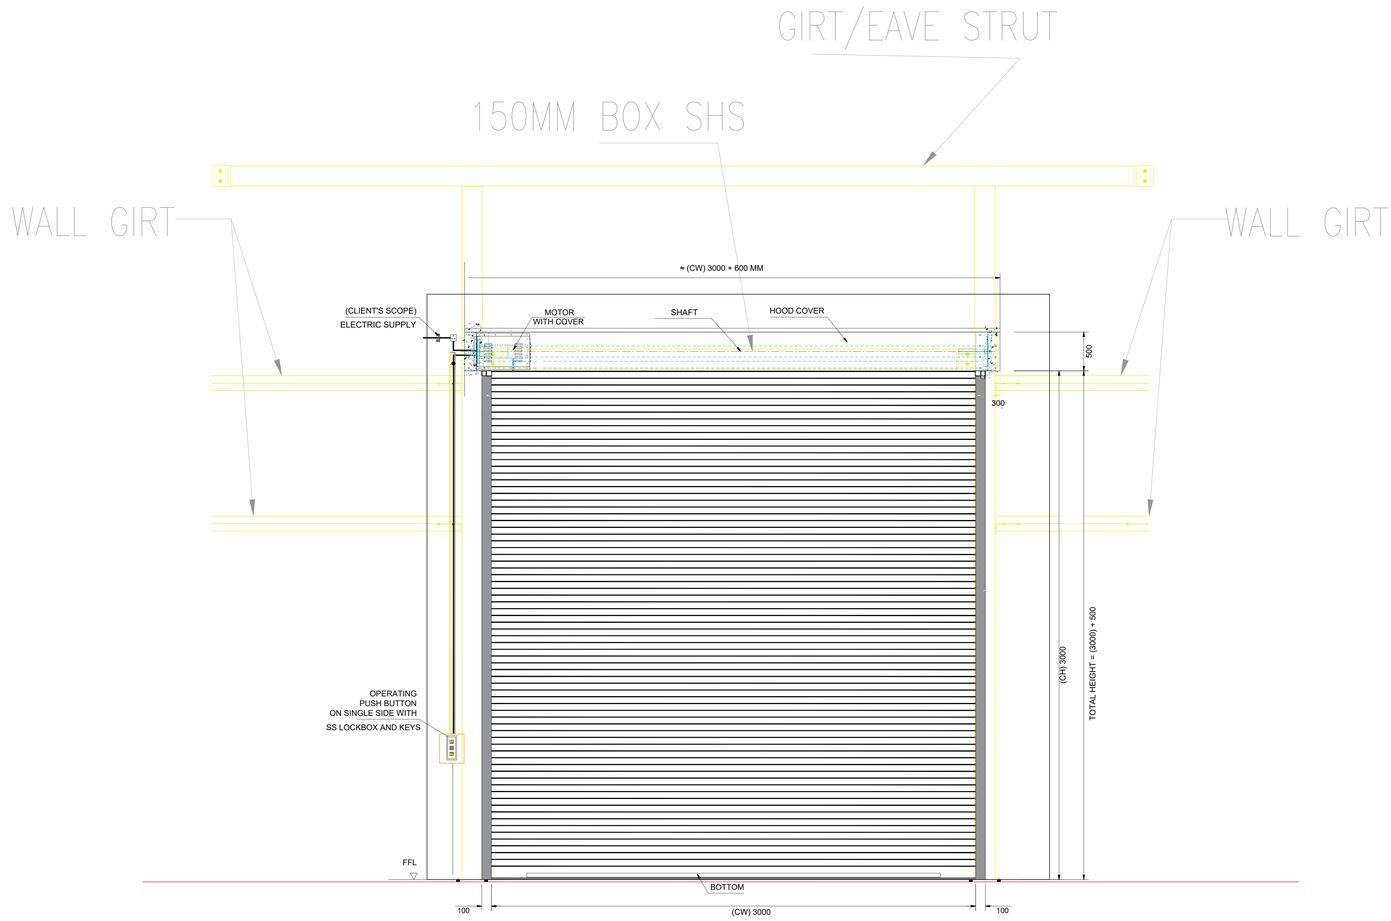
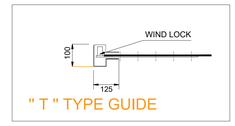



INSIDE ELEVATION

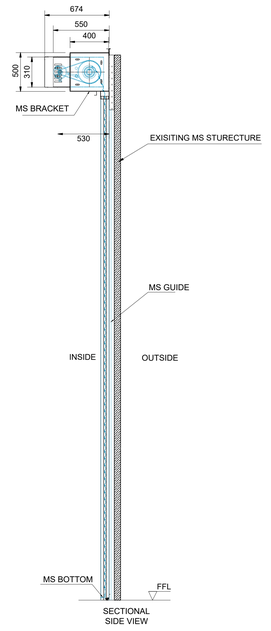


## TECHNICAL SPECIFICATION:-

| SR. | SPECIFICATION | DETAILS |
|---|---|---|
| 1. | Description & Drive | Motorized Rolling Shutter ( Direct Drive With CE Certificated ) |
| 2. | Location Area | Inside |
| 3. | Mounting Surface | MS STRACTURE |
| 4. | Slat | AS PER NIHVA STD. |
| 5. | Bottom Profile | MS Plate 100 x 2.5 mm thick with Angle Stiffner with rubber seal |
| 6. | Guide Profile | M.S." T " Shape profile 100 x 3 mm Thk. |
| 7. | Hood Cover & Motor Cover | Made of GI Sheet Thickness 0.9 mm |
| 8. | Surface finish | SYNTHETIC ENAMEL PAINT RAL SHADE 9002 |
| 9 | Accessories | Push Button Single side |

## SHUTTER SIZES :-

| SR. | CLEAR WIDTH | CLEAR HEIGHT | QTY. |
|---|---|---|---|
| 01 | 3000 mm | 3000 mm | 2 |

Note :-

1. All Dimension are in mm
2. This drawing is only for understanding purpose

This drawing & designing is the property of NIHVA TECHNOLOGIES. Not to be sold or copied to any other concern.

| | | | |
|---|---|---|---|
| TITLE :- MOTORISED ROLLING SHUTTER | | | NIHVA TECHNOLOGIES PVT. LTD. PUNE<br>Tel : 020 66304033<br>Email:- info@nihva.com<br>Website:- www.nihva.com |
| | NAME | DATE | CLIENT - SMP INFRASTRUCTURE PVT. LTD. |
| DRAWN | B.S. | 24/01/2025 | PROJECT - ROLLING SHUTTER |
| CHECK | V.M. | 24/01/2025 | FORMAT NO - NIHVA-DD-F-03 |
| APPROVAL | V.T. | 24/01/2025 | DWG. NO. : NIHVA/24-25/SMP/250124 REV-02 |
| | | | SCALE: NTS WT: SHEET: 01 OF 01 |
| ALL DIMENSION ARE IN mm | | | If any queries contact : design@nihva.com |