

BOM			
SL NO.	DESCRIPTION	SPECIFICATION	QTY
1	MS SQ. TUBE	100X100X4X3890L	2NOS
2	MS SQ. TUBE	100X100X4X1650L	2NOS
3	MS SQ. TUBE	32X32X2.6X1050L	29NOS
4	MS SQ. TUBE	32X32X2.6X300L	5NOS
5	MS SQ. TUBE	100X100X4X3690L	1NO
6	SUPPORT CHANNEL	ISMC 100X50X145L	2NOS
7	HING SUPPORT PLATE	175X175X10THK	2NOS
8	CLADDING1	649X350X1.5	2NOS
9	CLADDING2	633X350X1.5	4NOS
10	HING	4" MANUAL HING	2PAIRS
11	NYLON ROLLER	50X75	2NOS
12	MS PLATE	135X50X10THK	2NOS
13	ISMC	125X65X5.3X1650L	1NO

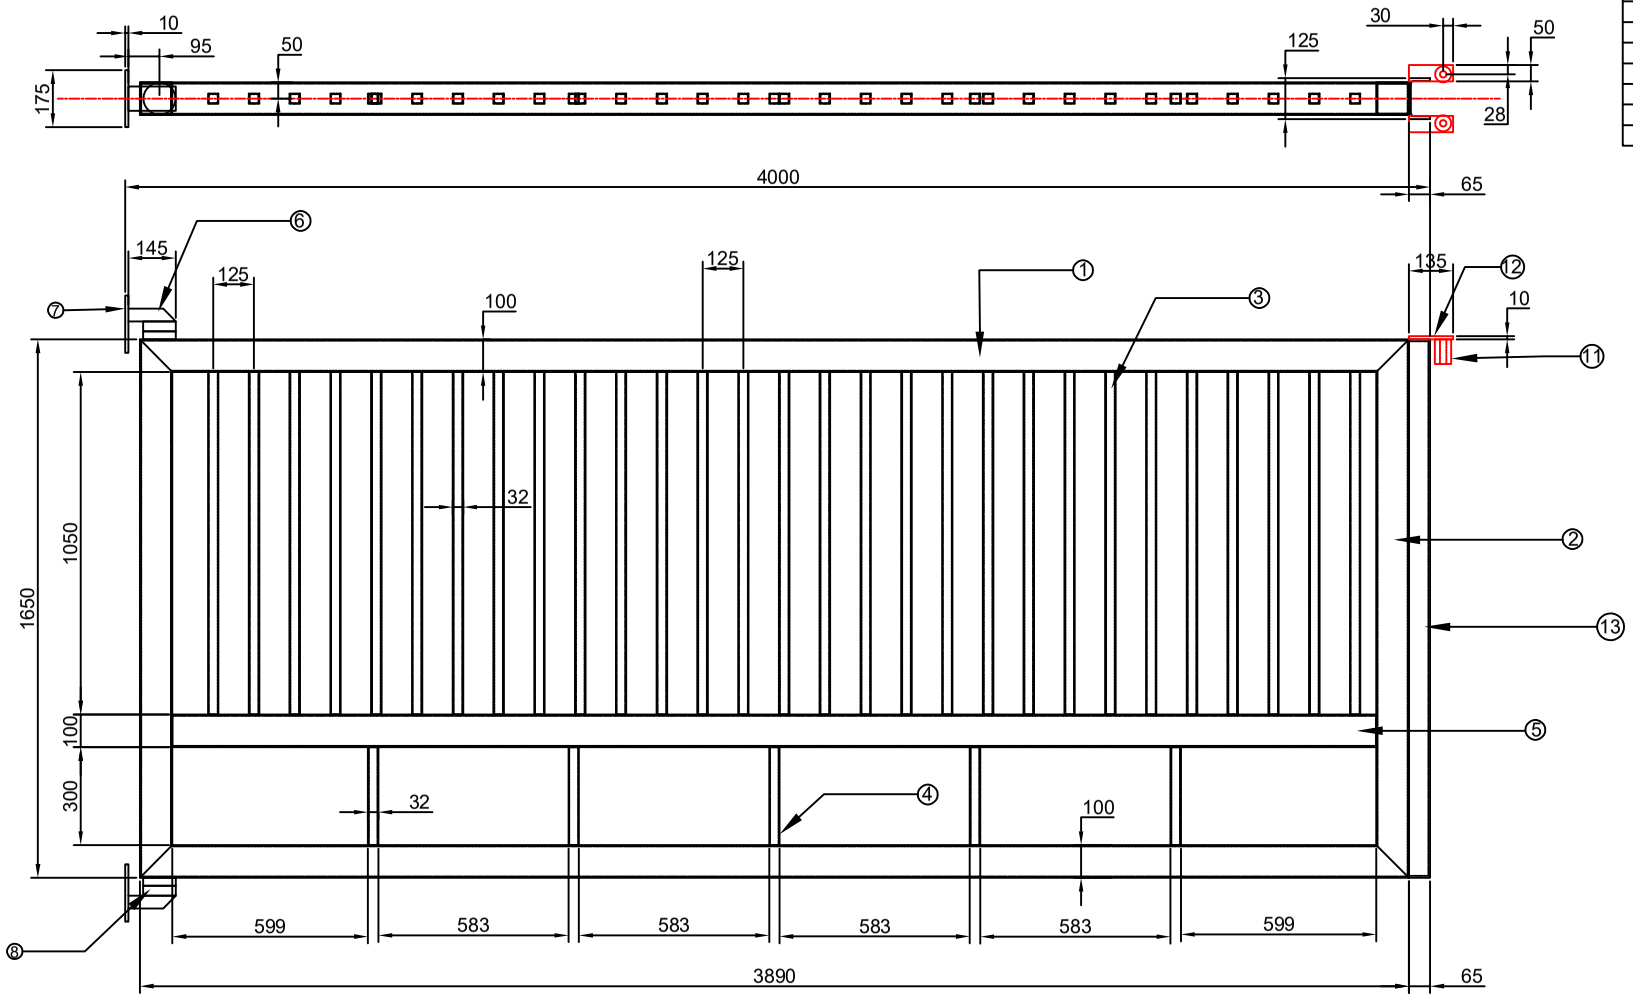

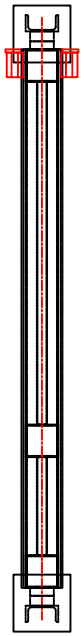

This drawing & design is the property of NIHVA TECHNOLOGIES. Not to be sold or copied to any other concern.

TITLE:- SWING GATE

NIHVA TECHNOLOGIES PVT. LTD.

NIHVA TECHNOLOGIES PVT. LTD. PUNE
Tel : 020 66304033
Email:- info@nihva.com
Website:- www.nihva.com

	NAME	DATE	SIGN
DRAWN	SUJATA	03/02/2022	
CHECK	G.PATIL	03/02/2022	
APPRD.	A.K	03/02/2022	

If any queries contact : design@nihva.com

ALL DIMENSION ARE IN mm

CLIENT -

LOCATION -

PRODUCT - SWING GATE | QTY- 01

DWG NO:-NIHVA/21-22/MFG/020 | REV- 0

SCALE: NTS | SCALE:-- 1:1 | SHEET: 01 OF 01

Rev No.	Revision	Date	Revised By