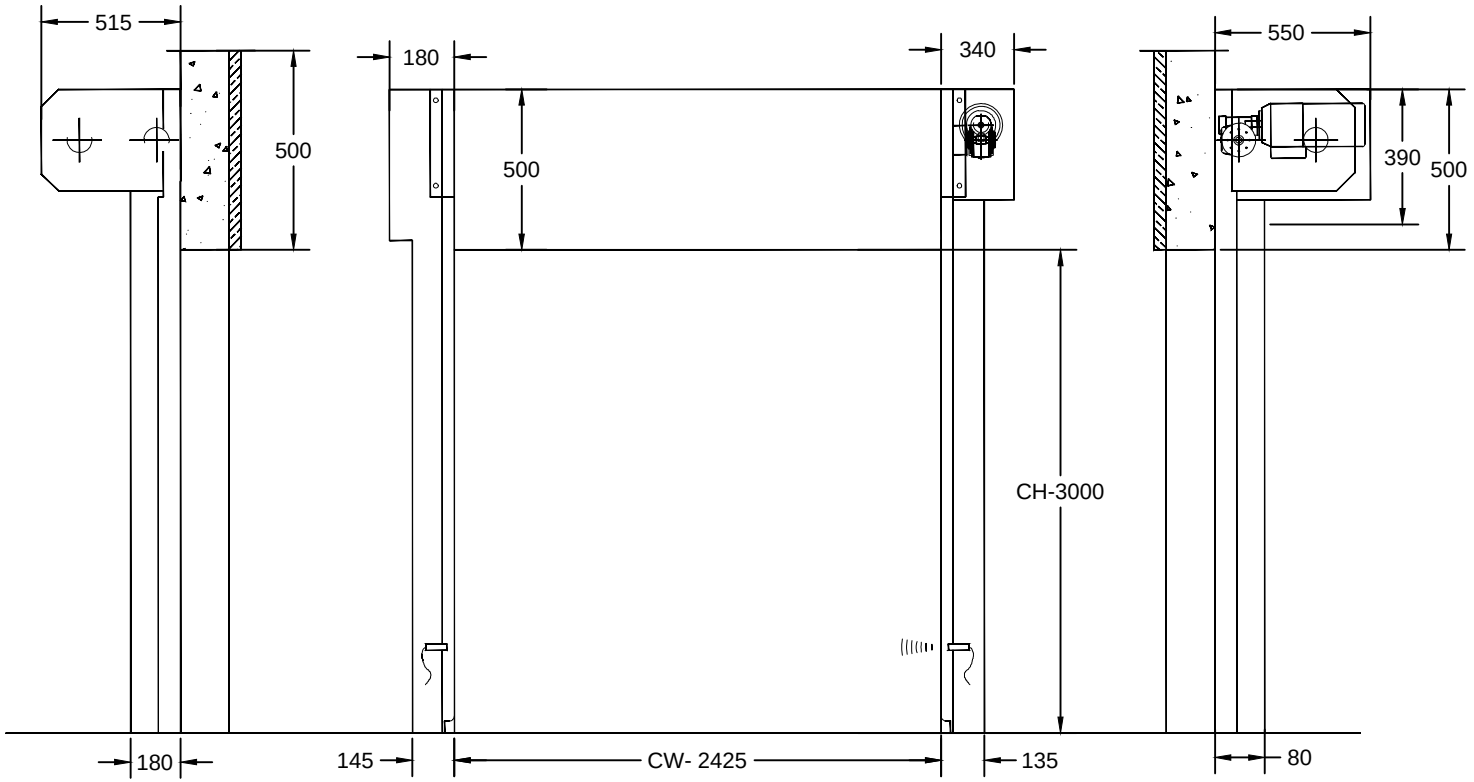

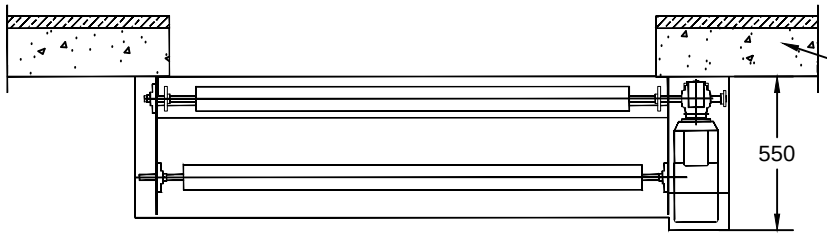

RCC / PEB STRUCTURE
FOR MOUNTING OF DOOR

This drawing & design is the property of NIHVA TECHNOLOGIES. Not to be sold or copied to any other concern.

TITLE: G.A. ALBANY HS9010PFR DRAWING

	SIGN	DATE
DRAWN	OMKAR	26/08/17
CHECK	SHEKHAR	26/08/17
REV.		
APPROVAL	SHEKHAR	26/08/17

If any queries contact : projects@nihva.com

ALL DIMENSION ARE IN mm

NIHVA
NIHVA TECHNOLOGIES PVT. LTD.
NIHVA TECHNOLOGIES PVT. LTD. PUNE
Tel : 020 66304033
Email:- info@nihva.com
Website:- www.nihva.com

CLIENT - HINDUSTAN UNILEVER LTD.

PROJECT -

SITE - MUMBAI

DWG. NO. : NIHVA/17-18/0184

SCALE: NTS | WT: | SHEET: 01 OF 01