

BASE FRAME DETAILS

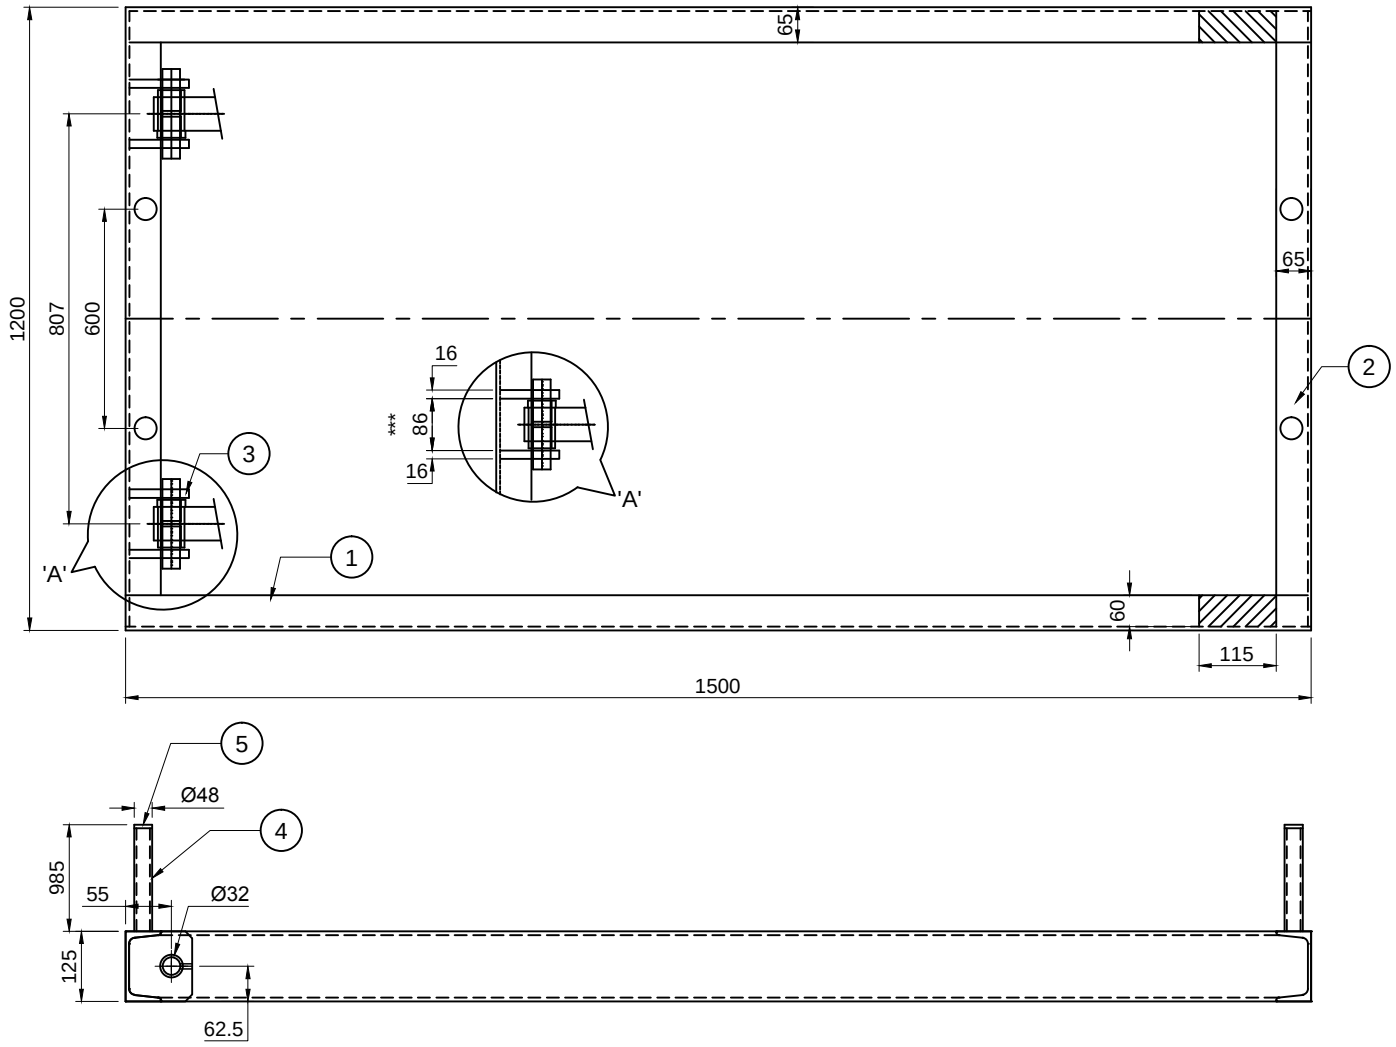

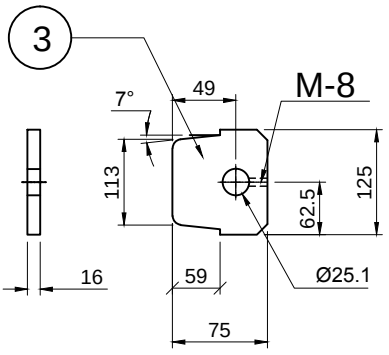

5.	PLATE OD48 X 5 THK	4NOS
4.	PIPE OD48 X 3 THK X 980L	4NOS
3.	FLAT 125 x 16Thk x 80L.M/C-75L	4NOS
2.	ISMC 125 x 65 x 1188L (NOTCH)	2NOS
1.	ISMC 125 x 65 x 1500L	2NOS
SR.NO	DESCRIPTION	QTY.

This drawing & design is the property of NIHVA TECHNOLOGIES. Not to be sold or copied to any other concern.

TITLE : - BASE FRAME ASSLY

NIHVA TECHNOLOGIES PVT. LTD.


NIHVA TECHNOLOGIES PVT. LTD. PUNE
Tel : 020 66304033
Email:- info@nihva.com
Website:- www.nihva.com


	SIGN	DATE	
DRAWN	P.A	04.10.2018	CLIENT -
CHECK	R.D	04.10.2018	PROJECT -
REV.			SITE -
APPROVAL			DWG. NO. : NIHVA/18-19/MFG/NSL/1018/001


If any queries contact : projects@nihva.com | SCALE: NTS | WT: | SHEET: 01 OF 01


ALL DIMENSION ARE IN mm

TOP FRAME DETAILS

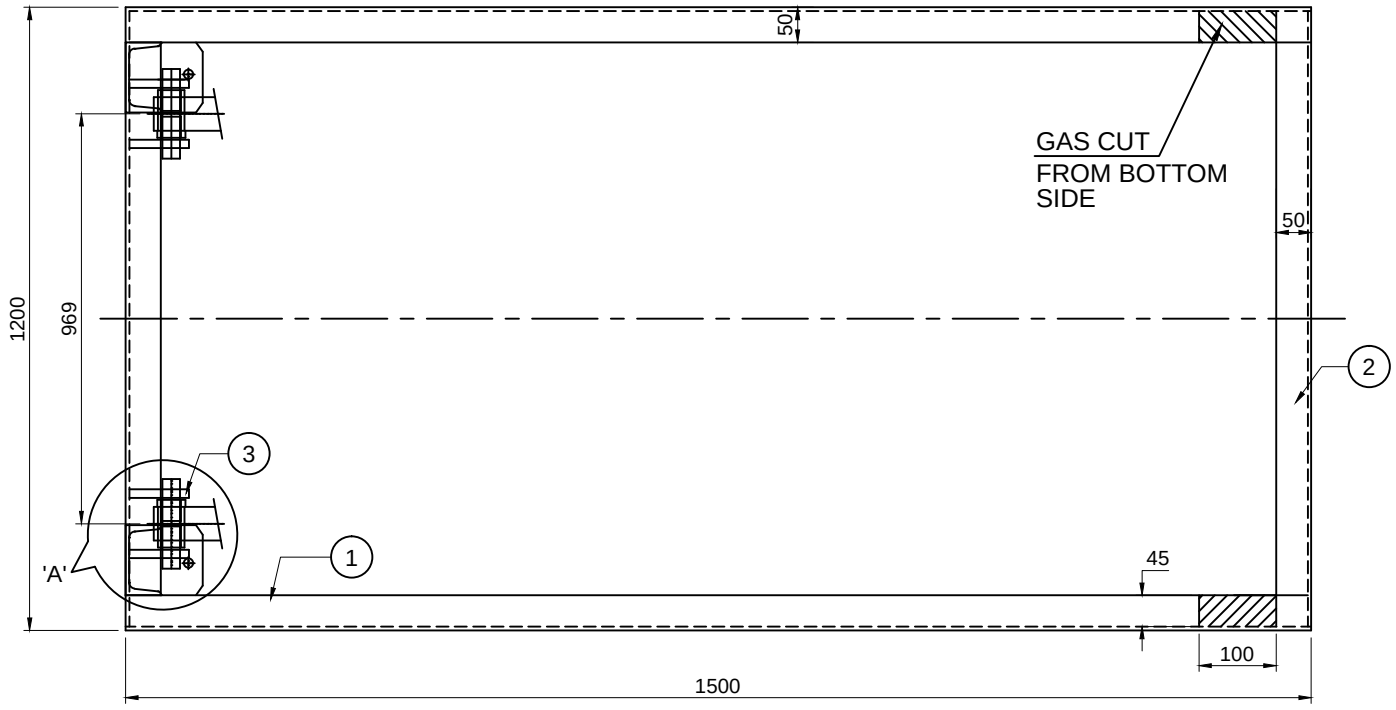

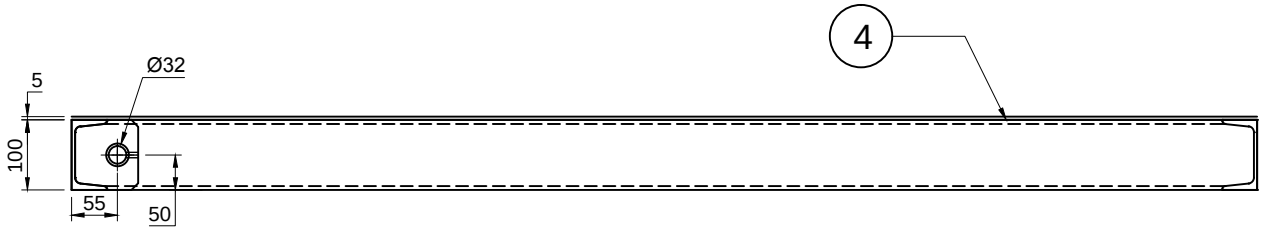

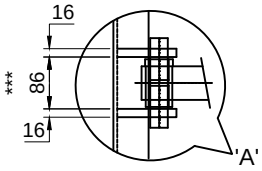

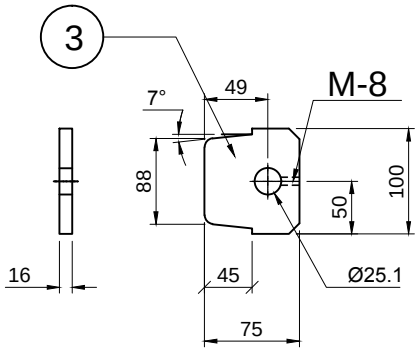

SR.NO	DESCRIPTION	QTY.
4.	CHEQ.SHEET 1200 X 3 THK X 1500L	1 NO
3.	PROFILE 100 X 16 X 75L	4NOS
2.	ISMC 100 x 50 x 1188L	2NOS
1.	ISMC 100 x 50 x 1500L	2NOS

This drawing & design is the property of NIHVA TECHNOLOGIES. Not to be sold or copied to any other concern.

TITLE : - TOP FRAME ASSLY

	SIGN	DATE
DRAWN	P.A	04.10.18
CHECK	R.D	04.10.18
REV.		
APPROVAL		

If any queries contact : projects@nihva.com

ALL DIMENSION ARE IN mm

NIHVA TECHNOLOGIES PVT. LTD.

NIHVA TECHNOLOGIES PVT. LTD. PUNE
Tel : 020 66304033
Email:- info@nihva.com
Website:- www.nihva.com

CLIENT -


PROJECT -

SITE -

DWG. NO. : NIHVA/18-19/MFG/NSL/1018/002

SCALE: NTS | WT: | SHEET: 01 OF 01

TOP FRAME STIFFENING DETAILS

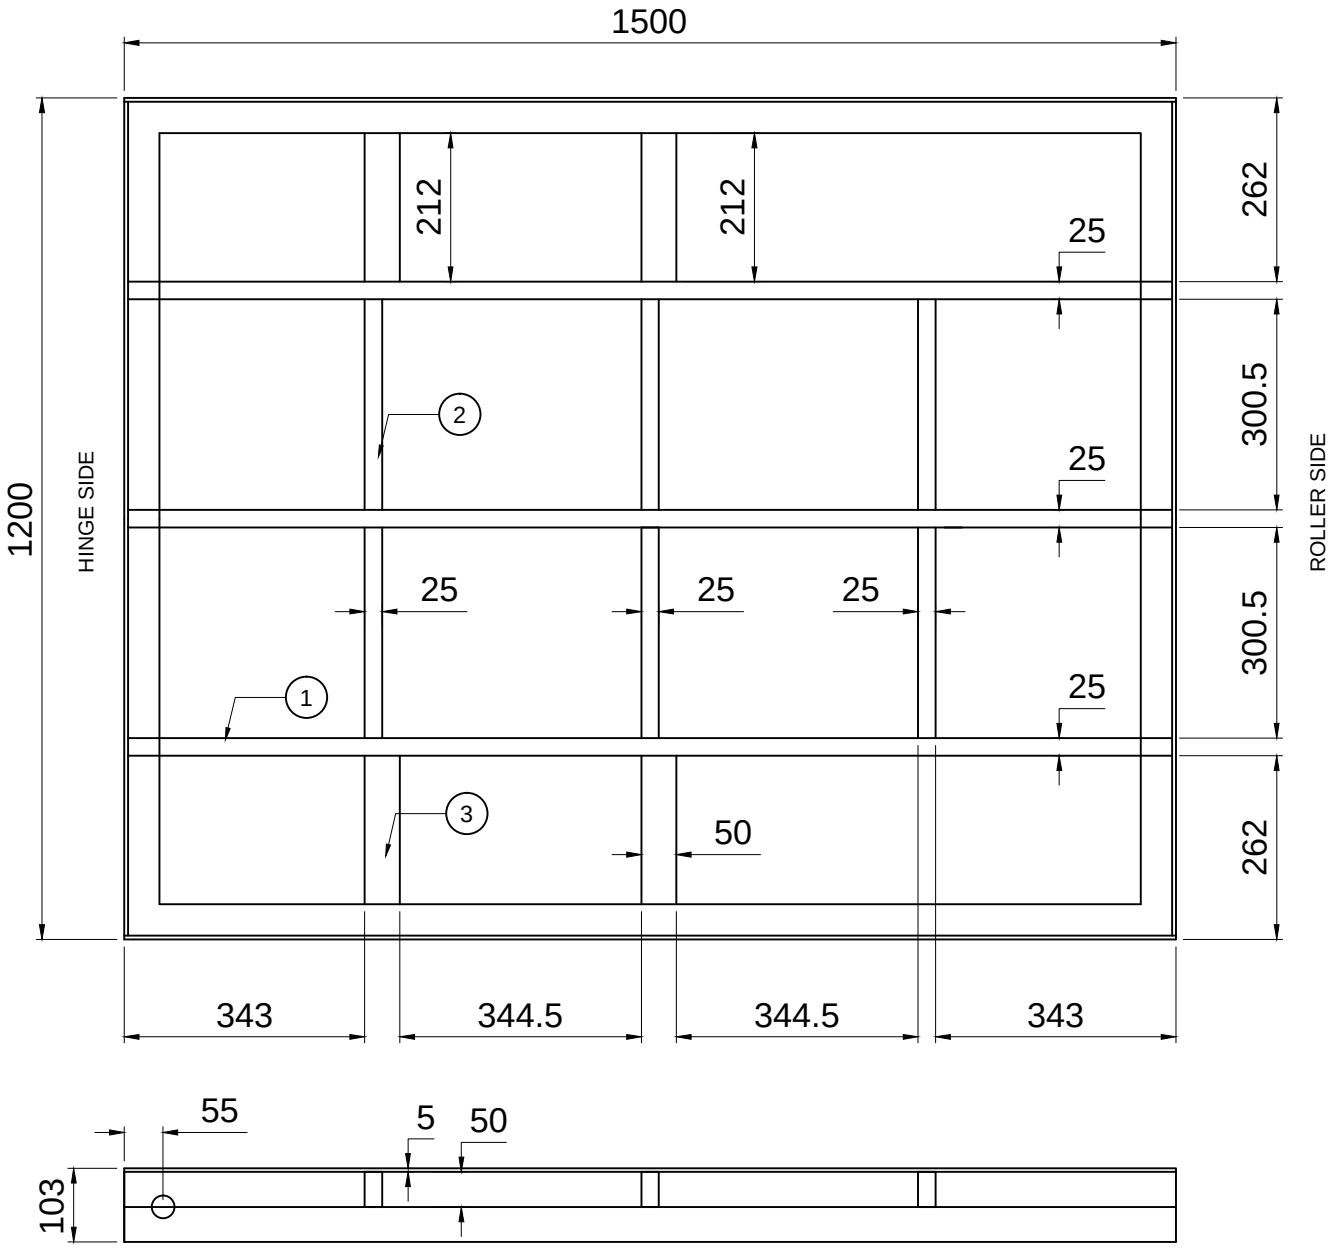

3.	FLAT 50 X 5 X 212L	4NOS
2.	R.TUBE 50 X 25 X 3 THK X 300L	6NOS
1.	R.TUBE 50 X 25 X 3 THK X 1488L	3NOS
SR.NO	DESCRIPTION	QTY.

This drawing & design is the property of NIHVA TECHNOLOGIES. Not to be sold or copied to any other concern.

TITLE : -
TOP FRAME STIFFENINIG

NIHVA
NIHVA TECHNOLOGIES PVT. LTD.

NIHVA TECHNOLOGIES PVT. LTD. PUNE
Tel : 020 66304033
Email:- info@nihva.com
Website:- www.nihva.com


	SIGN	DATE
DRAWN	P.A	04.10.18
CHECK	R.D	04.10.18
REV.		
APPROVAL		


If any queries contact : projects@nihva.com


ALL DIMENSION ARE IN mm


CLIENT -
PROJECT -
SITE -
DWG. NO. : NIHVA/18-19/MFG/NSL/1018/003
SCALE: NTS | WT: | SHEET: 01 OF 01

RAILING & DOOR ASSLY

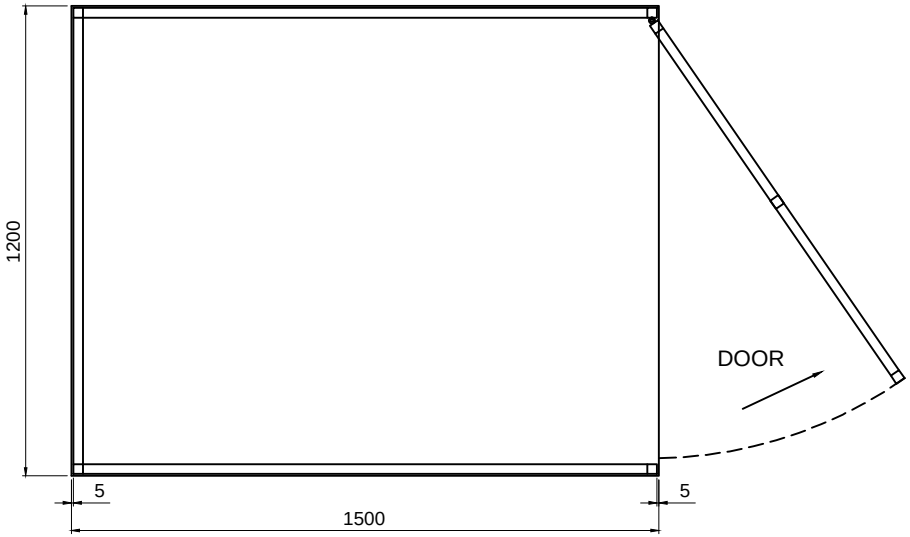

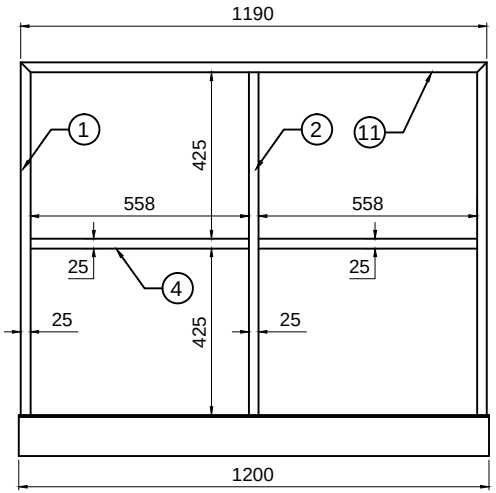

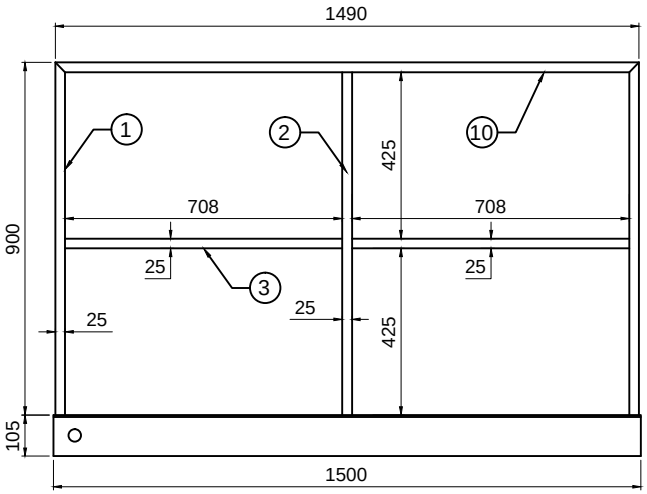

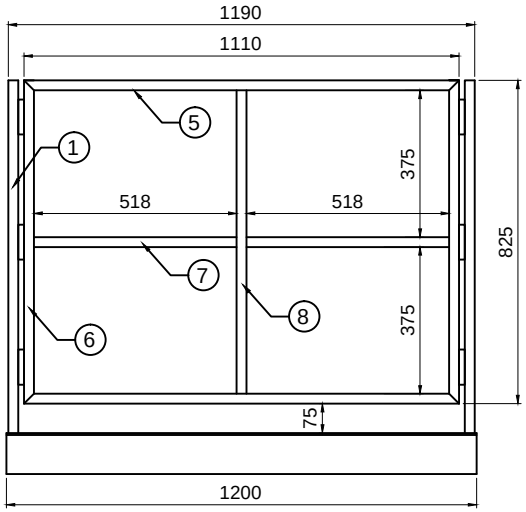

SR.NO	DESCRIPTION	QTY.	SR.NO	DESCRIPTION	QTY.
1.	SQ.TUBE 25 X 25 X 2.5 THK X 900L	4 NOS	10.	SQ.TUBE 25 X 25 X 2.5 THK X 1490L	2 NOS
2.	SQ.TUBE 25 X 25 X 2.5 THK X 875L	3 NOS	11.	SQ.TUBE 25 X 25 X 2.5 THK X 1190L	1 NO
3.	SQ.TUBE 25 X 25 X 2.5 THK X 708L	4NOS			
4.	SQ.TUBE 25 X 25 X 2.5 THK X 558L	2NOS			
5.	SQ.TUBE 25 X 25 X 2.5 THK X 1110L	1 NO			
6.	SQ.TUBE 25 X 25 X 2.5 THK X 825L	2NOS			
7.	SQ.TUBE 25 X 25 X 2.5 THK X 518L	2NOS			
8.	SQ.TUBE 25 X 25 X 2.5 THK X 775L	1 NO			
9.	HEAVY DUTY HINGES	6NOS			

This drawing & design is the property of NIHVA TECHNOLOGIES. Not to be sold or copied to any other concern.

TITLE : -
SAFETY RAILING ASSLY

NIHVA TECHNOLOGIES PVT. LTD.

NIHVA TECHNOLOGIES PVT. LTD. PUNE
Tel : 020 66304033
Email:- info@nihva.com
Website:- www.nihva.com

	SIGN	DATE
DRAWN	P.A	04.10.18
CHECK	R.D	04.10.18
REV.		
APPROVAL		


If any queries contact : projects@nihva.com

ALL DIMENSION ARE IN mm

CLIENT -
PROJECT -
SITE -
DWG. NO. : NIHVA/18-19/MFG/NSL/1018/004
SCALE: NTS | WT: | SHEET: 01 OF 01

BOTTOM ARM PAIR NO : 01

PIVOT BUSH

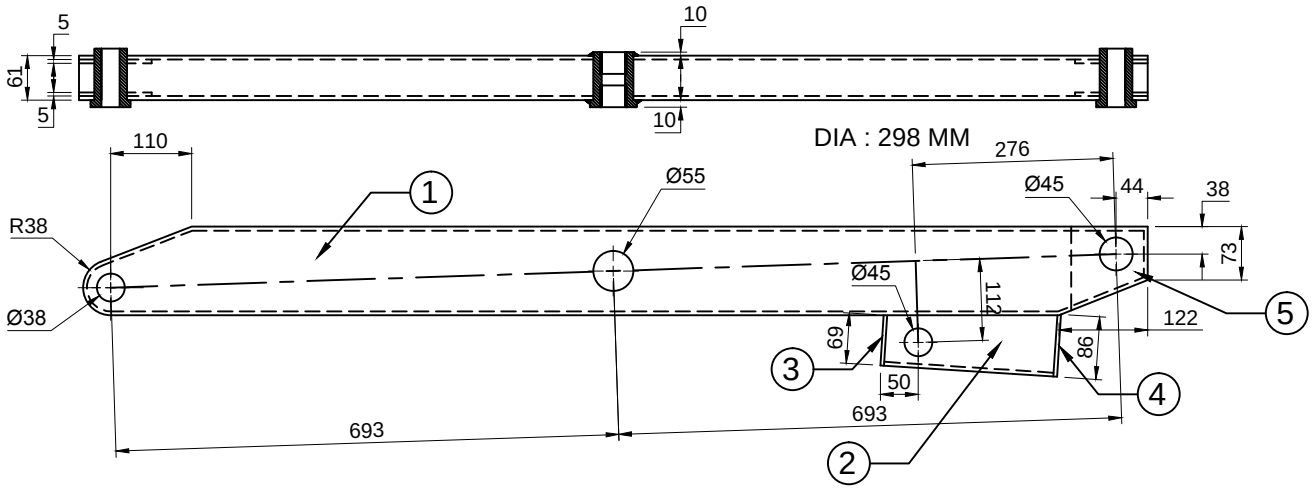


INNER ARM


1. R.TUBE 122 X 61 X 5.4 THK X 1470L = 2 NOS(LH / RH)
2. R.TUBE 122 X 61 X 5.4 THK X 235L = 2 NOS(5 MM CLOSING BOTH SIDE)
3. FLAT 61 X 5 X 69L = 2 NOS
4. FLAT 61 X 5 X 85L = 2 NOS
5. FLAT 100 X 5 X 100L = 4 NOS

USE OD 33 PIPE AT RADIUS

GAS CUT

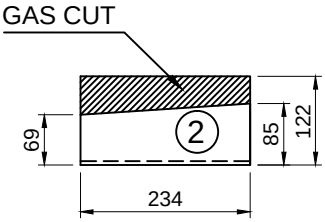

BOTTOM ROLLER PIN

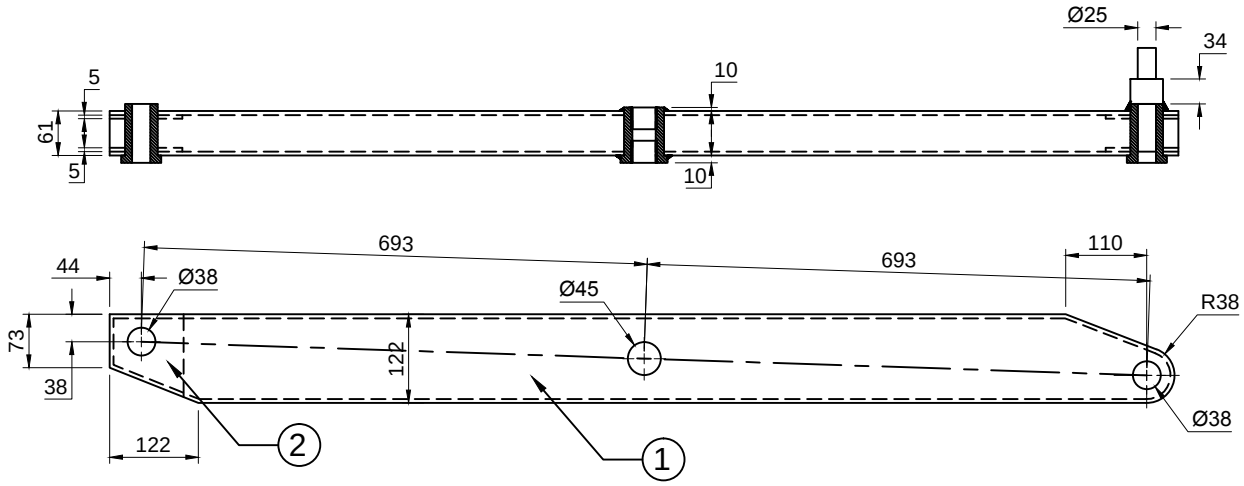

OUTER ARM


1. R.TUBE 122 X 61 X 5.4 THK X 1470L = 2 NOS(LH / RH)
2. FLAT 100 X 5 X 100L = 4 NOS

USE OD 33 PIPE AT RADIUS


This drawing & design is the property of NIHVA TECHNOLOGIES. Not to be sold or copied to any other concern.

TITLE : - BOTTOM SCISSOR PAIR 01			NIHVA TECHNOLOGIES PVT. LTD. PUNE Tel : 020 66304033 Email:- info@nihva.com Website:- www.nihva.com
	SIGN	DATE	
DRAWN	P.A	04.10.18	CLIENT -
CHECK	R.D	04.10.18	PROJECT -
REV.			SITE -
APPROVAL			DWG. NO. : NIHVA/18-19/MFG/NSL/1018/005
If any queries contact : projects@nihva.com			SCALE: NTS / WT: / SHEET: 01 OF 01
ALL DIMENSION ARE IN mm			

BOTTOM ARM PAIR NO : 02

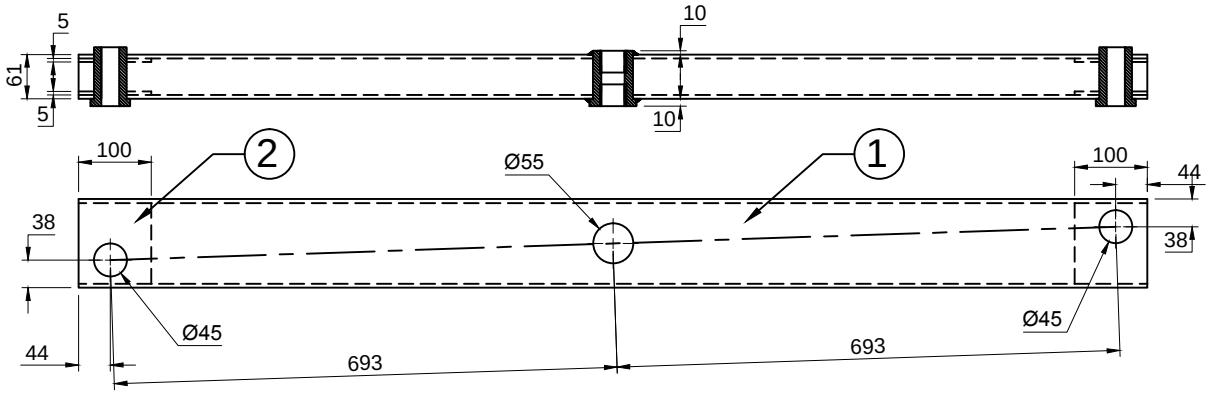

1. INNER ARM R.TUBE 122 X 61 X 5.4 THK X 1475L = 2 NOS(LH / RH)
2. INSIDE FLAT 100 X 5 X 100L = 8 NOS

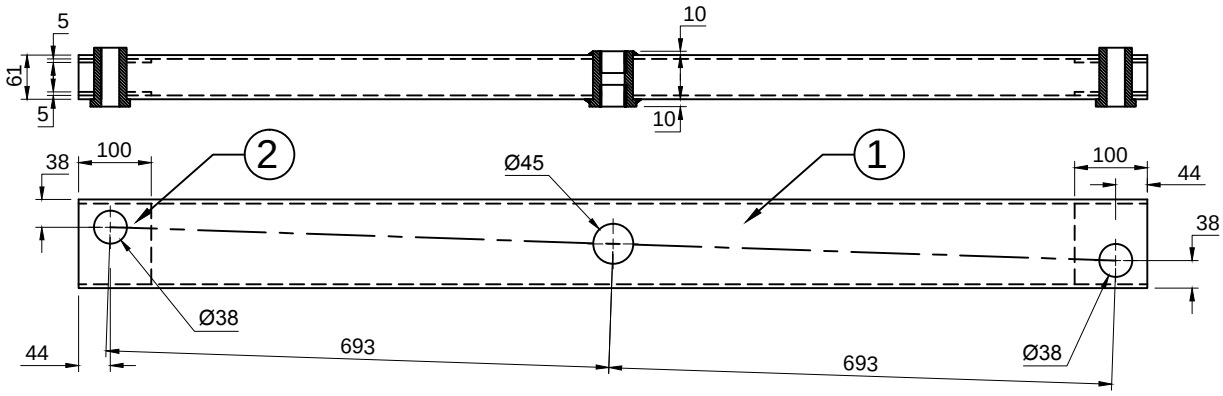


1. OUTER ARM R.TUBE 122 X 61 X 5.4 THK X 1475L = 2 NOS(LH / RH)
2. INSIDE FLAT 100 X 5 X 100L = 8 NOS


This drawing & design is the property of NIHVA TECHNOLOGIES. Not to be sold or copied to any other concern.

TITLE : - BOTTOM SCISSOR PAIR 02			NIHVA TECHNOLOGIES PVT. LTD. PUNE Tel : 020 66304033 Email:- info@nihva.com Website:- www.nihva.com
	SIGN	DATE	
DRAWN	P.A	04.10.2018	CLIENT -
CHECK	R.D	04.10.2018	PROJECT -
REV.			SITE -
APPROVAL			DWG. NO. : NIHVA/18-19/MFG/NSL/1018/006
If any queries contact : projects@nihva.com			SCALE: NTS / WT: / SHEET: 01 OF 01
ALL DIMENSION ARE IN mm			

BOTTOM ARM PAIR NO : 03

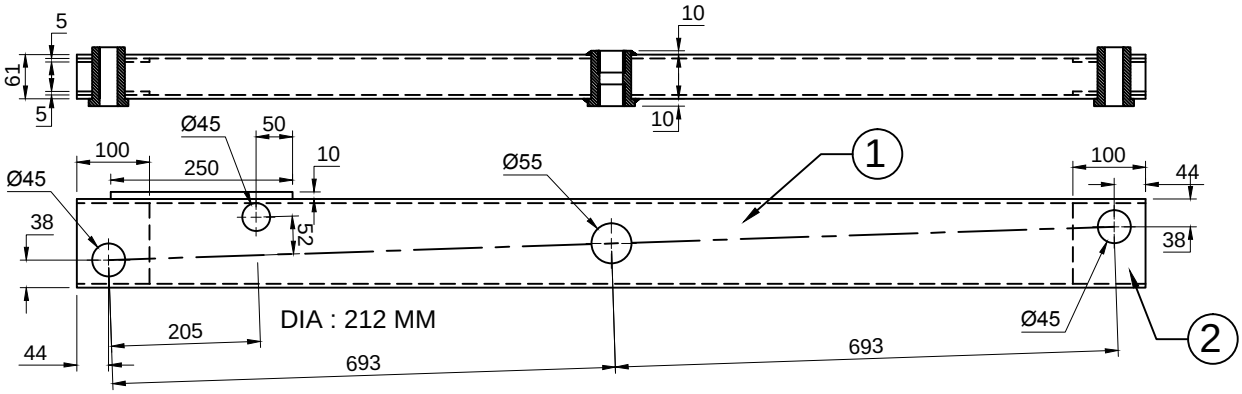

1. INNER ARM R.TUBE 122 X 61 X 5.4 THK X 1475L = 2 NOS(LH / RH)
2. INSIDE FLAT 100 X 5 X 100L = 8 NOS
3. FLAT 50 X 10 X 250L = 2 NOS

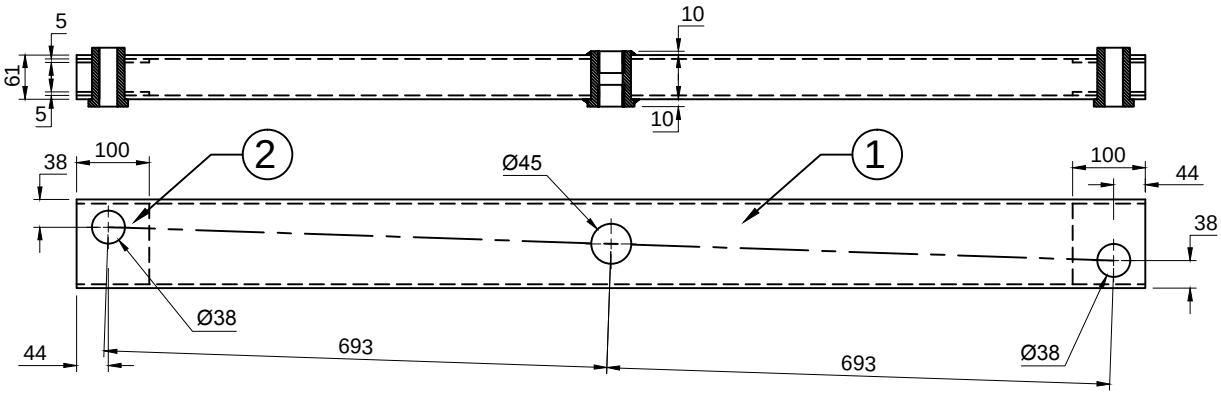



1. OUTER ARM R.TUBE 122 X 61 X 5.4 THK X 1475L = 2 NOS(LH / RH)
2. INSIDE FLAT 100 X 5 X 100L = 8 NOS

This drawing & design is the property of NIHVA TECHNOLOGIES. Not to be sold or copied to any other concern.


TITLE : - BOTTOM SCISSOR PAIR 03			NIHVA TECHNOLOGIES PVT. LTD. PUNE Tel : 020 66304033 Email:- info@nihva.com Website:- www.nihva.com
	SIGN	DATE	
DRAWN	P.A	04.10.2018	CLIENT -
CHECK	R.D	04.10.2018	PROJECT -
REV.			SITE -
APPROVAL			DWG. NO. : NIHVA/18-19/MFG/NSL/1018/007
If any queries contact : projects@nihva.com			SCALE: NTS / WT: / SHEET: 01 OF 01
ALL DIMENSION ARE IN mm			

BOTTOM ARM PAIR NO : 04

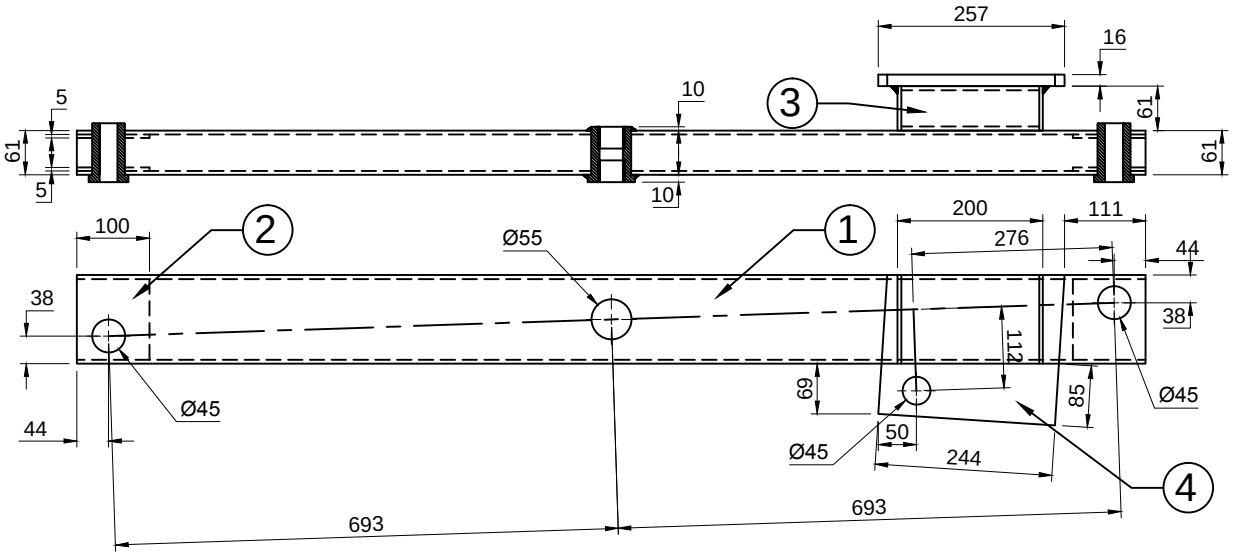

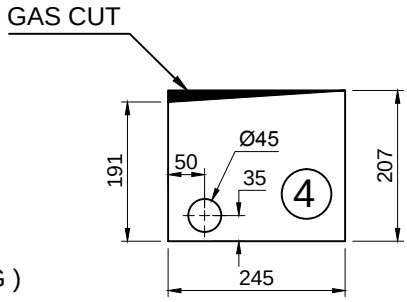

1. INNER ARM R.TUBE 122 X 61 X 5.4 THK X 1475L = 2 NOS (LH / RH)
2. INSIDE FLAT 100 X 5 X 100L = 8 NOS
3. R.TUBE 122 x 61 x 5.4 THK X 190L = 2 NOS (BOTH SIDE 5 MM CLOSING)
4. PROFILE PLATE 245 X 16 THK X 207L = 2 NOS

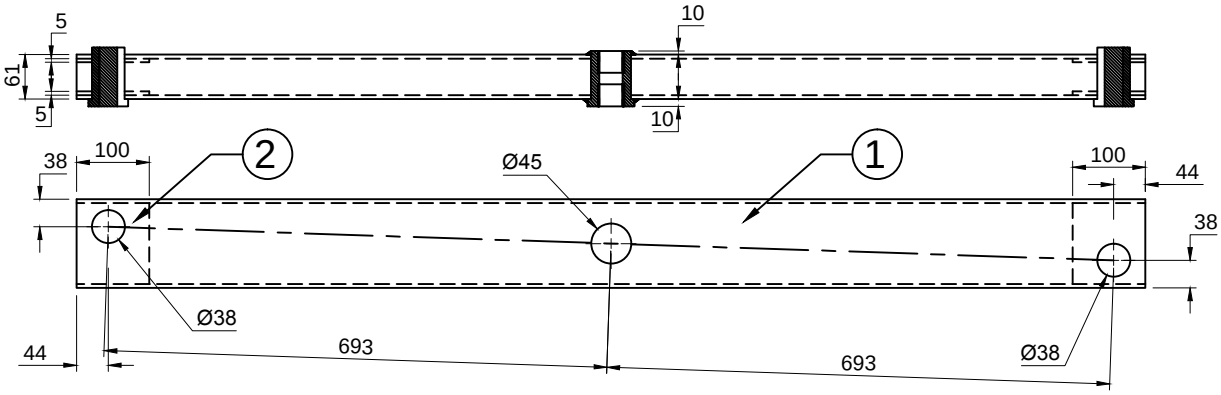


1. OUTER ARM R.TUBE 122 X 61 X 5.4 THK X 1475L = 2 NOS(LH / RH)
2. INSIDE FLAT 100 X 5 X 100L = 8 NOS


This drawing & design is the property of NIHVA TECHNOLOGIES. Not to be sold or copied to any other concern.

TITLE : - BOTTOM SCISSOR PAIR 04			NIHVA TECHNOLOGIES PVT. LTD. PUNE Tel : 020 66304033 Email:- info@nihva.com Website:- www.nihva.com
	SIGN	DATE	
DRAWN	P.A	04.10.2018	CLIENT -
CHECK	R.D	04.10.2018	PROJECT -
REV.			SITE -
APPROVAL			DWG. NO. : NIHVA/18-19/MFG/NSL/1018/008
If any queries contact : projects@nihva.com			SCALE: NTS / WT: / SHEET: 01 OF 01
ALL DIMENSION ARE IN mm			

BOTTOM ARM PAIR NO : 05

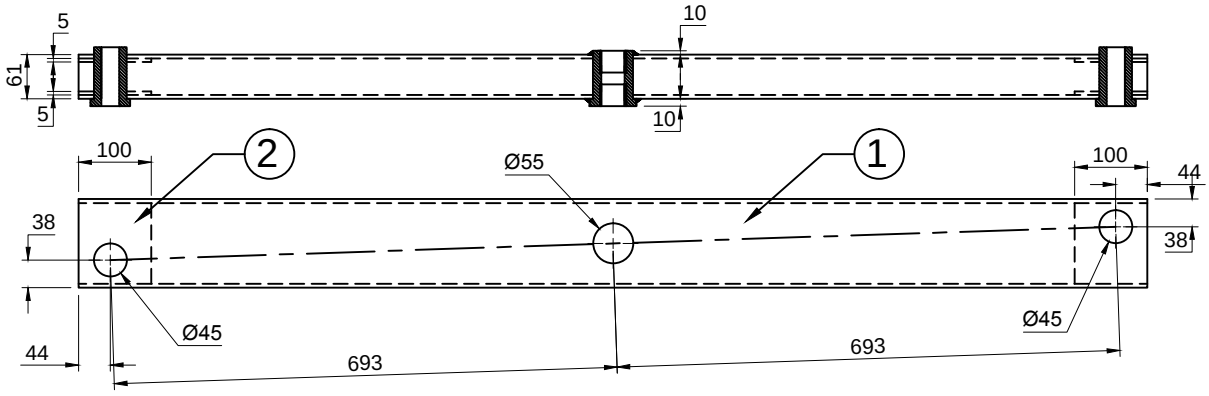

1. INNER ARM R.TUBE 122 X 61 X 5.4 THK X 1475L = 2 NOS(LH / RH)
2. INSIDE FLAT 100 X 5 X 100L = 8 NOS

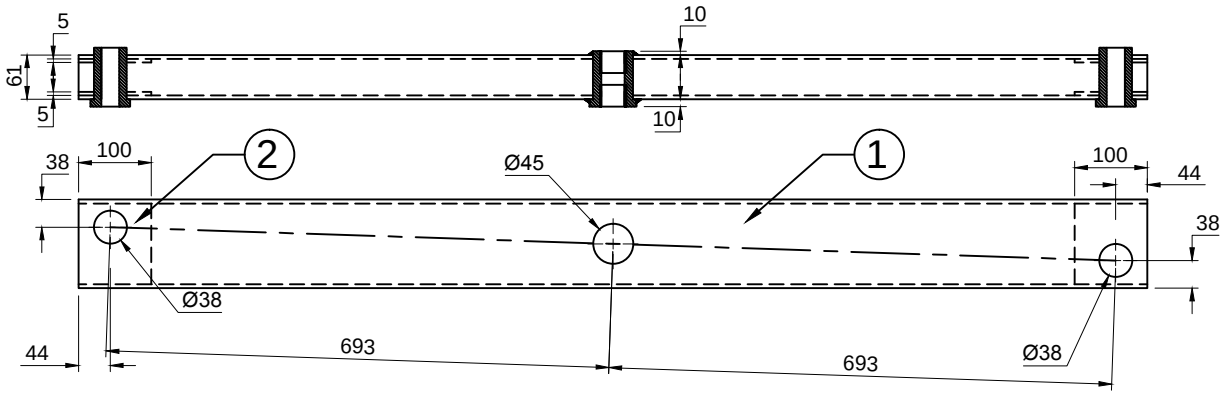


1. OUTER ARM R.TUBE 122 X 61 X 5.4 THK X 1475L = 2 NOS(LH / RH)
2. INSIDE FLAT 100 X 5 X 100L = 8 NOS


This drawing & design is the property of NIHVA TECHNOLOGIES. Not to be sold or copied to any other concern.

TITLE : - BOTTOM SCISSOR PAIR 05			NIHVA TECHNOLOGIES PVT. LTD. PUNE Tel : 020 66304033 Email:- info@nihva.com Website:- www.nihva.com
	SIGN	DATE	
DRAWN	P.A	04.10.2018	CLIENT -
CHECK	R.D	04.10.2018	PROJECT -
REV.			SITE -
APPROVAL			DWG. NO. : NIHVA/18-19/MFG/NSL/1018/009
If any queries contact : projects@nihva.com			SCALE: NTS / WT: / SHEET: 01 OF 01
ALL DIMENSION ARE IN mm			

BOTTOM ARM PAIR NO : 06

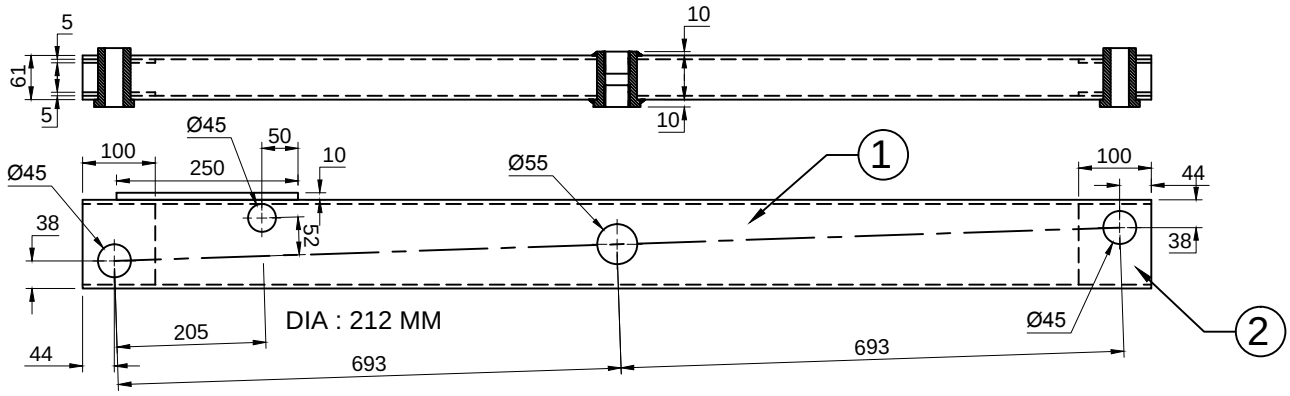

1. INNER ARM R.TUBE 122 X 61 X 5.4 THK X 1475L = 2 NOS(LH / RH)
2. INSIDE FLAT 100 X 5 X 100L = 8 NOS
3. FLAT 50 X 10 X 250L = 2 NOS

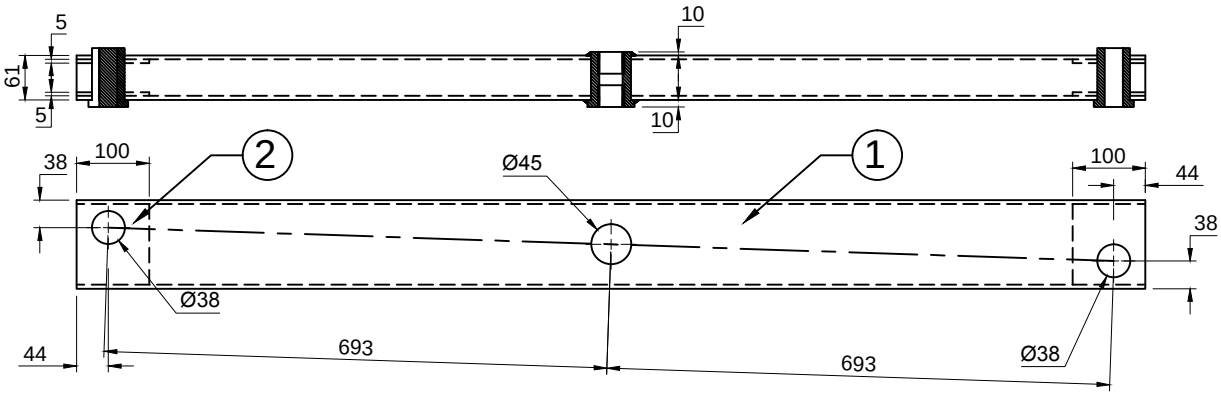


1. OUTER ARM R.TUBE 122 X 61 X 5.4 THK X 1475L = 2 NOS(LH / RH)
2. INSIDE FLAT 100 X 5 X 100L = 8 NOS


This drawing & design is the property of NIHVA TECHNOLOGIES. Not to be sold or copied to any other concern.

TITLE : - BOTTOM SCISSOR PAIR 06			NIHVA TECHNOLOGIES PVT. LTD. PUNE Tel : 020 66304033 Email:- info@nihva.com Website:- www.nihva.com
	SIGN	DATE	
DRAWN	P.A	04.10.2018	CLIENT -
CHECK	R.D	04.10.2018	PROJECT -
REV.			SITE -
APPROVAL			DWG. NO. : NIHVA/18-19/MFG/NSL/1018/010
If any queries contact : projects@nihva.com			SCALE: NTS / WT: / SHEET: 01 OF 01
ALL DIMENSION ARE IN mm			

BOTTOM ARM PAIR NO : 07

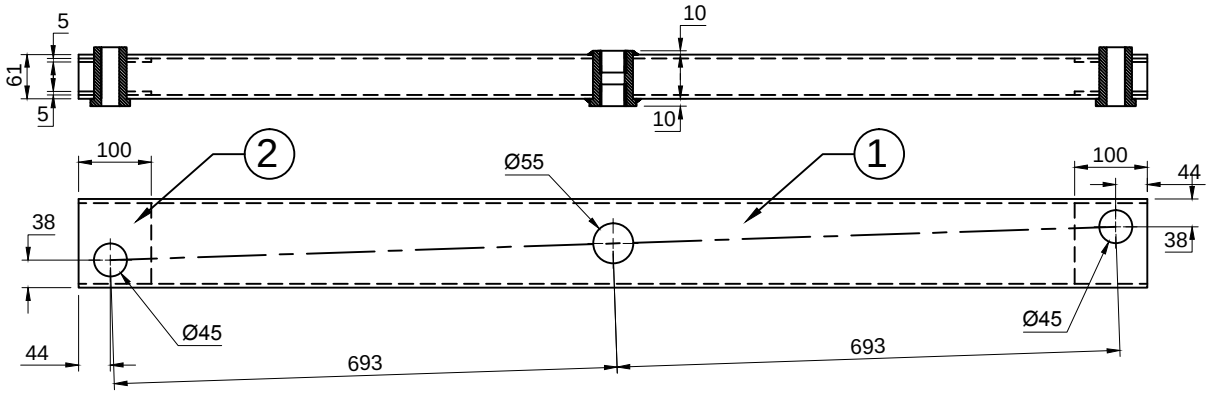

1. INNER ARM R.TUBE 122 X 61 X 5.4 THK X 1475L = 2 NOS(LH / RH)
2. INSIDE FLAT 100 X 5 X 100L = 8 NOS

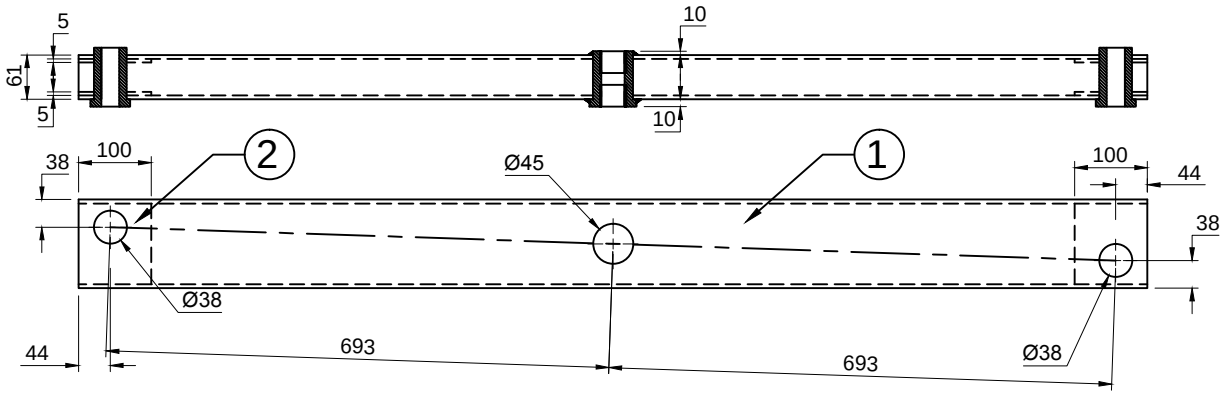


1. OUTER ARM R.TUBE 122 X 61 X 5.4 THK X 1475L = 2 NOS(LH / RH)
2. INSIDE FLAT 100 X 5 X 100L = 8 NOS

This drawing & design is the property of NIHVA TECHNOLOGIES. Not to be sold or copied to any other concern.

TITLE : - BOTTOM SCISSOR PAIR 07			NIHVA TECHNOLOGIES PVT. LTD. PUNE Tel : 020 66304033 Email:- info@nihva.com Website:- www.nihva.com
	SIGN	DATE	
DRAWN	P.A	04.10.2018	CLIENT -
CHECK	R.D	04.10.2018	PROJECT -
REV.			SITE -
APPROVAL			DWG. NO. : NIHVA/18-19/MFG/NSL/1018/011
If any queries contact : projects@nihva.com			SCALE: NTS / WT: / SHEET: 01 OF 01
ALL DIMENSION ARE IN mm			


BOTTOM ARM PAIR NO : 08

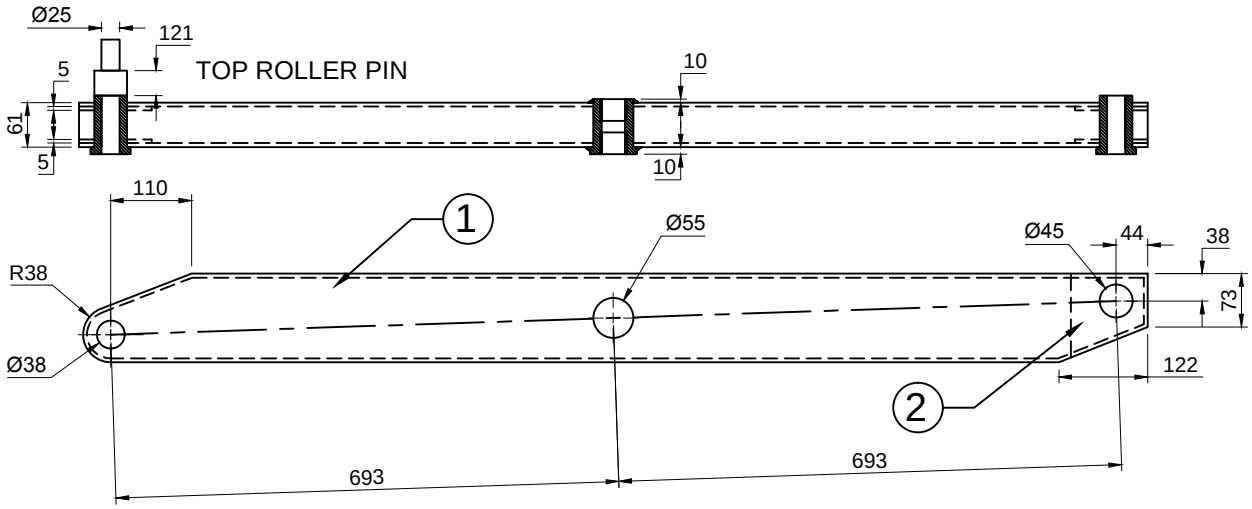

INNER ARM

1. R.TUBE 122 X 61 X 5.4 THK X 1470L = 2 NOS (LH / RH)
2. FLAT 100 X 5 X 100L = 4 NOS

TOP PIVOT BUSH

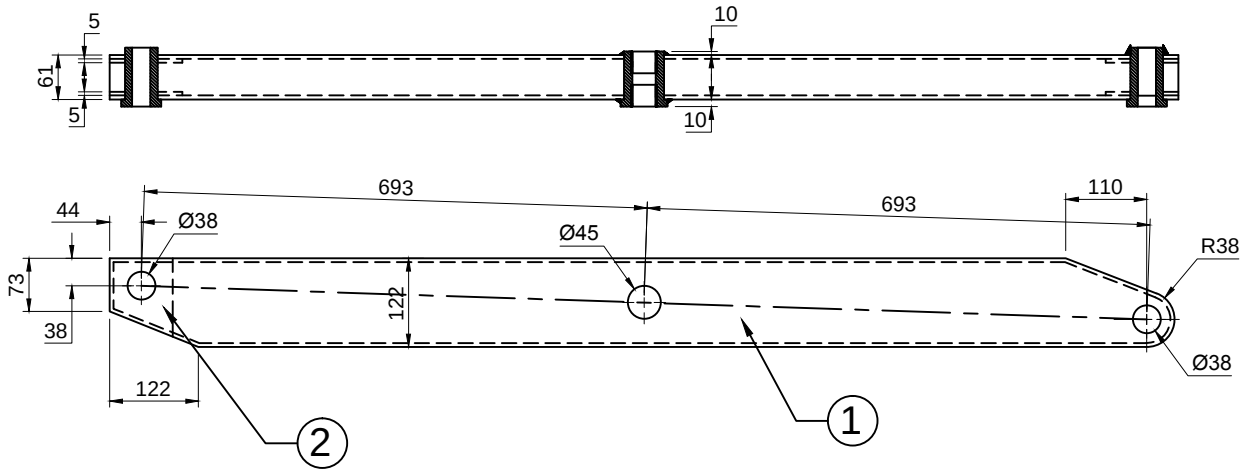


OUTER ARM

1. R.TUBE 122 X 61 X 5.4 THK X 1470L = 2 NOS (LH / RH)
2. FLAT 100 X 5 X 100L = 4 NOS

This drawing & design is the property of NIHVA TECHNOLOGIES. Not to be sold or copied to any other concern.

TITLE : - BOTTOM SCISSOR PAIR 08			NIHVA TECHNOLOGIES PVT. LTD. PUNE Tel : 020 66304033 Email:- info@nihva.com Website:- www.nihva.com
	SIGN	DATE	
DRAWN	P.A	04.10.2018	CLIENT -
CHECK	R.D	04.10.2018	PROJECT -
REV.			SITE -
APPROVAL			DWG. NO. : NIHVA/18-19/MFG/NSL/1018/012
If any queries contact : projects@nihva.com			SCALE: NTS / WT: / SHEET: 01 OF 01
ALL DIMENSION ARE IN mm			

BASE FRAME ASSLY WITH OUTRIGGERS

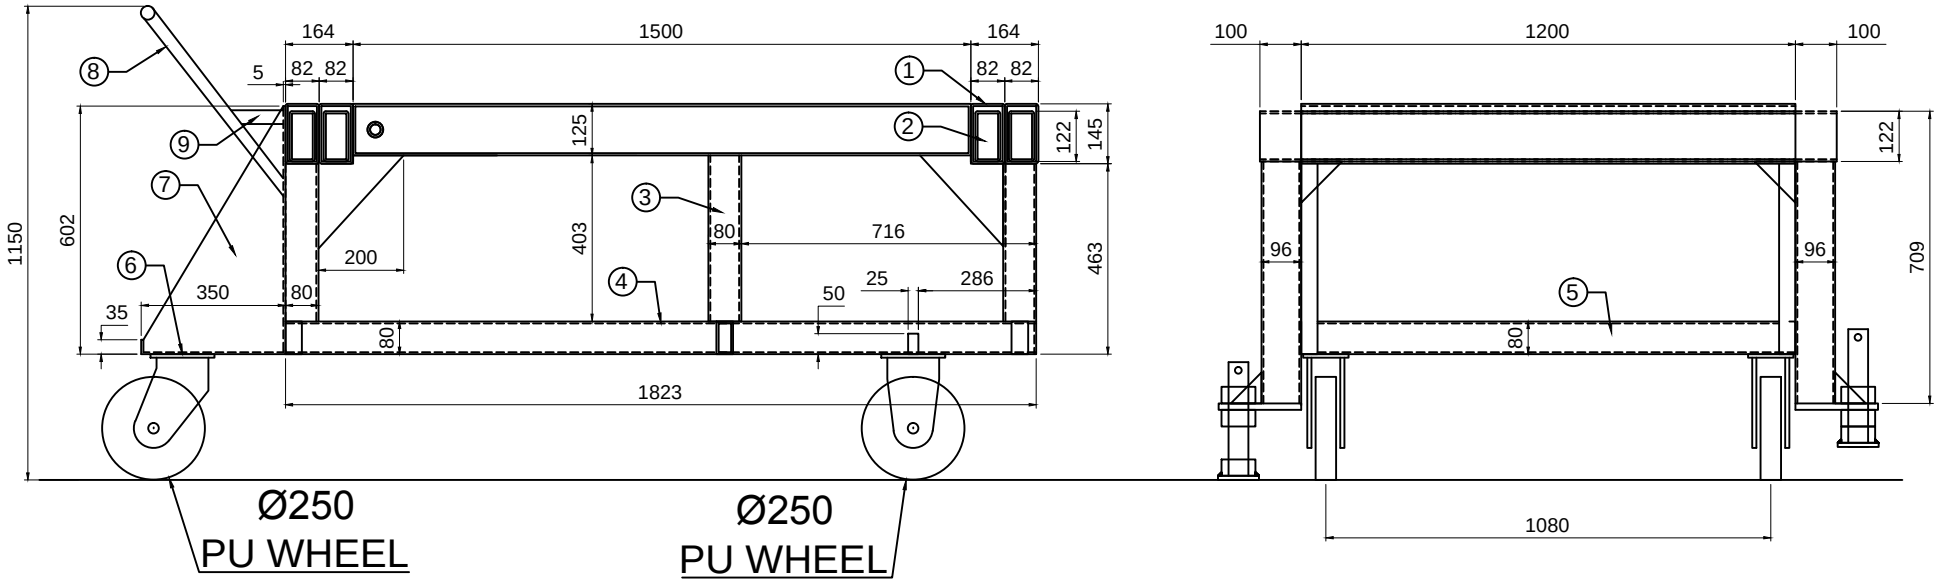


1. R.TUBE 145 x 82 x 5.4 THK X 1195L = 4 NOS (1 SIDE CLOSE BY 5 MM PLATE)
2. R.TUBE 122 x 61 x 5.4 THK X 1290L = 4 NOS (1 SIDE CLOSE BY 5 MM PLATE)
3. R.TUBE 80 x 40 x 4 THK X 403L = 6 NOS
4. R.TUBE 80 x 40 x 4 THK X 1818L = 2 NOS (1 SIDE CLOSE BY 5 MM PLATE)
5. R.TUBE 80 x 40 x 4 THK X 1120L = 3 NOS
6. FRONT PLATE = 1 NO
7. GUSSET = 2 NOS
8. PUSH PULL HANDLE = 1 NO
9. PUSH PULL HANDLE SUPPORT = 2 NOS

This drawing & design is the property of NIHVA TECHNOLOGIES. Not to be sold or copied to any other concern.


TITLE : - BASE FRAME WITH OUTRIGGER		
	SIGN	DATE
DRAWN	P.A	28.09.2018
CHECK	R.D	28.09.2018
REV.		
APPROVAL		
If any queries contact : projects@nihva.com		
ALL DIMENSION ARE IN mm		

NIHVA TECHNOLOGIES PVT. LTD.
NIHVA TECHNOLOGIES PVT. LTD. PUNE
Tel : 020 66304033
Email:- info@nihva.com
Website:- www.nihva.com


CLIENT -		
PROJECT -		
SITE -		
DWG. NO. : NIHVA/18-19/MFG/NSL/1018/013		
SCALE: NTS	WT:	SHEET: 01 OF 01

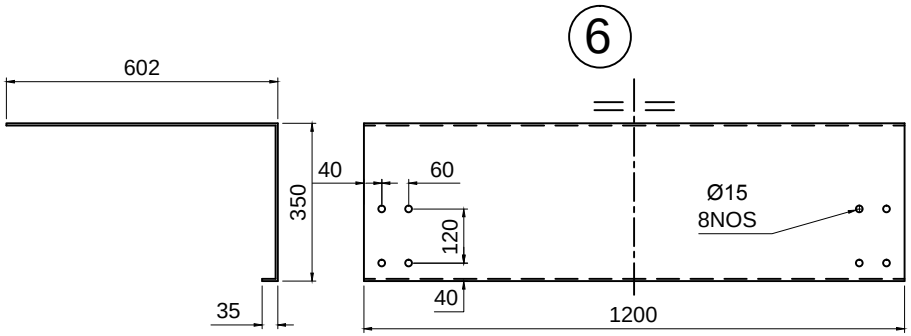

6. FRONT PLATE 965 X 5 THK X 1200L = 1 NO

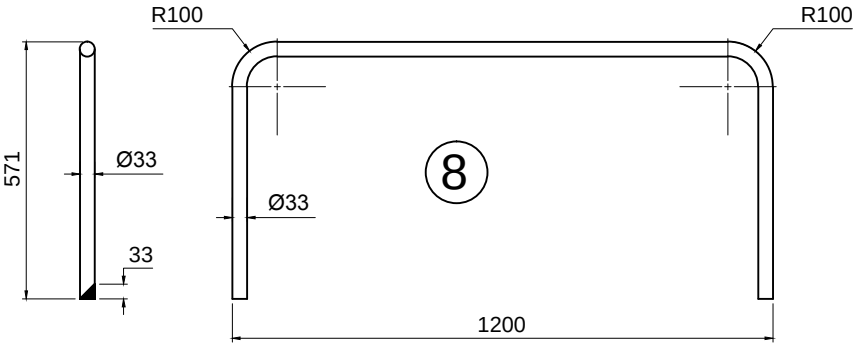

8. HANDLE OD 33 X 2340L = 1 NO

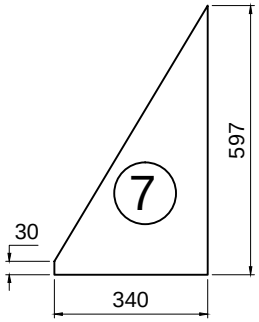

7. RIB 340X 5 THK X 597L = 2 NOS

This drawing & design is the property of NIHVA TECHNOLOGIES. Not to be sold or copied to any other concern.

TITLE : -

BASE FRAME DETAILS

	SIGN	DATE
DRAWN	P.A	04.10.2018
CHECK	R.D	04.10.2018
REV.		
APPROVAL		

NIHVA TECHNOLOGIES PVT. LTD.

NIHVA TECHNOLOGIES PVT. LTD. PUNE
Tel : 020 66304033
Email:- info@nihva.com
Website:- www.nihva.com

CLIENT -

PROJECT -

SITE -


DWG. NO. : NIHVA/18-19/MFG/NSL/1018/014

If any queries contact : projects@nihva.com


SCALE: NTS | WT: | SHEET: 01 OF 01

ALL DIMENSION ARE IN mm

OUTRIGGER ASSLY

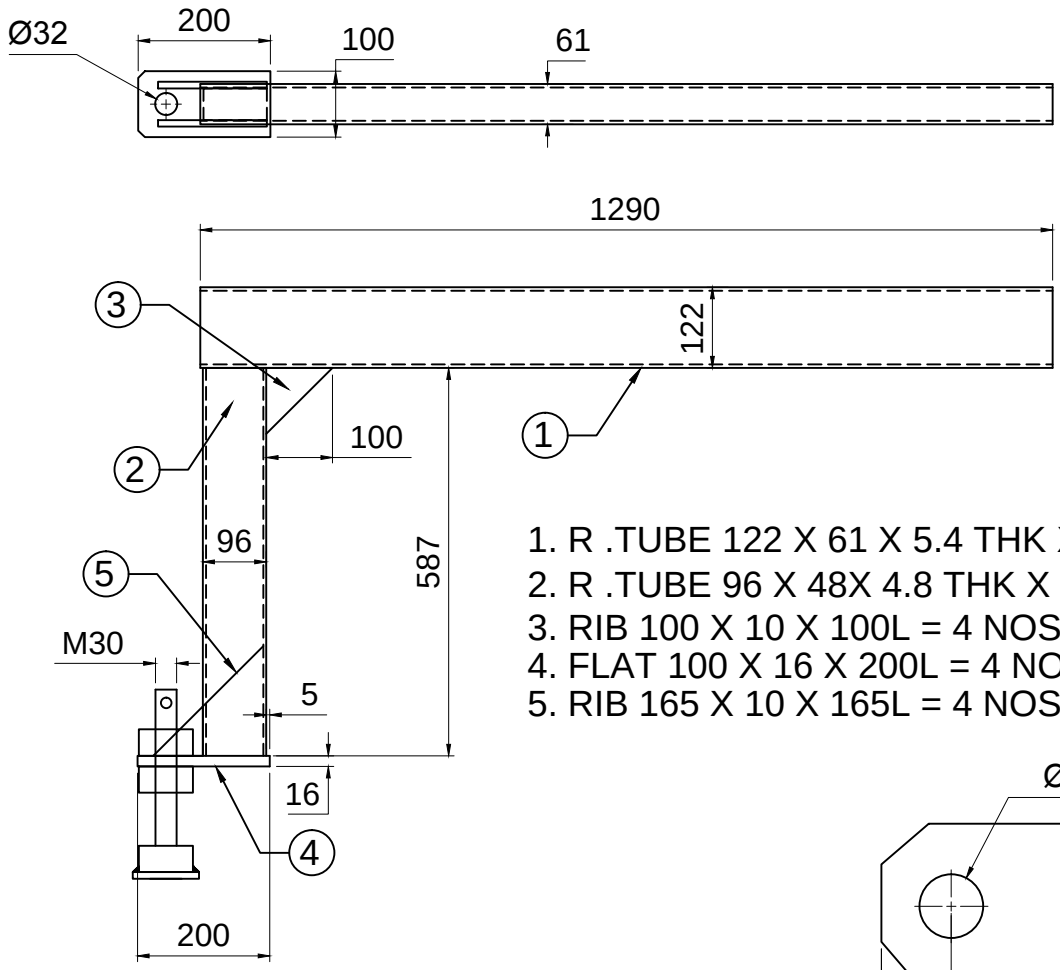


1. R .TUBE 122 X 61 X 5.4 THK X 1290L = 4 NOS
2. R .TUBE 96 X 48X 4.8 THK X 585L = 4 NOS
3. RIB 100 X 10 X 100L = 4 NOS
4. FLAT 100 X 16 X 200L = 4 NOS
5. RIB 165 X 10 X 165L = 4 NOS

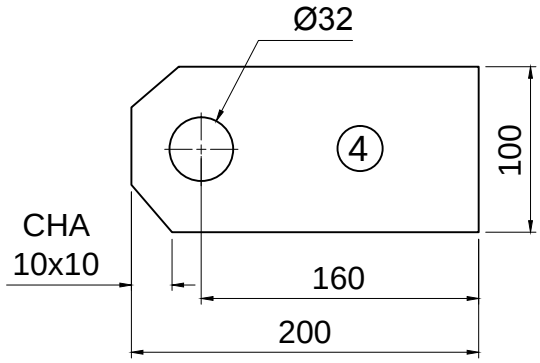

This drawing & design is the property of NIHVA TECHNOLOGIES. Not to be sold or copied to any other concern.

TITLE : - OUTRIGGER			NIHVA TECHNOLOGIES PVT. LTD. PUNE Tel : 020 66304033 Email:- info@nihva.com Website:- www.nihva.com
	SIGN	DATE	
DRAWN	P.A	04.10.2018	CLIENT -
CHECK	R.D	04.10.2018	PROJECT -
REV.			SITE -
APPROVAL			DWG. NO. : NIHVA/18-19/MFG/NSL/1018/015
If any queries contact : projects@nihva.com			SCALE: NTS / WT: / SHEET: 01 OF 01
ALL DIMENSION ARE IN mm			

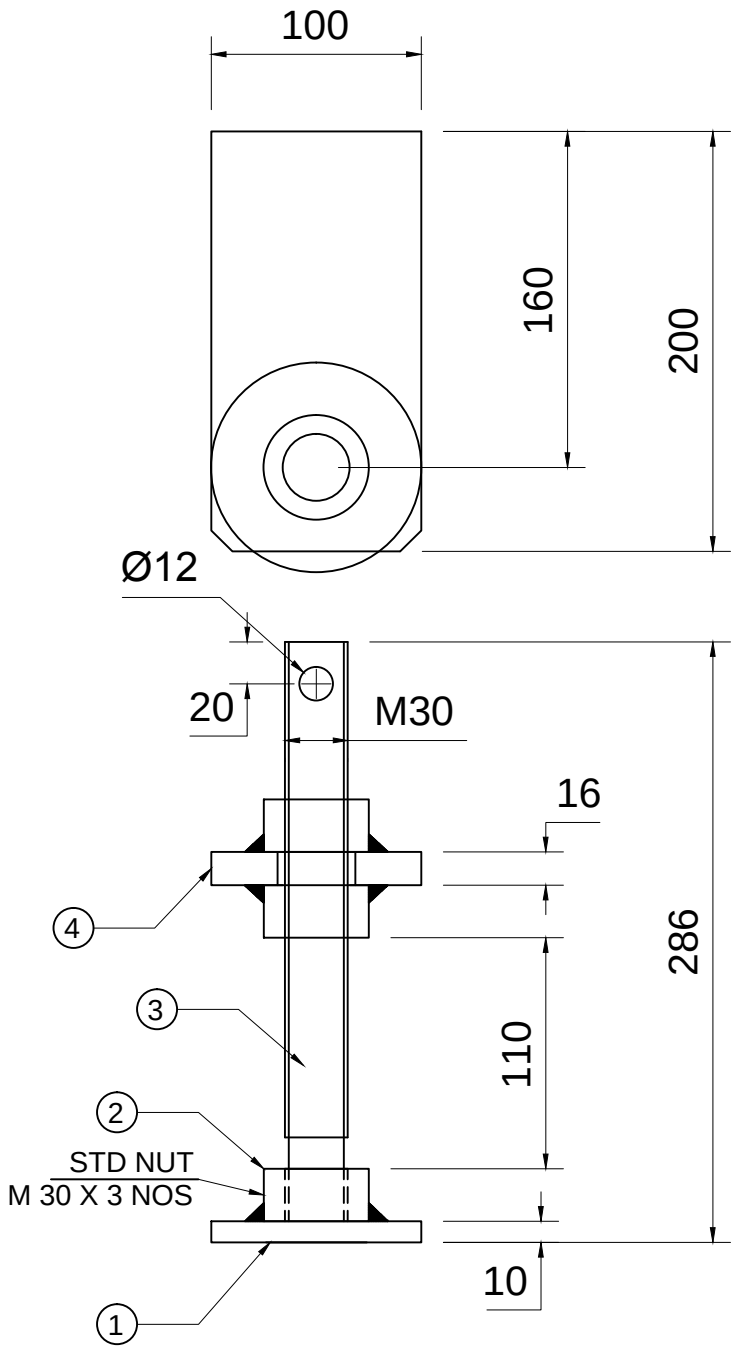


FLOOR LOCK ASSLY = 04 NOS

1. ROUND Ø100 X 10THK = 1 NOS
2. STD NUT M 30 = 3 NOS
3. STUD M 30 X 280L = 1 NO
4. FLAT 100 X 16 X 200 = 1 NO
5. MS BAR Ø12 X 200L = 4 NOS


This drawing & design is the property of NIHVA TECHNOLOGIES. Not to be sold or copied to any other concern.

TITLE : - FLOOR LOCK ASSLY			NIHVA TECHNOLOGIES PVT. LTD.
	SIGN	DATE	
DRAWN	P.A	04.10.2018	CLIENT -
CHECK	R.D	04.10.2018	PROJECT -
REV.			SITE -
APPROVAL			DWG. NO. : NIHVA/18-19/MFG/NSL/1018/016
If any queries contact : projects@nihva.com			SCALE: NTS | WT: | SHEET: 01 OF 01
ALL DIMENSION ARE IN mm			

NIHVA TECHNOLOGIES PVT. LTD. PUNE
Tel : 020 66304033
Email:- info@nihva.com
Website:- www.nihva.com

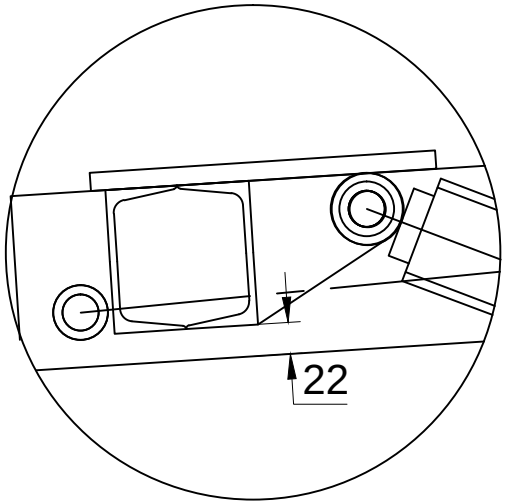

TOP BOX MOUNTING

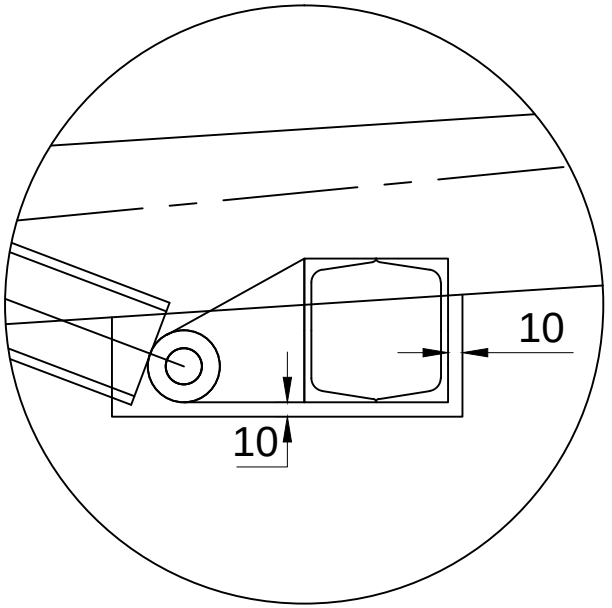

BOTTOM BOX MOUNTING

This drawing & design is the property of NIHVA TECHNOLOGIES. Not to be sold or copied to any other concern.

TITLE : -

BOX MOUNTING ASSLY

NIHVA TECHNOLOGIES PVT. LTD.

NIHVA TECHNOLOGIES PVT. LTD. PUNE
Tel : 020 66304033
Email:- info@nihva.com
Website:- www.nihva.com

	SIGN	DATE
DRAWN	P.A	04.10.18
CHECK	R.D	04.10.18
REV.		
APPROVAL		

CLIENT -

PROJECT -

SITE -


DWG. NO. : NIHVA/18-19/MFG/NSL/1018/017

If any queries contact : projects@nihva.com


SCALE: NTS | WT: | SHEET: 01 OF 01

ALL DIMENSION ARE IN mm


HYD. CYLINDER BOX

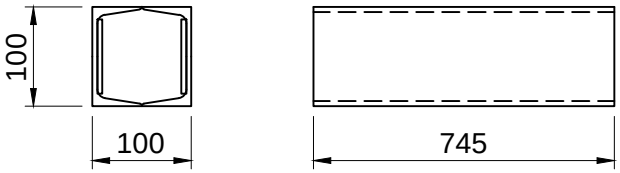


CYLINDER TOP BOX
ISMC 100 X 50 X 750L(M/C 745) = 4 NOS
FLAT 75 X 6 X 745L = 4 NOS

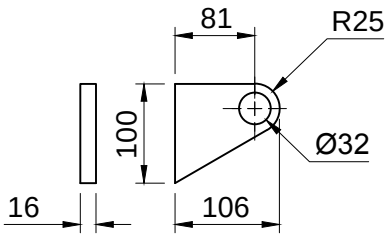


PROFILE 100 X 16 X 106L = 6 NOS

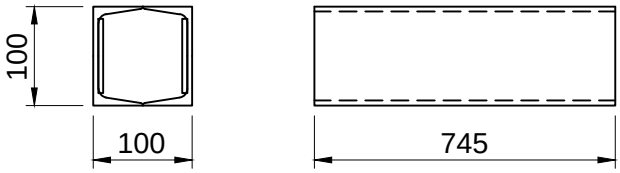

BOTTOM CYLINDER BOTTOM BOX
ISMC 100 X 50 X 750L(M/C 745) = 2 NOS
FLAT 75 X 6 X 745L = 2 NOS

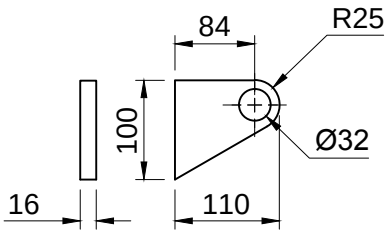

PROFILE 100 X 16 X 110L = 4 NOS

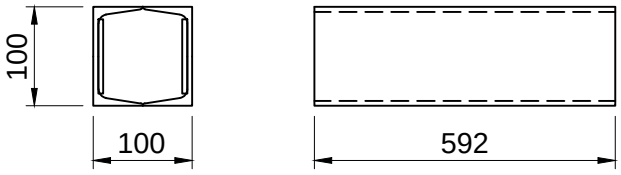


TOP CYLINDER BOTTOM BOX
ISMC 100 X 50 X 595L(M/C 592) = 2 NOS
FLAT 75 X 6 X 592L = 2 NOS

This drawing & design is the property of NIHVA TECHNOLOGIES. Not to be sold or copied to any other concern.

TITLE : - HYD. CYLINDER BOX DETAILS			NIHVA TECHNOLOGIES PVT. LTD.
	SIGN	DATE	
DRAWN	P.A	04.10.18	CLIENT -
CHECK	R.D	04.10.18	PROJECT -
REV.			SITE -
APPROVAL			DWG. NO. : NIHVA/18-19/MFG/NSL/1018/018
If any queries contact : projects@nihva.com			SCALE: NTS | WT: | SHEET: 01 OF 01
ALL DIMENSION ARE IN mm			

NIHVA TECHNOLOGIES PVT. LTD. PUNE
Tel : 020 66304033
Email:- info@nihva.com
Website:- www.nihva.com

OUTRIGGER ASSLY

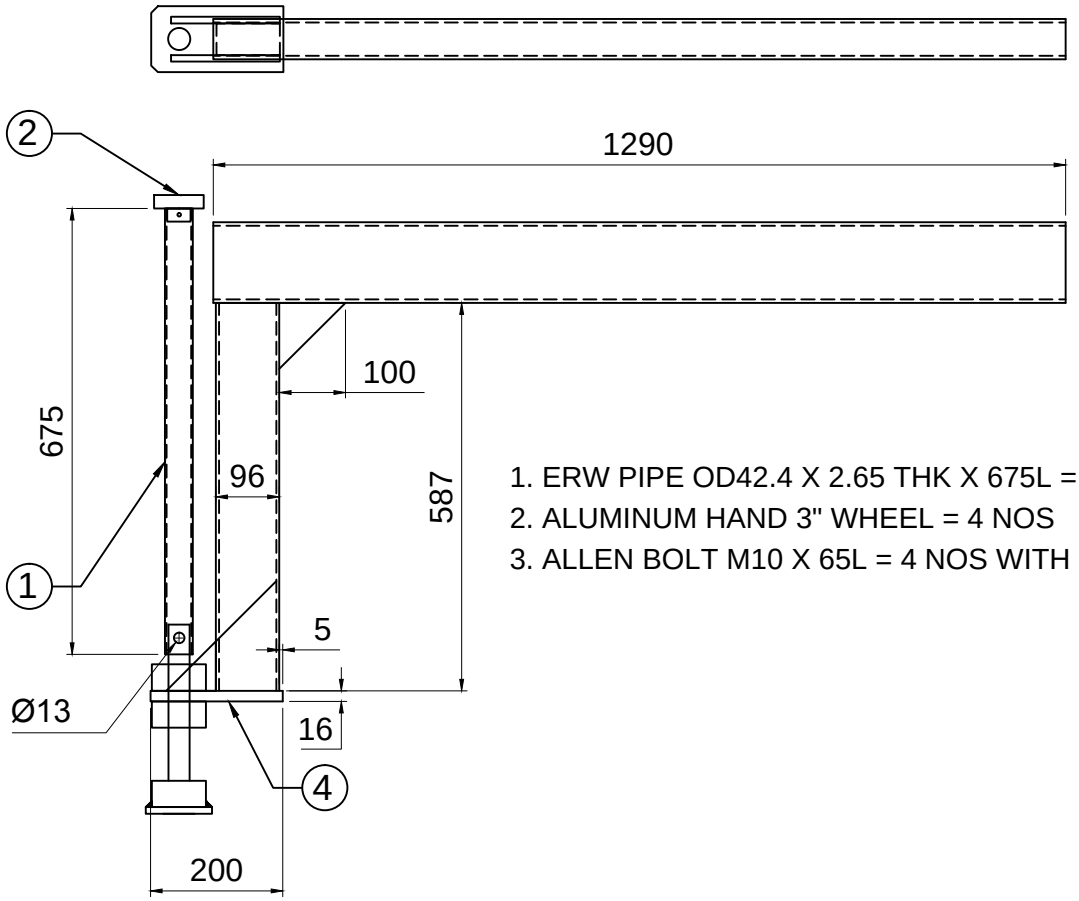

1. ERW PIPE OD42.4 X 2.65 THK X 675L = 4 NOS
2. ALUMINUM HAND 3" WHEEL = 4 NOS
3. ALLEN BOLT M10 X 65L = 4 NOS WITH SPRING WASHER

This drawing & design is the property of NIHVA TECHNOLOGIES. Not to be sold or copied to any other concern.

TITLE : - OUTRIGGER			NIHVA TECHNOLOGIES PVT. LTD. PUNE Tel : 020 66304033 Email:- info@nihva.com Website:- www.nihva.com
	SIGN	DATE	
DRAWN	P.A	04.10.2018	CLIENT -
CHECK	R.D	04.10.2018	PROJECT -
REV.			SITE -
APPROVAL			DWG. NO. : NIHVA/18-19/MFG/NSL/1018/019
If any queries contact : projects@nihva.com			SCALE: NTS | WT: | SHEET: 01 OF 01
ALL DIMENSION ARE IN mm			