

Prinzipzeichnung
RapidRoll 300 plus


General Drawing


RapidRoll 300 plus


ALBANY
ASSA ABLOY

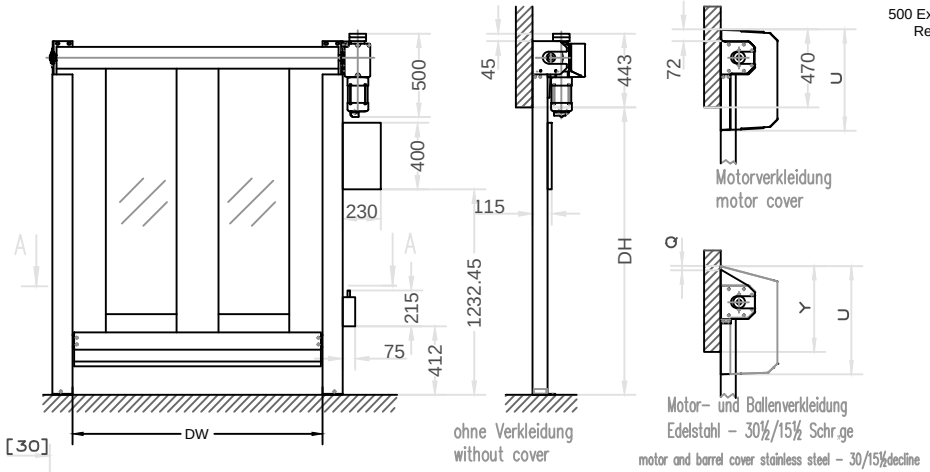

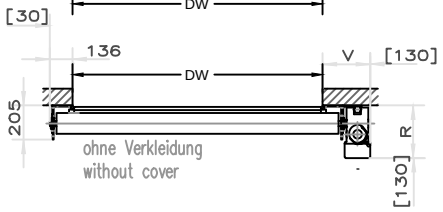

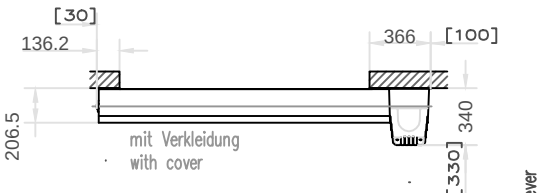

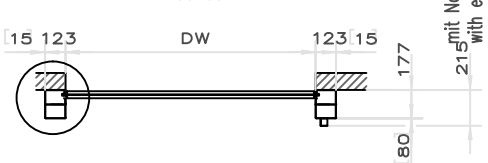

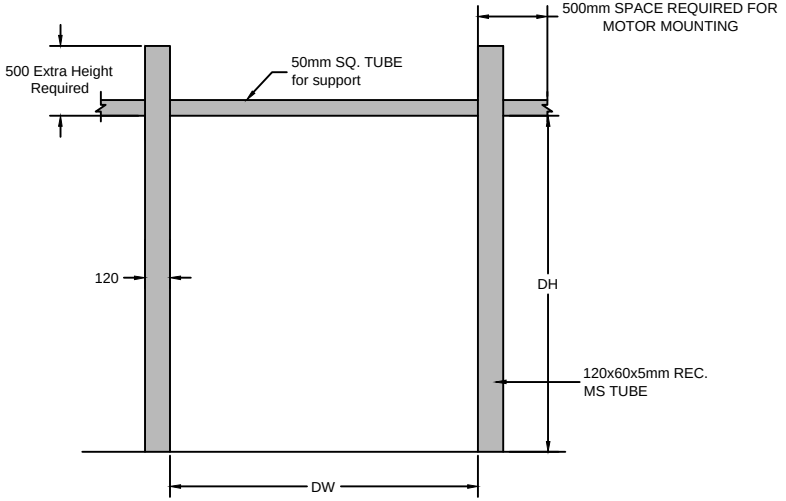

STRUCTURE FOR HSD

	Without motorcover
	ACS 50 / MCC / without control
X	443
V	285
R	315, if DW<=4000 and DH<=4200
R	325, if DW>4000 or DH>4200 and Alu side frames
T	500
P	45

	With motorcover		
	Plastic	Steel	Stainless steel
Y	470	465	515
W	366	362	362
S	340	340	340
U	610	600	650
Q	70	65	18(30½), 115(0½)

DOOR WIDTH (DW)	DOOR HEIGHT (DH)	QUANTITY
2000	2200	1

DIMENSION :

CLEAR WIDTH	CLEAR HEIGHT	QUANTITY
2000 mm	2200 mm	01

MATERIAL :

THICKNESS :

NOTE: REQUIRED STRUCTURE FOR DOOR SHALL BE IN CLIENT'S SCOPE.

NIHVA TECHNOLOGIES PVT. LTD.

NIHVA TECHNOLOGY PVT. LTD. PUNE
Email:- info@nihva.com
Website:- www.nihva.com

TITLE:

HIGH SPEED DOOR (RR 300 PLUS)

CLIENT'S APPROVAL :

CLIENT - LUPIN PHARMA

PROJECT -

SITE LOCATION - SIKKIM

DWG. NO. : NIHVA/16-17/0079/R02

SCALE: NTS	WT:	SHEET:1 OF 1

DRAWN BY: OMKAR	DATE: 25-10-2016
CHECK : ANIL	DATE: 25-10-2016

If any queries contact : projects@nihva.com

NOTE: ALL DIMENSION ARE IN mm

THIS DRAWING & DESIGNING IS THE PROPERTY OF NIHVA TECHNOLOGIES. NOT BE SOLD OR COPY TO ANY OTHER CONCERN.