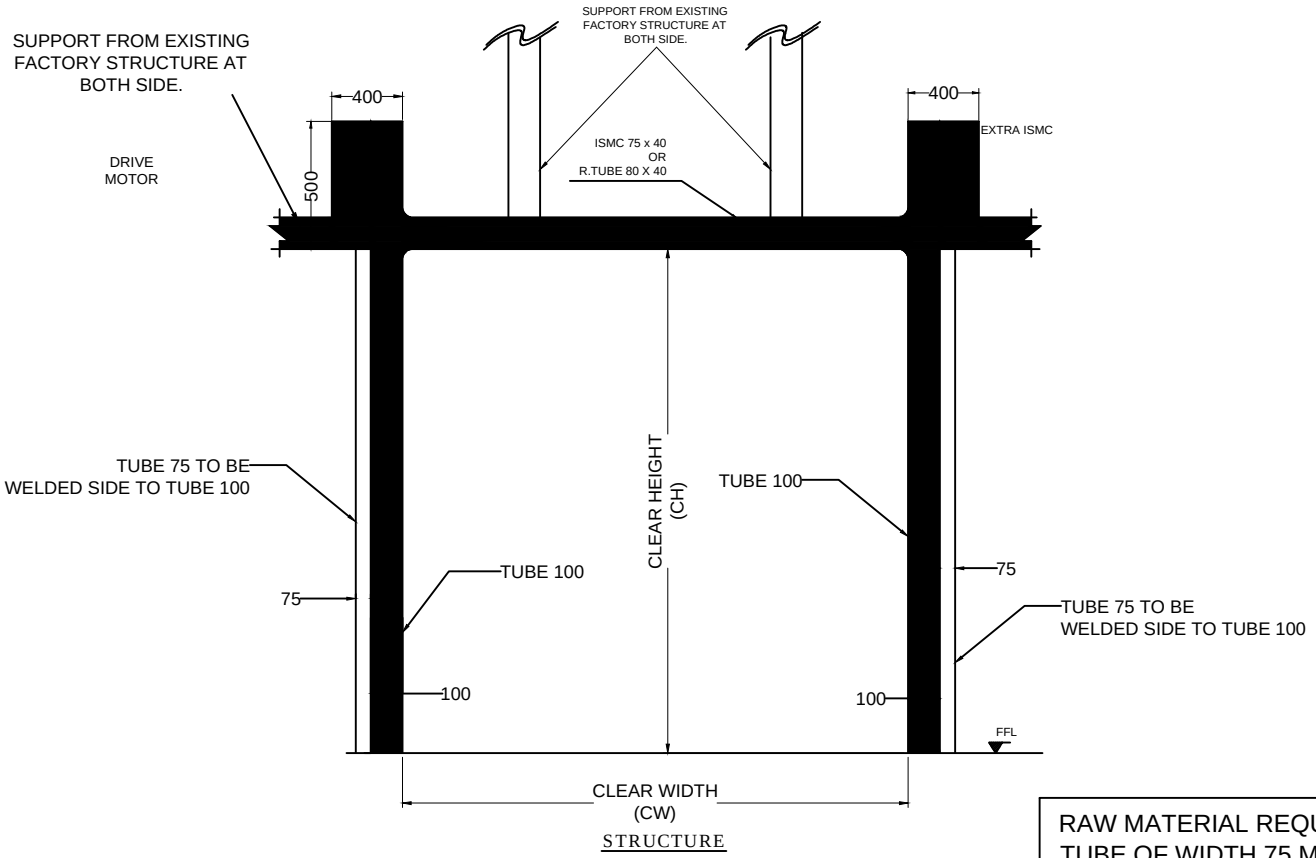

STRUCTURE

RAW MATERIAL REQUIRED FOR MODIFICATION -
TUBE OF WIDTH 75 MM
LENGTH = 3560 mm QTY- 2 NOS

NOTES-
(1) REQUIRED MS STRUCTURE & FITTING IN CLIENT SCOPE.
(2) ALL SITE CIVIL WORK IN CLIENT SCOPE .
(3) ROLLING SHUTTER WILL BE ONLY INSTALLED AFTER STRUCTURE READINESS AS PER DRAWING PROVIDED.

5000 mm	3560 mm	1 NO
CLEAR WIDTH	CLEAR HEIGHT	QUANTITY

This drawing & design is the property of NIHVA TECHNOLOGIES. Not to be sold or copied to any other concern.

TITLE DOUBLE WALL ROLLING SHUTTER STRUCTURE

NIHVA TECHNOLOGIES PVT. LTD.
NIHVA TECHNOLOGIES PVT. LTD. PUNE
Tel : 020 66304033
Email:- info@nihva.com
Website:- www.nihva.com

	NAME	SIGN	DATE
DRAWN	S.M.S.		09.10.2020
CHECK			
APPRD.			

CLIENT - M A ENGINEERING
PROJECT - JOHN DEERE INDIA PVT LTD
SITE LOCATION - PUNE
If any queries contact : projectsupport@nihva.com
DWG. NO. : NIHVA/20-21/0088 REV- R00
ALL DIMENSION ARE IN mm
SCALE: NTS WT: SHEET: