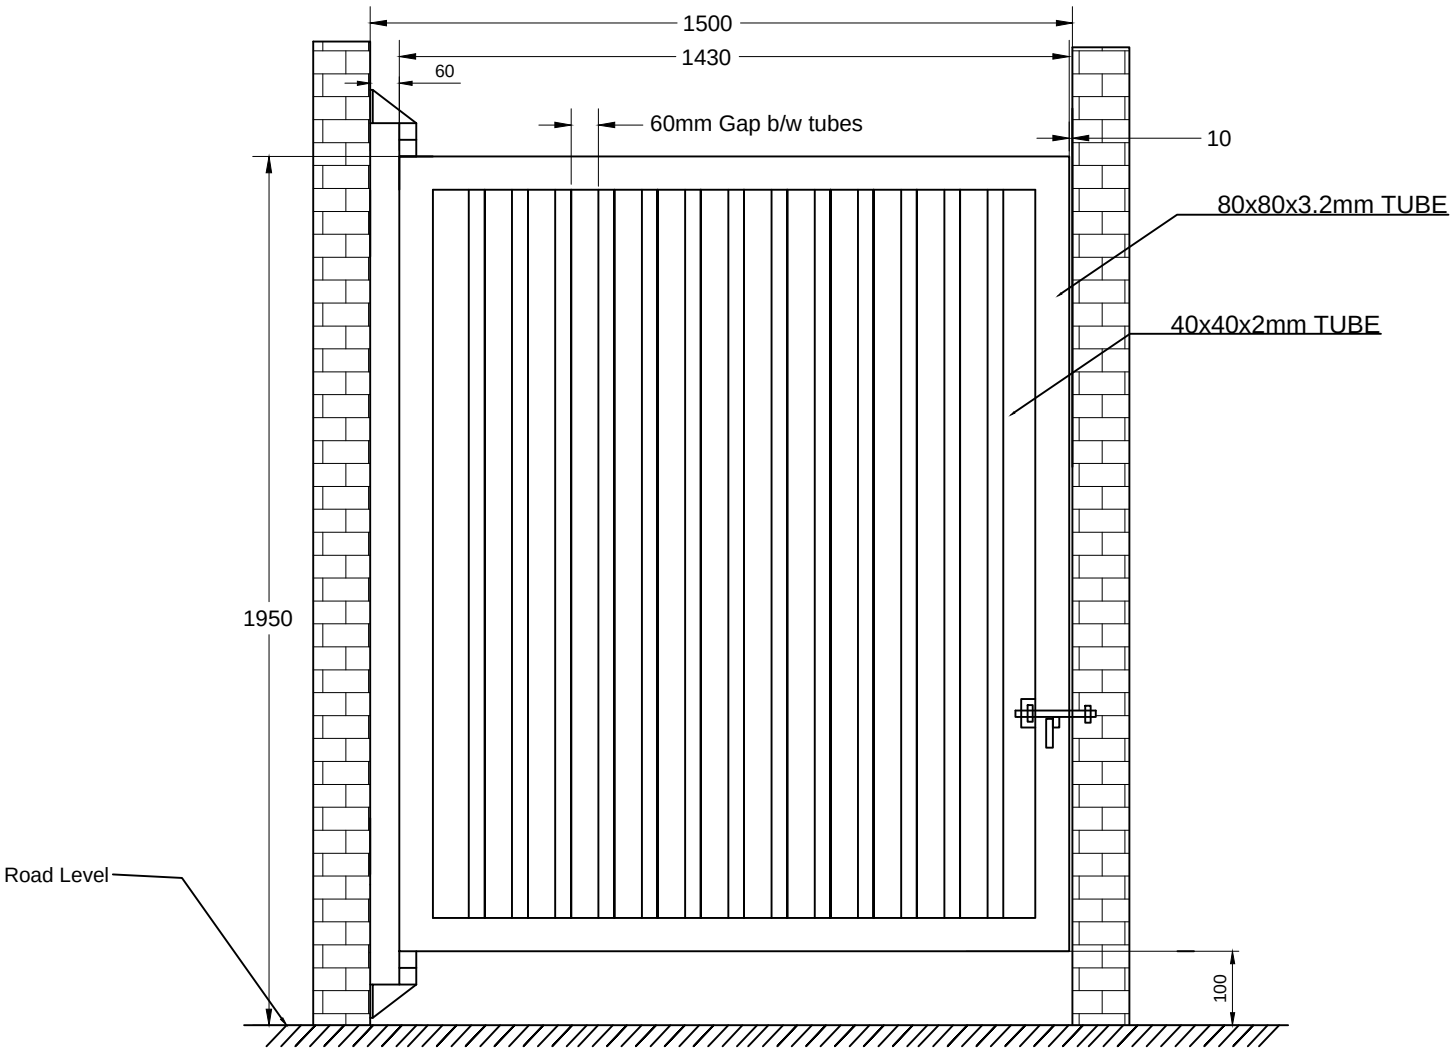

INSIDE ELEVATION

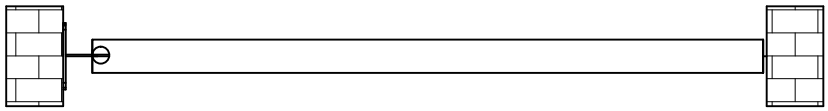

PLAN

This drawing & designing is the property of NIHVA TECHNOLOGIES. Not be sold or copy to any other concern.

TITLE: WICKET GATE	ALL DIMENSION ARE IN mm			NIHVA TECHNOLOGY PVT. LTD. PUNE Tel : 020 66304033 Email:- info@nihva.com Website:- www.nihva.com
		SIGN	DATE	
	DRAWN	OMKAR	09/06/16	CLIENT -MAHINDRA WINDOOR SOLUTION
CLIENT APPROVAL	CHECK	ANIL	09/06/16	PROJECT -AUROBINDO PHARMA LIMITED
	REV.	01		SITE -
	APPRD.			DWG. NO. -NIHVA/16-17/0027
	MFG			SCALE: NTS | WT: | SHEET: 01 OF 01
	Ref. No.			If any queries contact : projects@nihva.com