
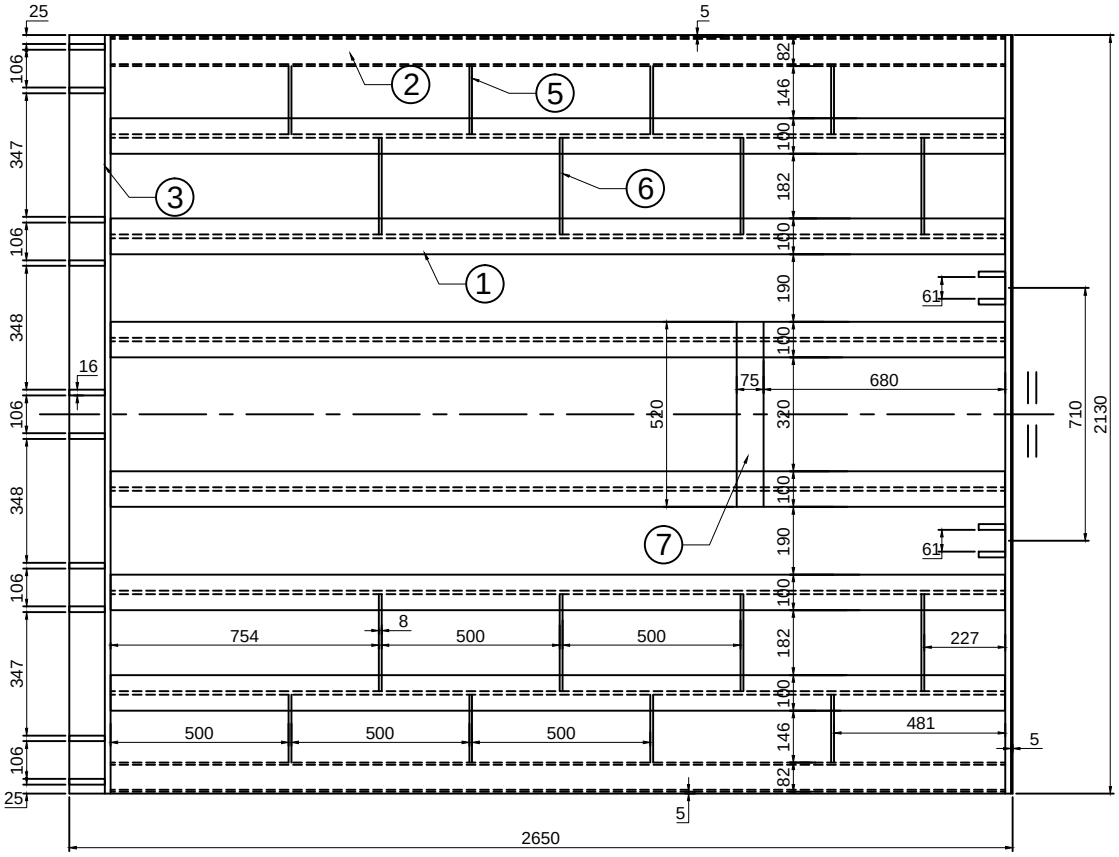


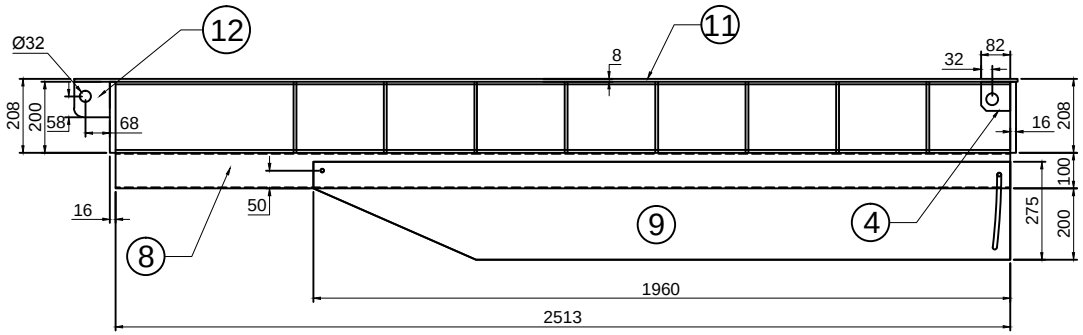

NOTE:~ MTL : MS

PART NO.	PART NAME	DESCRIPTION	QTY
1.	ISMB	200 X 100 X 2510L	6 NOS
2.	R.TUBE	145 X 82 X 5.4THK X 2510L	2 NOS
3.	FLAT	200 X 16 X 2130L	2 NOS
4.	PROFILE	82 X 16 X 82L	4 NOS
5.	FLAT	190 X 8 X 190L	8 NOS
6.	FLAT	272 X 8 X 270L	8 NOS
7.	FLAT	75 X 6 X 520L	1 NOS
8.	BEND	100 X 3THK X 2510L	2 NOS
9.	SIDE COVER	275 X 3THK X 1960L	2 NOS
10.	LIP STOPER	Ø20 X 50L	4 NOS
11.	CHEQ.SHEET	2130 X 8 THK X 2650L	1 NO
12.	PROFILE	100 X 16 X 100L	10 NOS
13.	EYE BOLT	M16 X STD WITH NUT	3 NOS

This drawing & design is the property of NIHVA TECHNOLOGIES. Not to be sold or copied to any other concern.

TITLE: DECK ASSLY

	NAME	SIGN	DATE
DRAWN	P.V.A		20.06.2019
CHECK	V.M.T		20.06.2019
APPRD.			

NIHVA TECHNOLOGIES PVT. LTD.
NIHVA TECHNOLOGIES PVT. LTD. PUNE
Tel : 020 66304033
Email:- info@nihva.com
Website:- www.nihva.com

CLIENT -

PROJECT - NDL451

SITE LOCATION -

If any queries contact : design@nihva.com

DWG. NO. : NIHVA/19-20/VDR/073

ALL DIMENSION ARE IN mm | SCALE: NTS | WT: | REV- 00