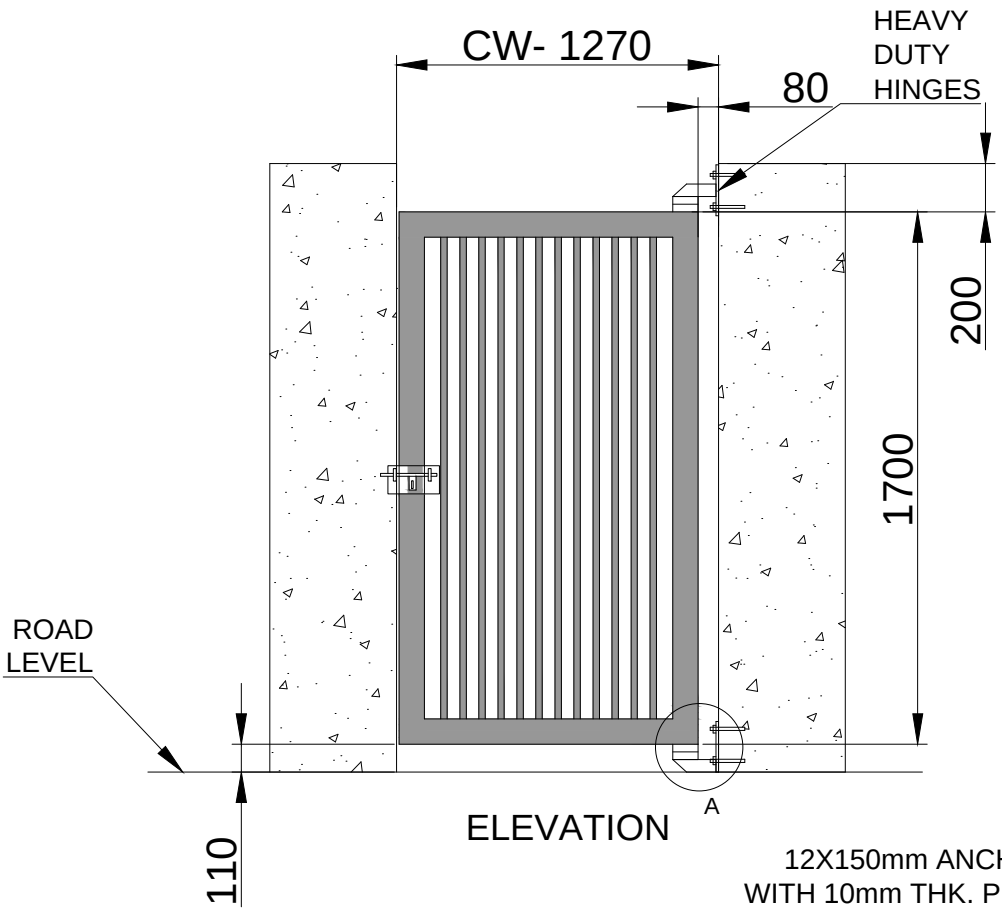

ELEVATION

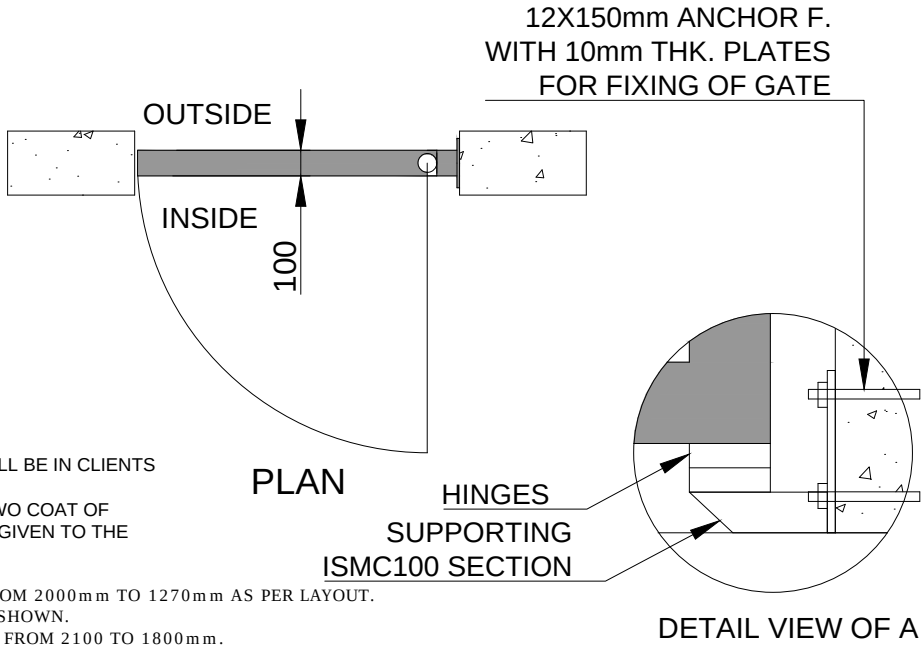

PLAN

DETAIL VIEW OF A

NOTE-
1. ALL REQUIRED CIVIL WORK WILL BE IN CLIENTS SCOPE.
2. ONE COAT OF RED OXIDE & TWO COAT OF APPROVED RAL SHADE WILL BE GIVEN TO THE GATE.

REV 1- CLEAR WIDTH REVISED FROM 2000mm TO 1270mm AS PER LAYOUT. ALSO FIXING DETAILS ARE ALSO SHOWN.
REV 2- HEIGHT OF GATE REVISED FROM 2100 TO 1800mm.
REV 3- HEIGHT OF GATE REVISED FROM 1800 TO 1700mm.

GATE WIDTH	GATE HEIGHT	QUANTITY	LOCATION
1270mm	1800 mm	1 NOS	SECURITY CABIN 3

This drawing & design is the property of NIHVA TECHNOLOGIES. Not to be sold or copied to any other concern.

TITLE

WICKET GATE
1.27X1.8m

CLIENT APPROVAL

ALL DIMENSION ARE IN mm

NIHVA TECHNOLOGIES PVT. LTD.

NIHVA TECHNOLOGIES
PVT. LTD. PUNE
Tel : 020 66304033
Email:- info@nihva.com
Website:- www.nihva.com

	SIGN	DATE
DRAWN	OMKAR	08/11/17
CHECK	SHEKHAR	08/11/17
REV.		
APPRD.	SHEKHAR	08/11/17
MFG		
Ref. No.		

CLIENT - LUPIN LIMITED
PROJECT -
SITE - MIHAN, NAGPUR
DWG. NO. - NIHVA/17-18/0254/R03 | REV-3
SCALE: NTS | WT: | SHEET: 01 OF 01
If any queries contact : projects@nihva.com