


DWG.NO: SALT_1714_STR_01_R1

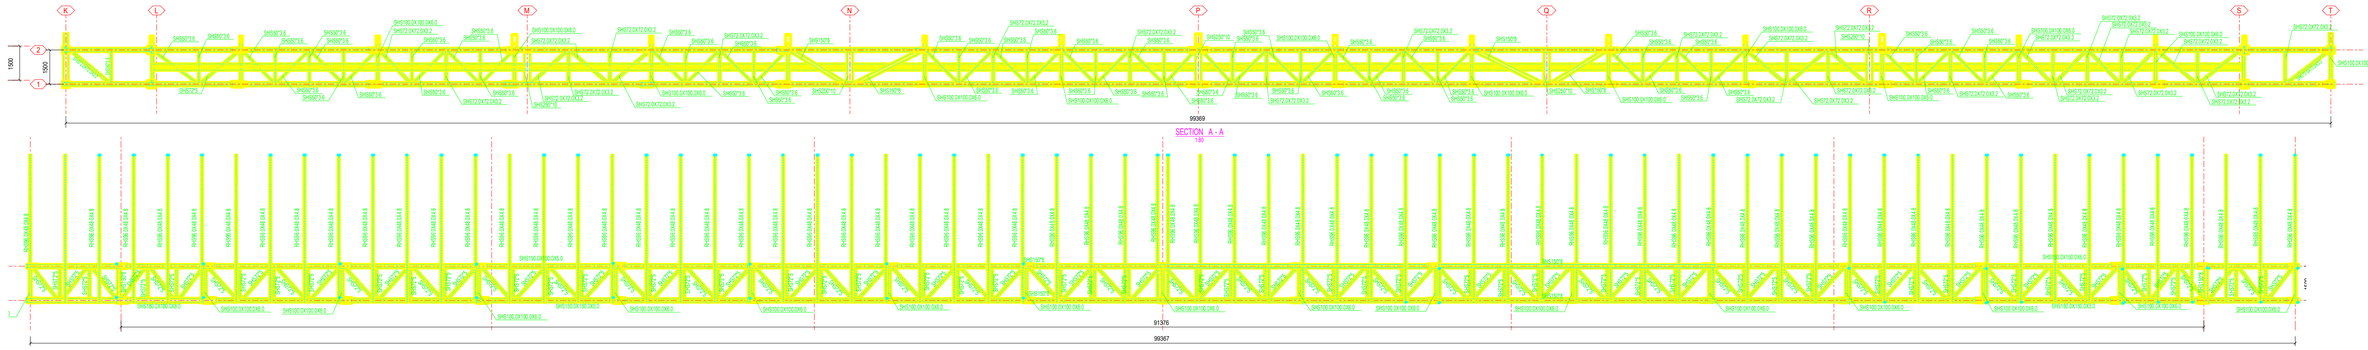


SECTION A - A
1:80

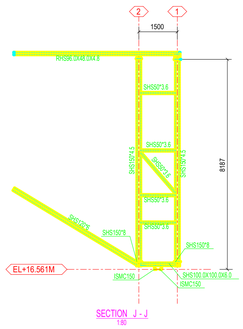


SECTION J - J
1:80

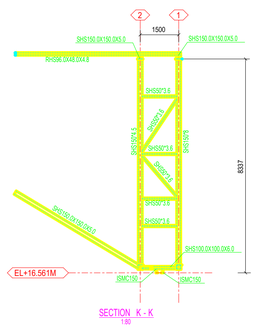


SECTION K - K
1:80

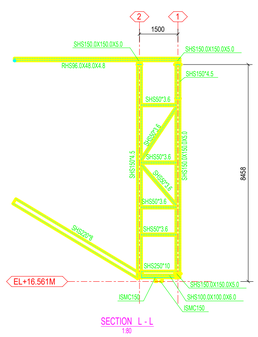


SECTION L - L
1:80

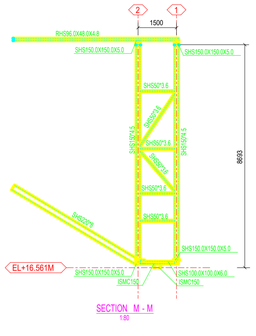


SECTION M - M
1:80

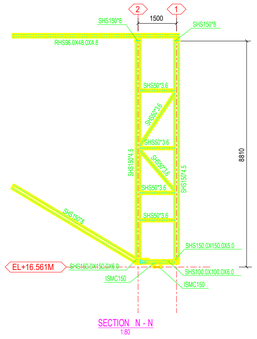


SECTION N - N
1:80

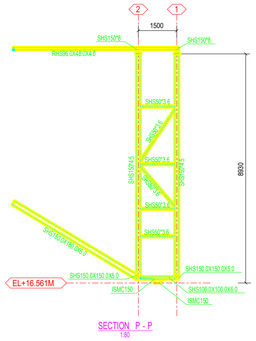


SECTION P - P
1:80

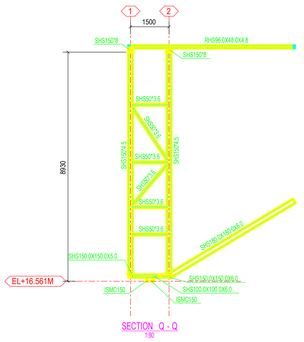


SECTION Q - Q
1:80

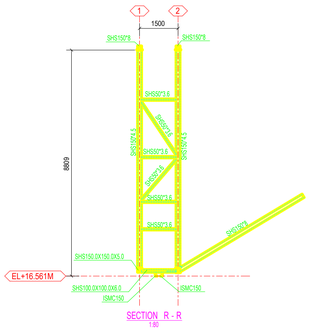


SECTION R - R
1:80

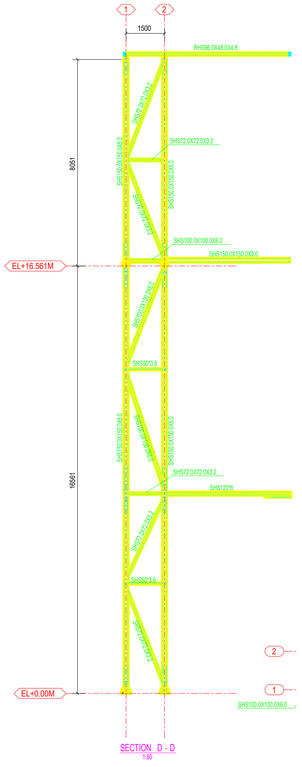


SECTION D - D
1:80

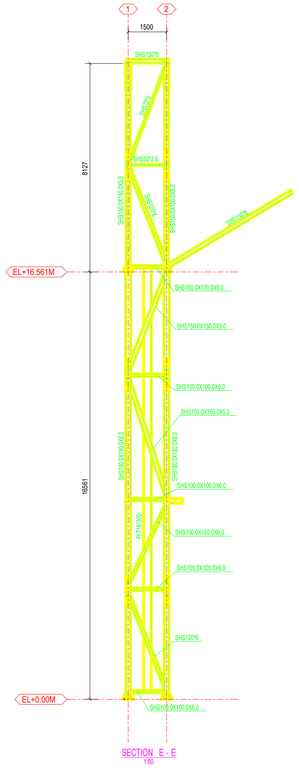


SECTION E - E
1:80

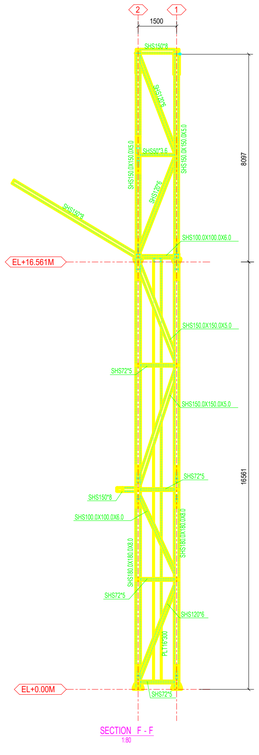


SECTION F - F
1:80

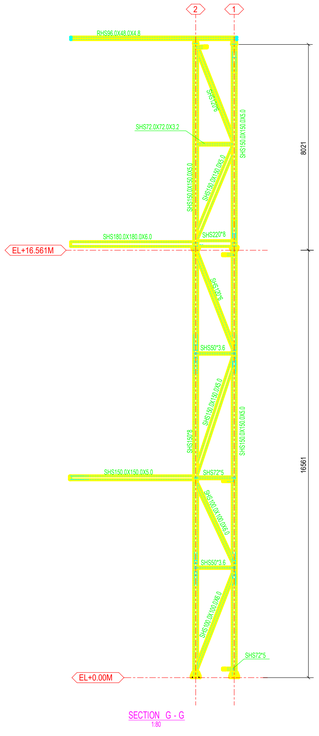


SECTION G - G
1:80

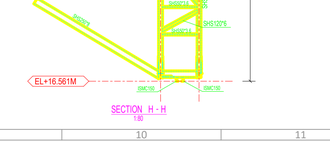


SECTION U - U
1:80

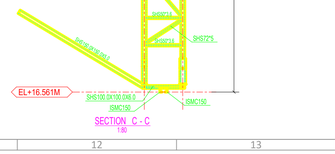


SECTION V - V
1:80

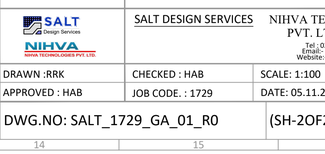


SECTION W - W
1:80

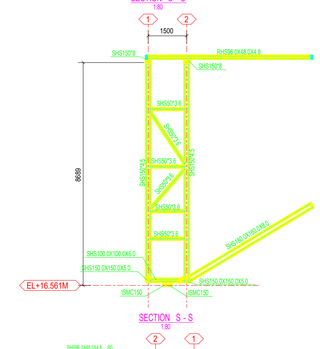


SECTION S - S
1:80

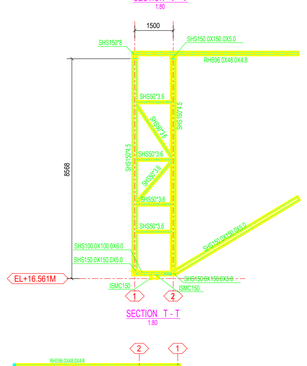

SECTION T - T
1:80

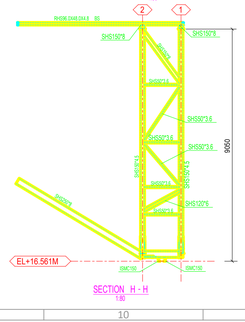

SECTION H - H
1:80

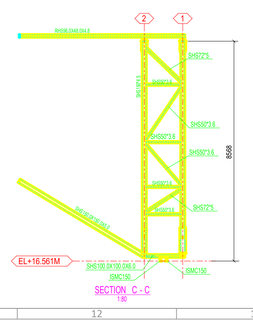

SECTION C - C
1:80

NOTES :-

1. ALL DIMENSIONS ARE IN MM & LEVEL ARE IN METER.
2. ALL STRUCTURAL STEEL AS PER IS:2062.
3. PROVIDE WELDING AS PER IS:816.
4. PROVIDE MIN. 6MM SHOP WELD AND 8MM SITE WELD
5. USE ELECTRODS AS PER IS:814 (PT.-I).
6. FILLET/ BUTT WELD SHALL BE OF 6MM SIZE AND SHALL BE CONTINUOUS.
7. FABRICATION AND ERECTION SHALL BE AS PER IS:800 AND IS:803.
8. WELD SHALL BE GROUND SMOOTH.
9. ALL GUSSET PLATES SHALL BE MIN. 8 THK.
10. ALL M.S. BLACK BOLTS AND NUTS SHALL CONFORM TO IS:1363(PT. 1 TO 3).
11. LIVE LOAD ON ROOF = 75KG/SQM.
12. STRUCTURE SHALL BE APPLIED WITH ONE COAT OF RED OXIDE ZINC CROMATE PRIMER AFTER FABRICATION FOLLOWED ONE MORE COAT BEFORE ERECTION. FINALLY APPLY 2 COATS OF SYNTHETIC ENAMAL OF APPROVED QUALITY.
13. STRUCTURAL MEMBER SHALL BE OF 355N/MM^2 MIN STRENGTH.

REV.NO.	DESCRIPTION.	REV.DATE	DRAWN.	CHKD.	APPD.
0	GA DRAWING FOR APPROVAL	05.11.22	MEGHA	HAB	HAB

DWG.TITLE :- SECTION VIEW FOR DOOR FRAME (99M)

PROJECT	MEGADOOR INSTALLATION AT HYDRABAD AIRPORT
CLIENT	GMR

SALT Design Services
NIHVA TECHNOLOGIES PVT. LTD.

SALT DESIGN SERVICES
NIHVA TECHNOLOGIES PVT. LTD. PUNE
Tel : 020 66304033
Email:- info@nihva.com
Website:- www.nihva.com

DRAWN :RRK	CHECKED : HAB	SCALE: 1:100
APPROVED : HAB	JOB CODE. : 1729	DATE: 05.11.2022

DWG.NO: SALT_1729_GA_01_R0 (SH-2OF2) REV. - R0 SIZE. - A0

A1 (841 x 594)