CAPACITY	20 TON
BAILING CHAMBER	1000L X 500W X 1000H
BAIL SIZE	1000L X 500W X 300H

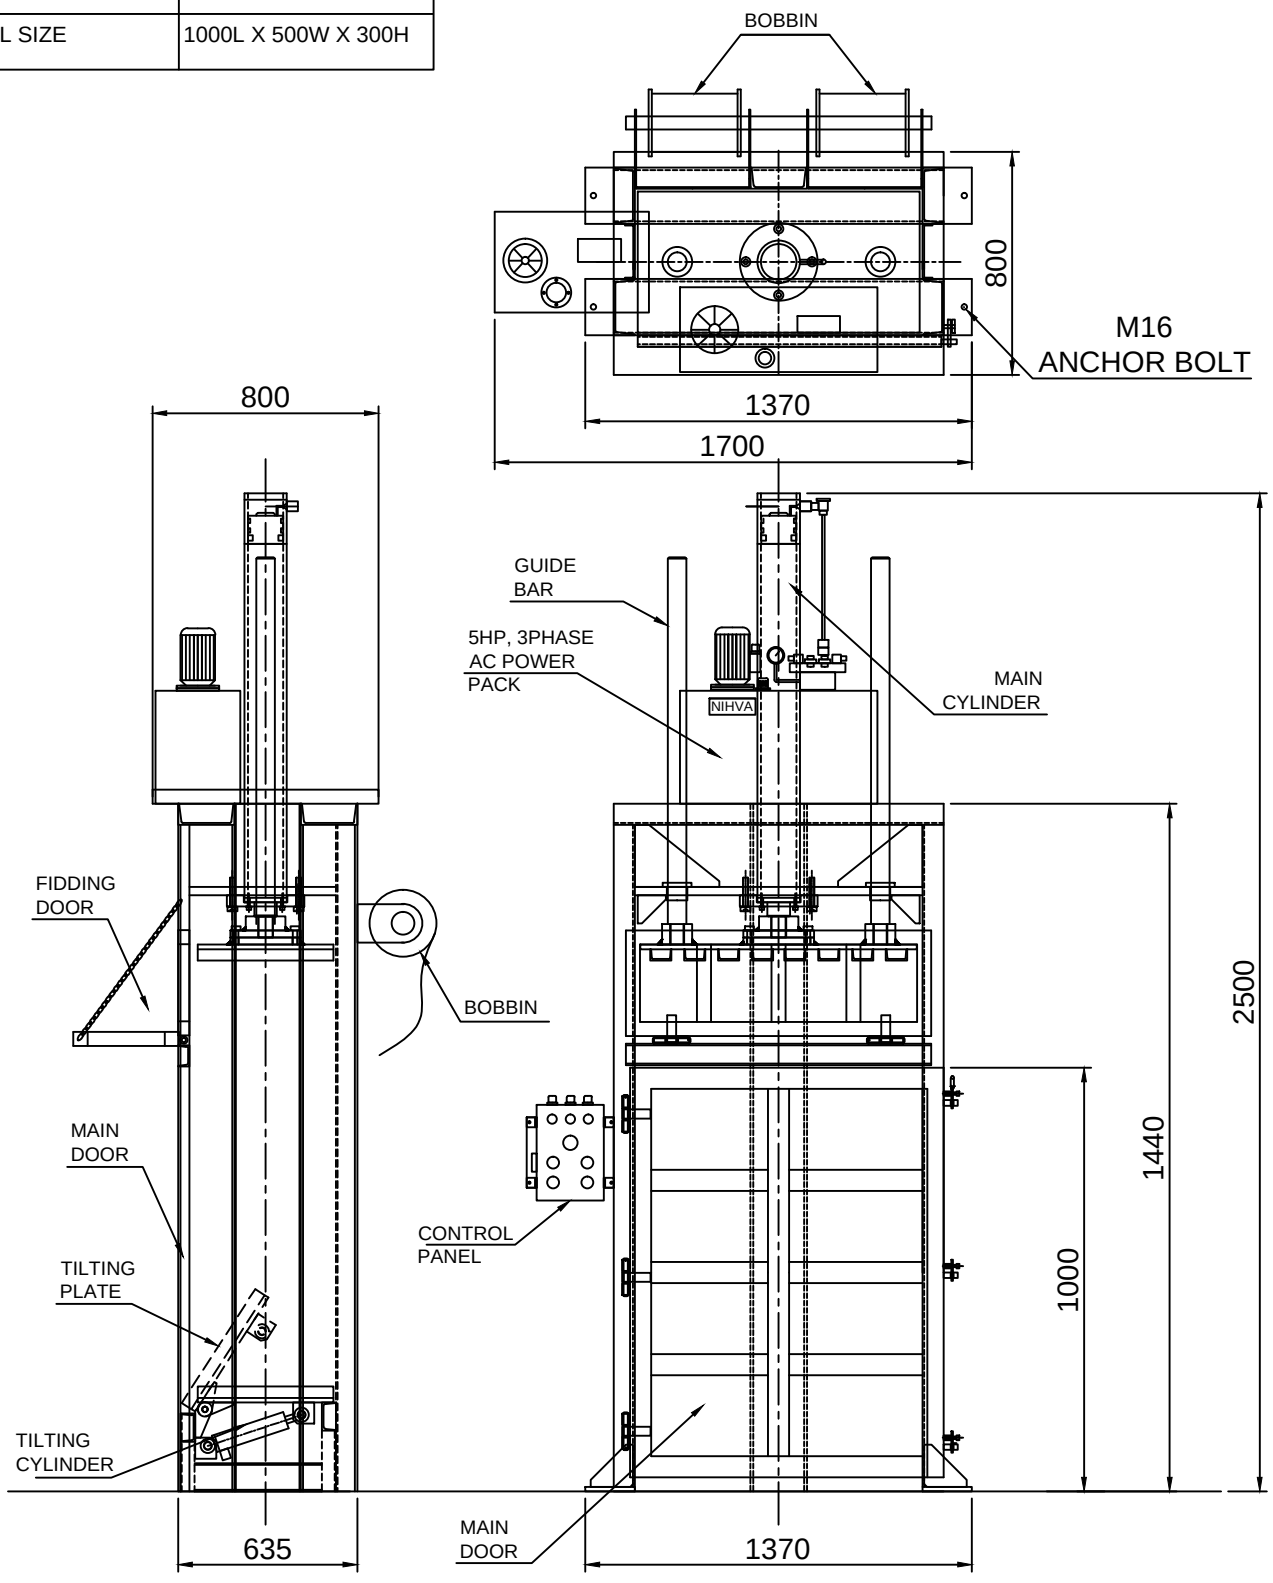

REV NO	REV DATE	DRAWN	REMARK
R02	05.10.2019	P.V.A	1. POWER PACK LOCATION CHANGE
R01	01.10.2019	P.V.A	1. POWER PACK LOCATION CHANGE 2. CHAMBER SIZE CHANGE

This drawing & design is the property of NIHVA TECHNOLOGIES. Not to be sold or copied to any other concern.

TITLE: BAILING PRESS

	NAME	SIGN	DATE
DRAWN	P.A		18.09.2019
CHECK	G.J		18.09.2019
APPRD.			

NIHVA TECHNOLOGIES PVT. LTD.
NIHVA TECHNOLOGIES PVT. LTD. PUNE
Tel : 020 66304033
Email:- info@nihva.com
Website:- www.nihva.com

CLIENT - IKEA

PROJECT -

SITE LOCATION -

If any queries contact : design@nihva.com

DWG. NO. :NIHVA/1 9-20/0096/R02 REV- R02

ALL DIMENSION ARE IN mm

SCALE: NTS WT: SHEET: 01 OF 01