


PEB structure with framing

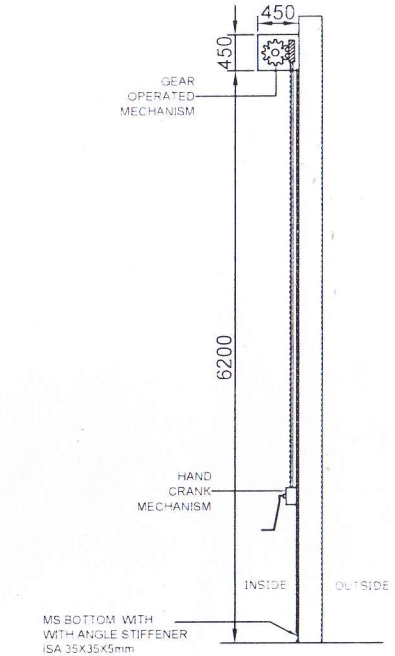

SIDE VIEW

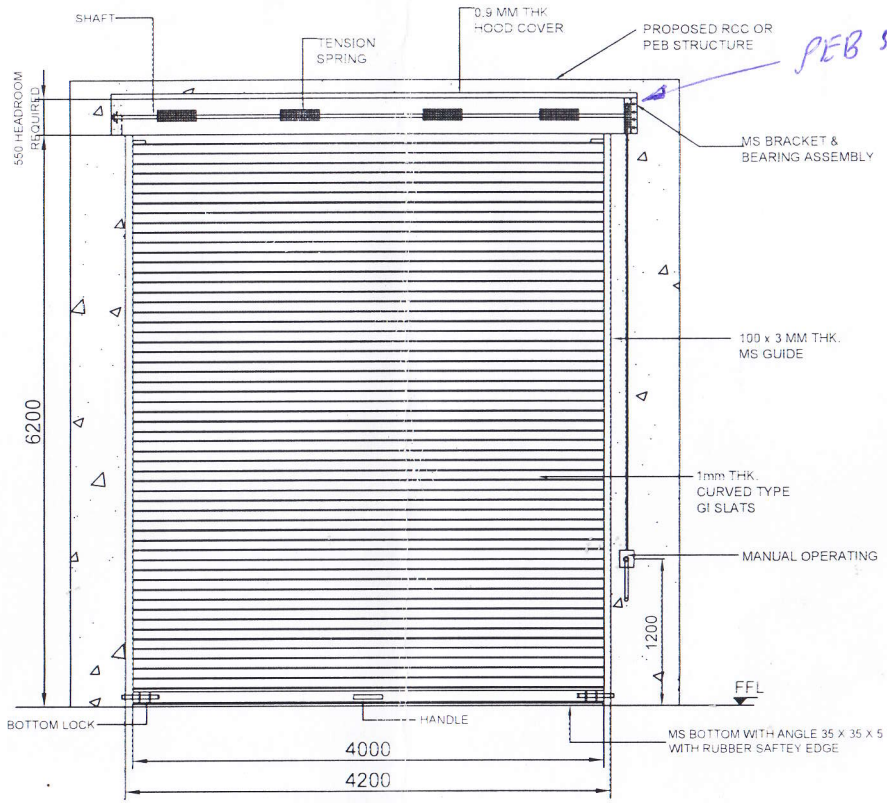

INSIDE ELEVATION

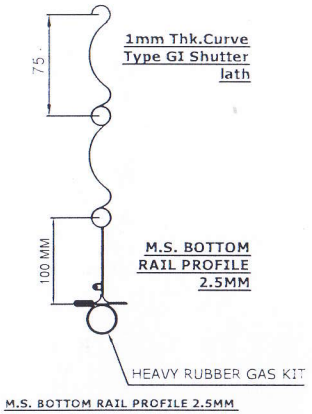


M.S. BOTTOM RAIL PROFILE 2.5MM


Dwg Read on 13/11/18

Approved

(S. Prasad)
13/11/18

(All other specifications to be as per LNO.)

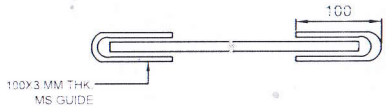

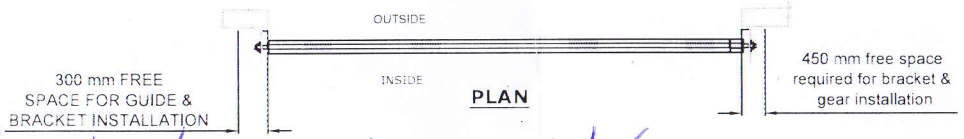

PLAN

NOTE :- Delivery & Installation to be Completed by 20/11/2018

TOLERANCE - ±10mm

S.N.	LOCATION	SIZE	QUANTITY
1	B600	4000(W)X6200(H)	01

NOTE-
1. ALL CIVIL WORK WILL BE CLIENT'S SCOPE.
2. STRUCTURE REQUIRED FOR SHUTTER IS IN CLIENT'S SCOPE.
3. FINAL FINISH OF SHUTTER WILL BE IN POWDER COATING OF APPROVED COLOR i.e.RAL 7001
4. DESIGN OF SHUTTER IS AS PER I.S. 6248 1979 STANDARDS.

Sumit P. Jungade
13-11-18

TITLE	GEAR OPERATED ROLLING SHUTTER 4mX6.2m With Right side gearbox		
	NAME	SIGN	DATE
DRAWN	P.A		27.10.2018
CHECK	R.D		27.10.2018
APPRD.	V.T		27.10.2018

ALL DIMENSION ARE IN mm

NIHVA TECHNOLOGIES PVT. LTD. PUNE
Tel : 020 66304033
Email:- info@nihva.com
Website - www.nihva.com

CLIENT - INDOSPACE
PROJECT - BUILDING B600
SITE LOCATION - CHAKAN
DWG. NO. : NIHVA/18-19/0163 | REV- 0
SCALE NTS | WT: | SHEET: 01 OF 01

For any queries contact design@nihva.com