LATEST ARCH. DWG : MP-A-5009-A
LAST MODIFIED : 05-08-2024

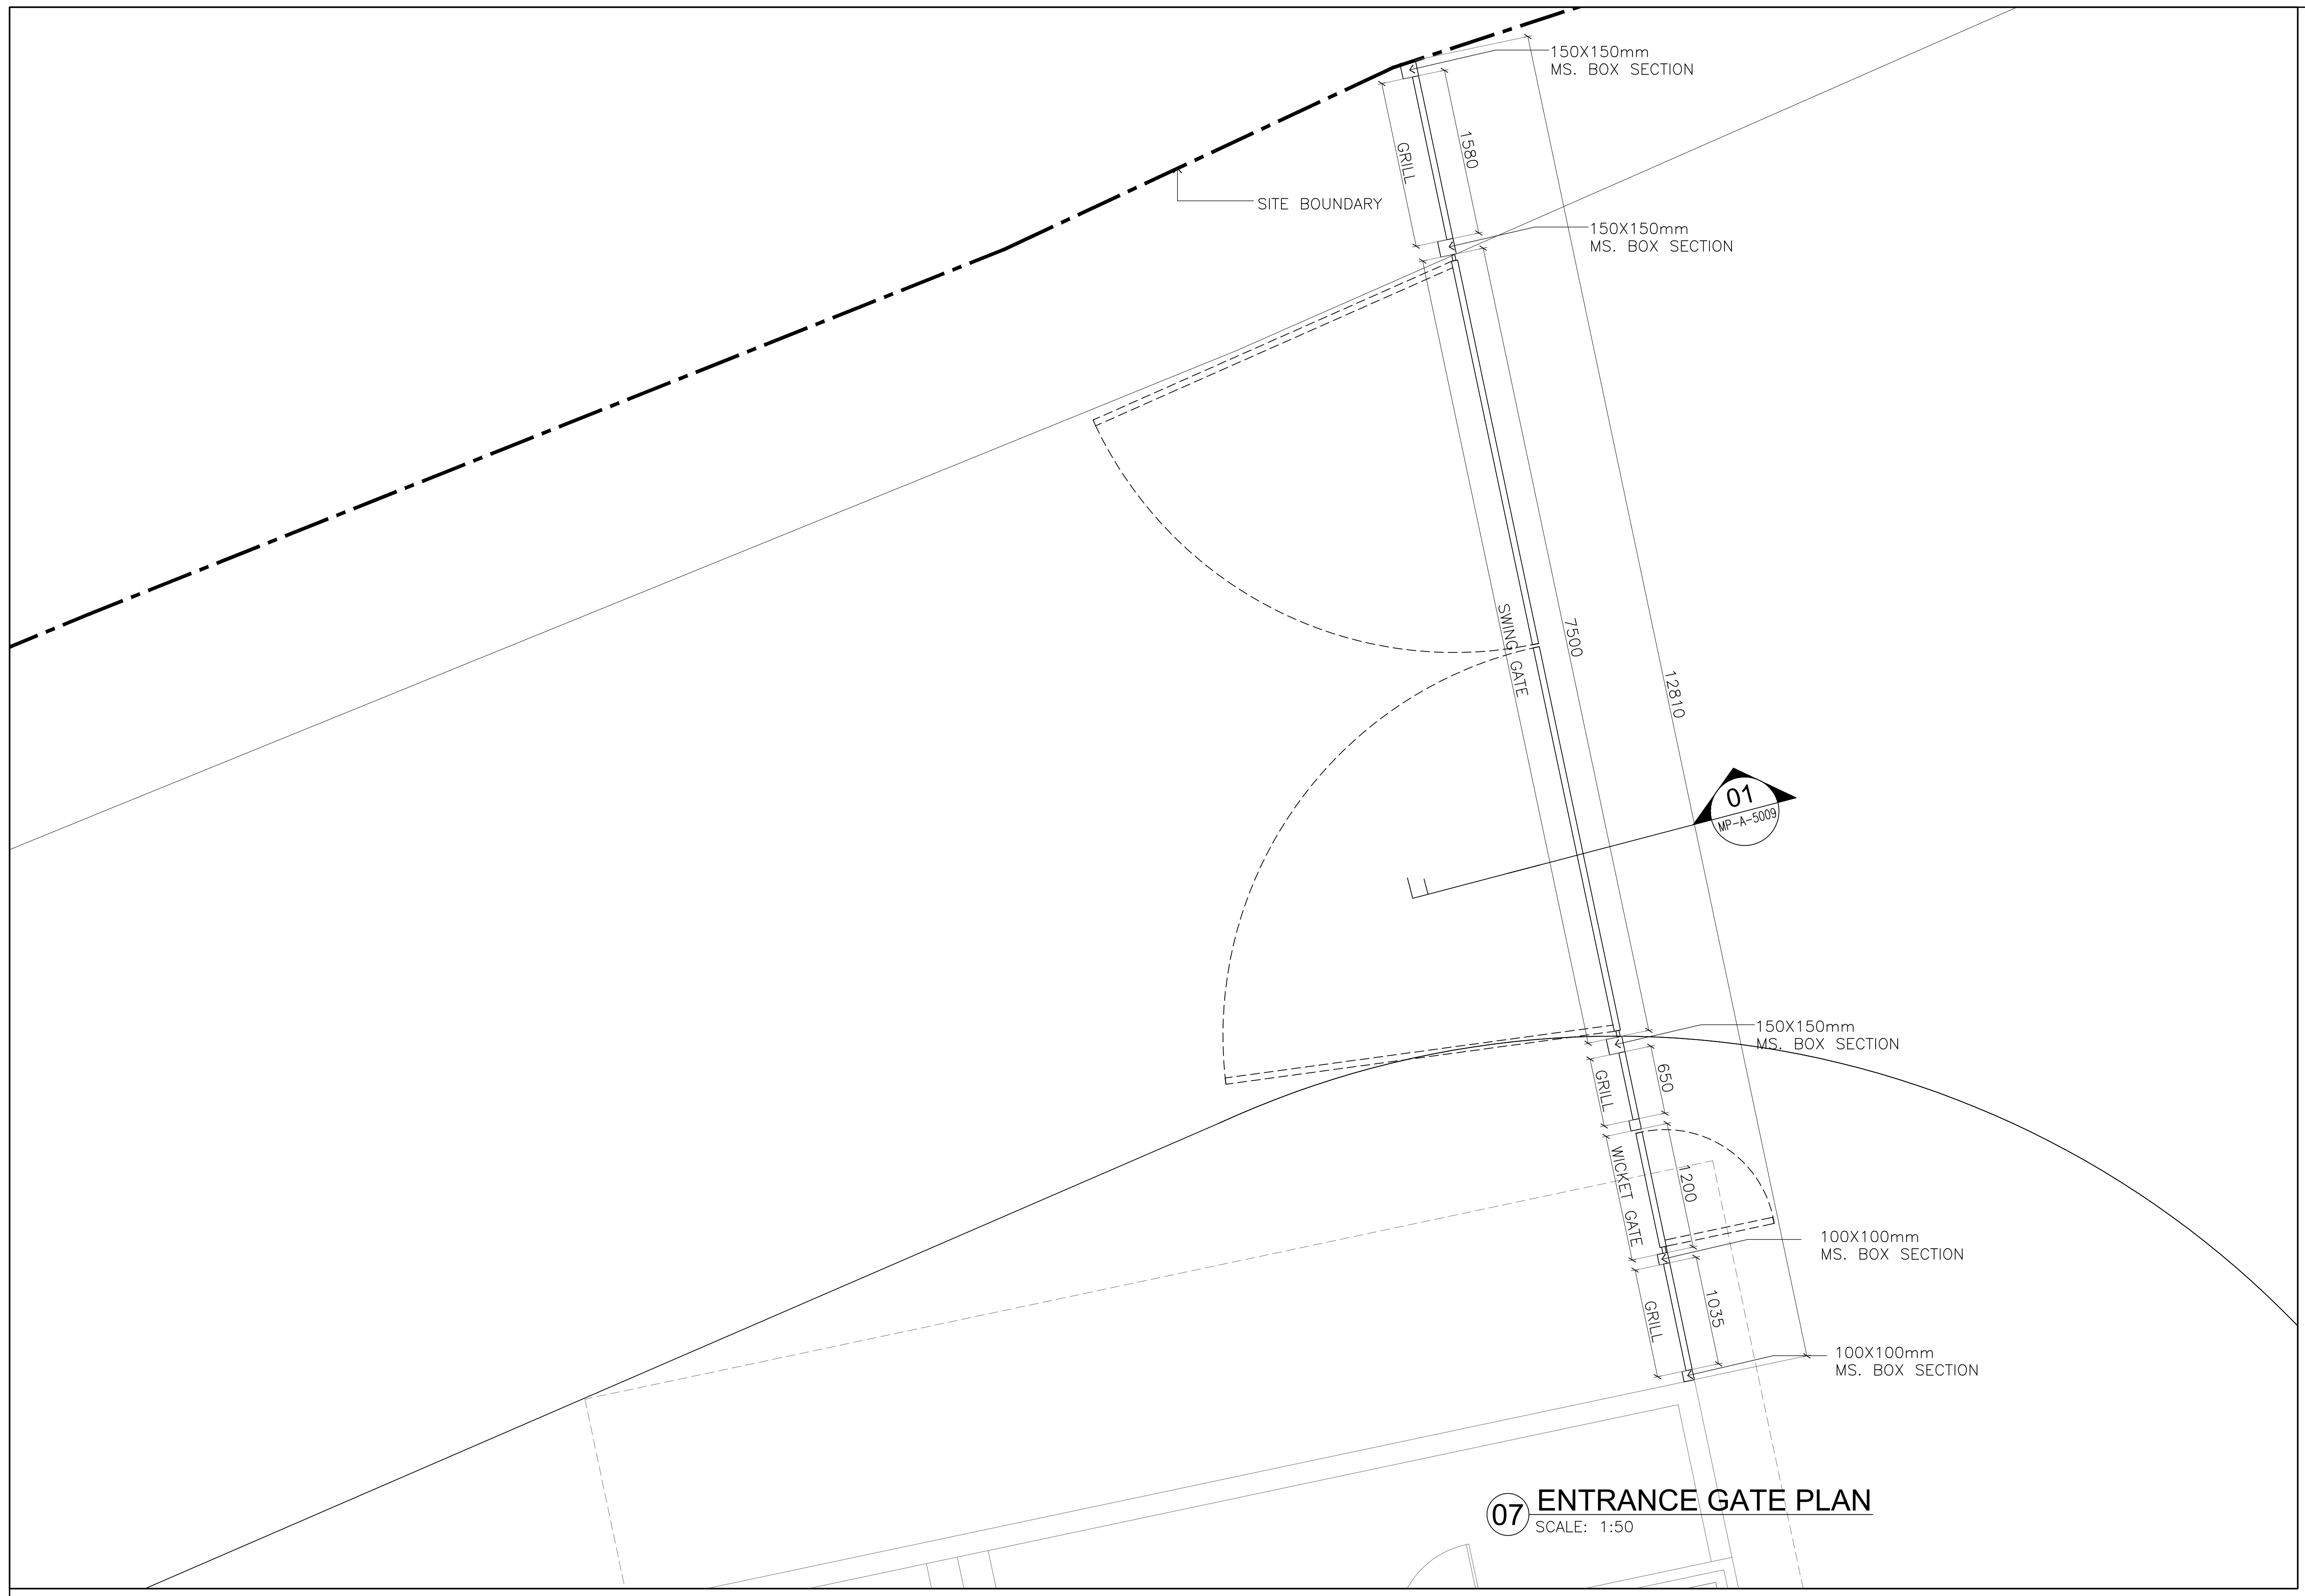

07 ENTRANCE GATE PLAN
SCALE: 1:50

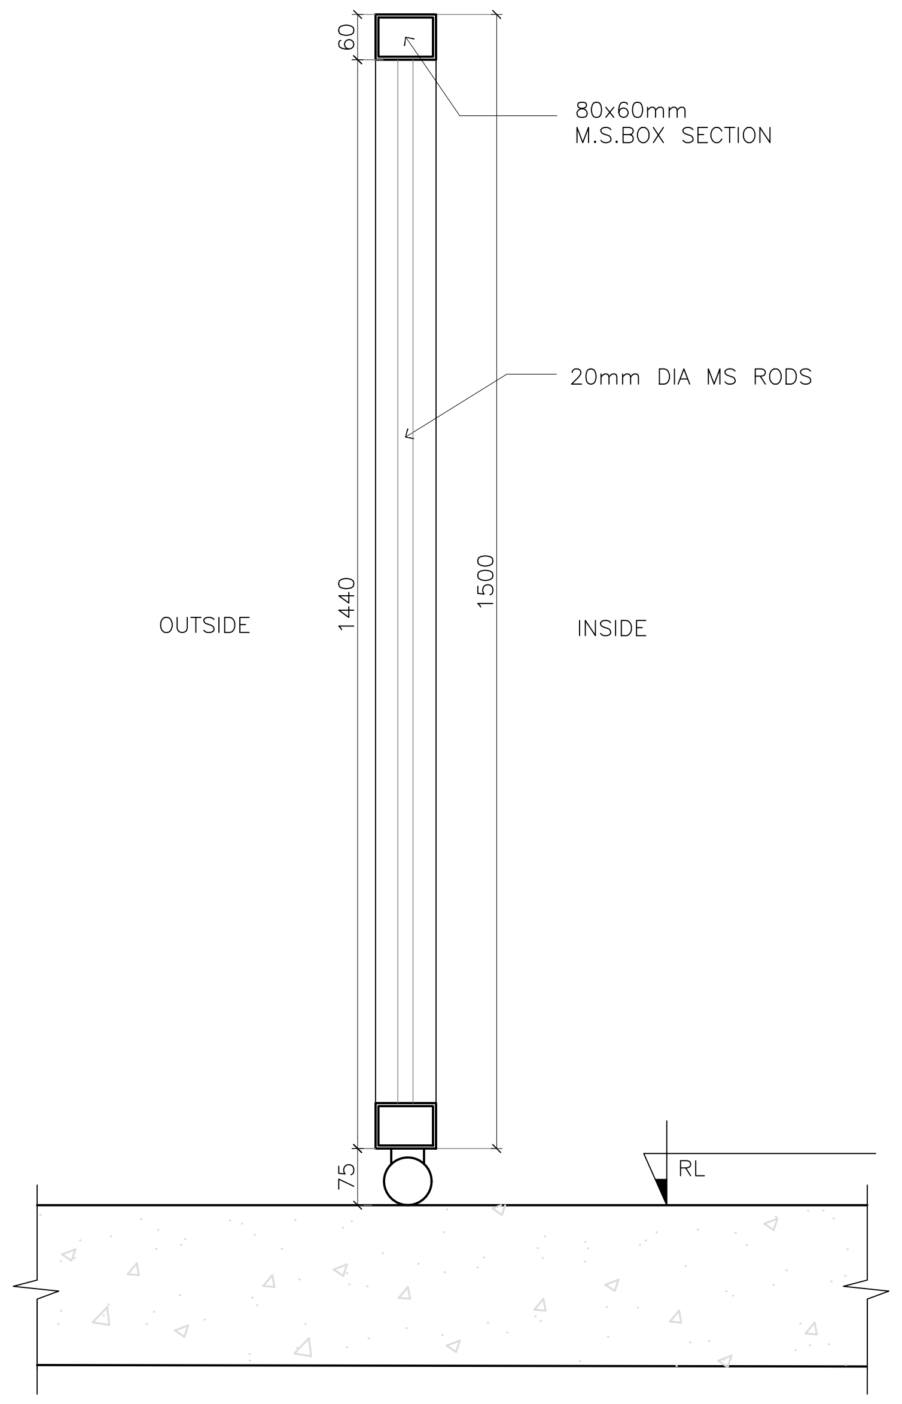

03 SECTION-1
SCALE: 1:10

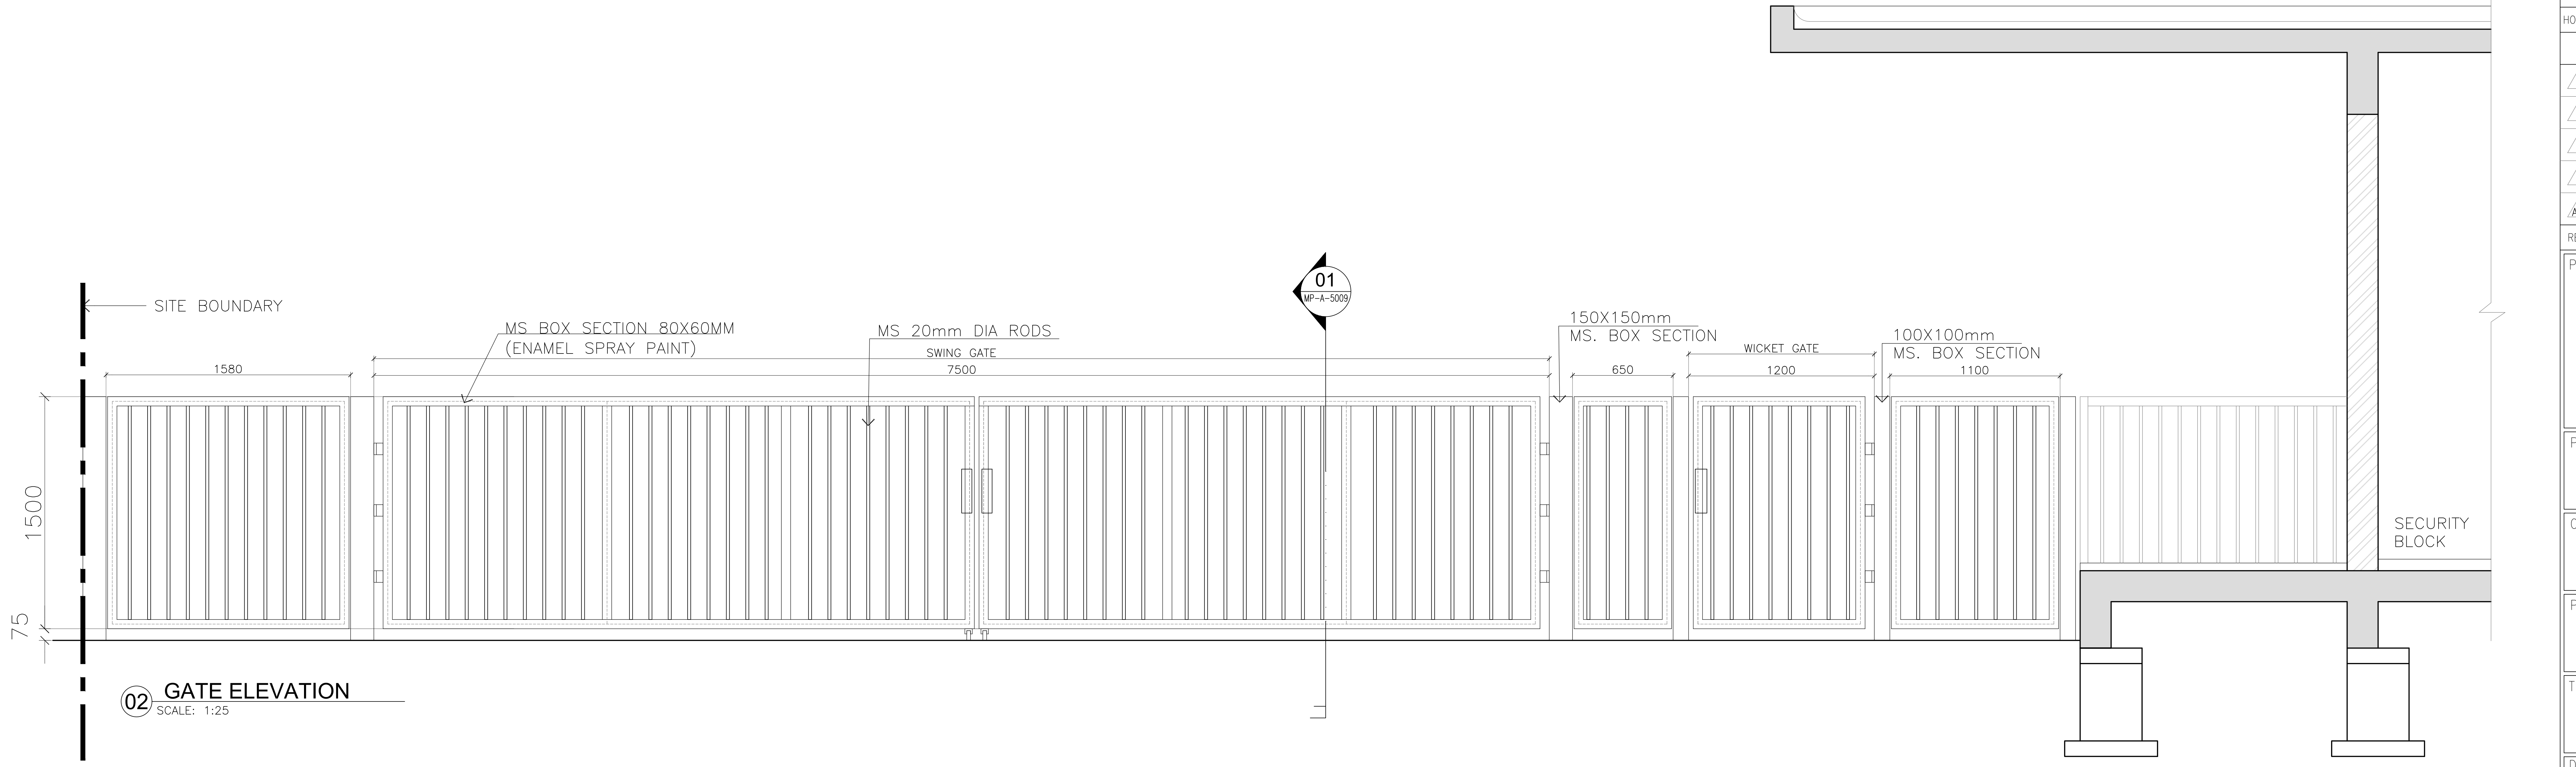

02 GATE ELEVATION
SCALE: 1:25

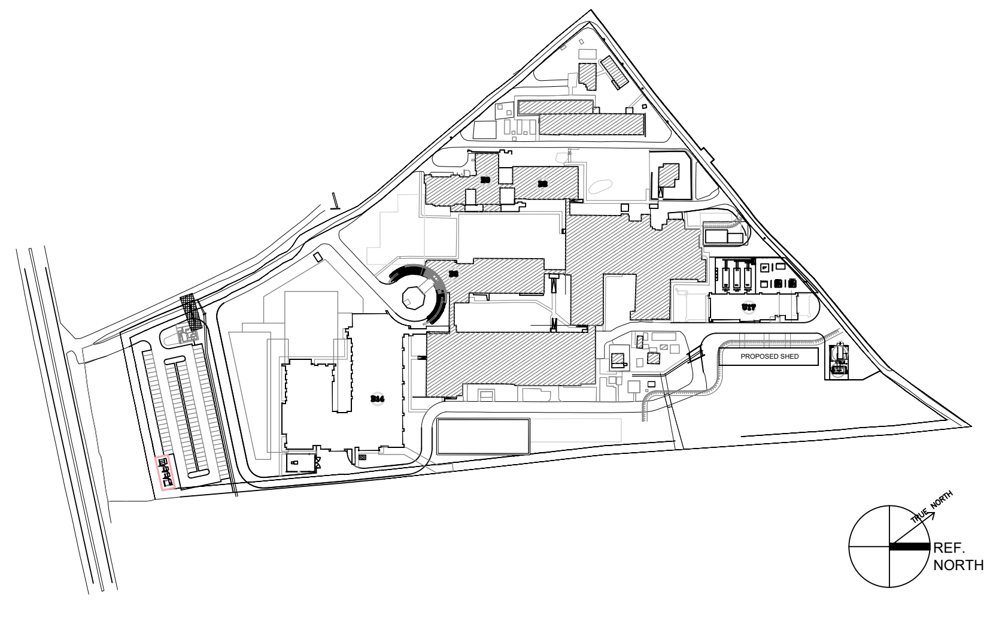

△			
△			
HOLD.NO.	DATE	REASON FOR HOLD	SIGNED BY

△				
△				
△				
△				
A	05-08-2024	FOR TENDER	SULEKHA	HARSHINI
REV.NO.	DATE	DESCRIPTION FOR REVISION	DRAWN BY	CHECKED BY

PURPOSE:VA

FOR TENDER

PROJECT MANAGERS

OWNER
syngenta
Syngenta Research and Technology Centre – Goa

PROJECT
PRAGATI

TITLE
MASTER PLAN
ENTRY GATE DETAILS

DEALT SHEKAR	JOB NO 074.05.07.22	REVISION A
SCALE AS MENTIONED	DATE 02-08-2024	DRAWING NO MP-A-5009

Venkataramanan
Associates
ARCHITECTURE
INTERIOR DESIGN
URBANISM
10/2, O'Shaughnessy Road, Langford Gardens, Bengaluru - 560025 India | www.vagroup.com

1. Maintain a register of drawing receipts,listing drawing & revision number,title,from whom received,date received,number of copies received,details of transmittal from the issuer & any other relevant details to be advised from time to time.
2. Archive all previous revision issues immediately upon receipt of a new revision and no superseded drawing shall remain in the site of works except in the contractor's archives for record and reference purpose only.
3. While archiving superseded drawing,the contractor is expected to stamp all previously issued drawing/prints appropriately,mentioning the date and revision number of the new revision on account of which the previous revision is archived.
4. The contractor shall allow the representative of Client/PMC/Architect to inspect contractor's archives for ensuring compliance.
5. Any work carried out by the contractor using a superseded drawing after the issue of a new revision is liable for rejection and reinstatement as per new revision at contractor's risk and cost without any entitlement to extension of time.