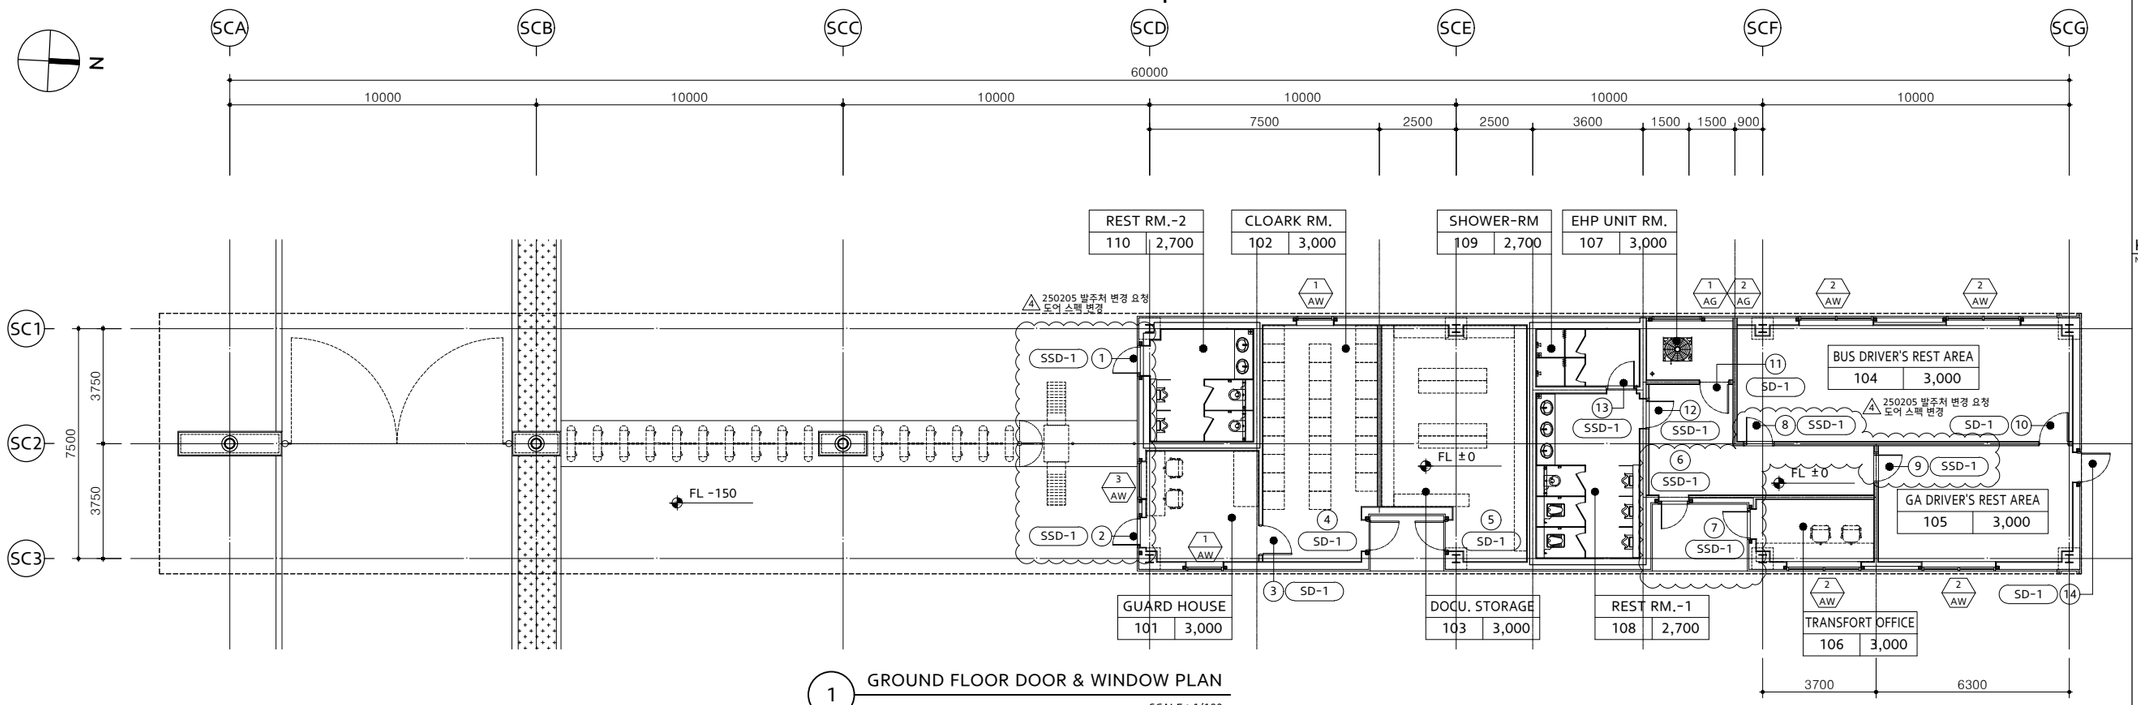



1 GROUND FLOOR DOOR & WINDOW PLAN

SCALE : 1/100

KEY PLAN

NOTE

1. IF APPLICABLE TO EXISITING DOORS, WINDOWS CONSTRUCTION SHALL BE CARRIED OUT CLIENT'S, CONTRACTOR'S APPROVAL.
2. VARIOUS OPENINGS MUST BE DETERMINED IN ADVANCE BY SHOP DWG OF THE RELEVANT WORK TYPE
3. PROVIDE 15mm GAP BETWEEN INSIDE FACE OF STEEL FRAMING AND CLEAR OPENINGS.

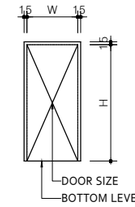


DOOR SHAPE & LEGEND

1	GENERAL NOTE



2	DOOR & WINDOW TYPE				
SD	STEEL DOOR		OHD	OVERHEAD DOOR	
FSD	FIRE STEEL DOOR		RS	ROOL-UP SHUTTER	
SSD	S' STEEL DOOR		RRS	RAPID ROOL-UP SHUTTER	
SFD	S' STEEL FOLDING DOOR		AW	ALUMINUM WINDOW	
ASD	AUTO SLIDING DOOR		SSW	S' STEEL WINDOW	
SLID	SLID DOOR		AG	ALUMINUM GRILL	

3	DOOR SHAPE : SINGLE DOOR

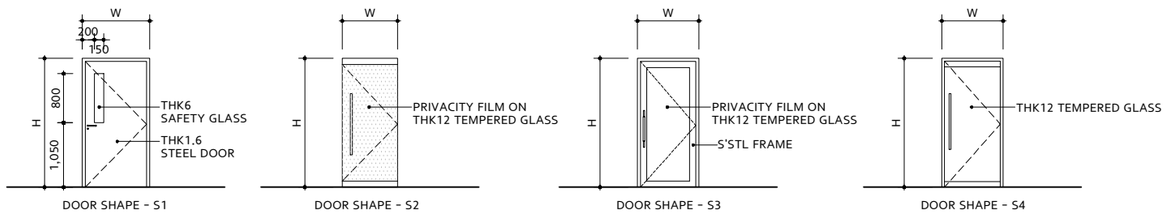


DOOR SCHEDULE


FLOOR NO.	NO.	DOOR NO. △4 250205 발주처 요청사항 도어 스펙 변경	MATERIAL		DOOR SIZE			SHAPE	MATERIAL			FIRE	KEY SET	HW SET	REMARKS
			DOOR	FRAME	THK	WIDTH	HEIGHT		HEAD	JAMB	SILL				
1F	1	SSD-1	GLASS	S'STL	45	1,000	2,100	S3	-	-	-	-	-	521	△4 250205 발주처 요청사항 도어 스펙 변경
	2	SSD-1	GLASS	S'STL	45	1,000	2,100	S3	-	-	-	-	-	521	
	3	SD-1	STL	STL	45	1,000	2,100	S1	-	-	-	-	-	110	
	4	SD-1	STL	STL	45	1,000	2,100	S1	-	-	-	-	-	110	
	5	SD-1	STL	STL	45	1,000	2,100	S1	-	-	-	-	-	110	△4 250205 발주처 요청사항 도어 스펙 변경
	6	SSD-1	GLASS	S'STL	45	1,000	2,100	S3	-	-	-	-	-	521	
	7	SSD-1	GLASS	S'STL	45	1,000	2,100	S3	-	-	-	-	-	521	
	8	SSD-1	GLASS	S'STL	45	1,000	2,100	S4	-	-	-	-	-	516	
	9	SSD-1	GLASS	S'STL	45	1,000	2,100	S4	-	-	-	-	-	516	
	10	SD-1	STL	STL	45	1,000	2,100	S1	-	-	-	-	-	110	
	11	SD-1	STL	STL	45	1,000	2,100	S1	-	-	-	-	-	110	
	12	SSD-1	GLASS	S'STL	45	1,000	2,100	S2	-	-	-	-	-	501	
	13	SSD-1	GLASS	S'STL	45	1,000	2,100	S2	-	-	-	-	-	501	
	14	SD-1	STL	STL	45	1,000	2,100	S1	-	-	-	-	-	110	

WINDOW SCHEDULE


△4 250205 발주처 요청사항 도어 스펙 변경

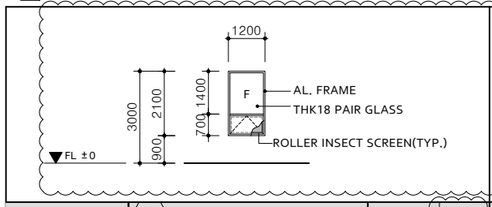


ID	1 AW	ALUMINUM WINDOW	QT'Y	2 EA
GLAZING	THK18 PAIR GLASS			
FRAME	AL,BAR / ELECTROSTATIC POWDER COATING			
HARDWARE	-			

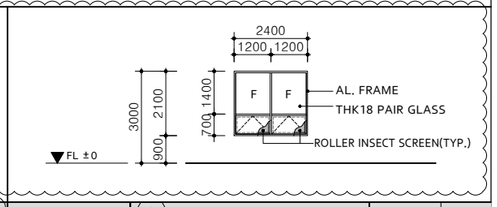


ID	2 AW	ALUMINUM WINDOW	QT'Y	4 EA
GLAZING	THK18 PAIR GLASS			
FRAME	AL,BAR / ELECTROSTATIC POWDER COATING			
HARDWARE	-			

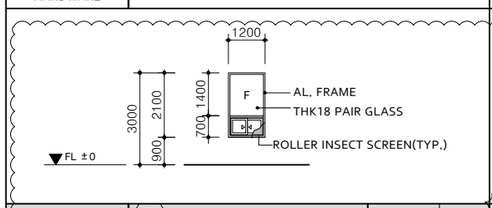

ID	3 AW	ALUMINUM WINDOW	QT'Y	1 EA
GLAZING	THK18 PAIR GLASS			
FRAME	AL,BAR / ELECTROSTATIC POWDER COATING			
HARDWARE	-			

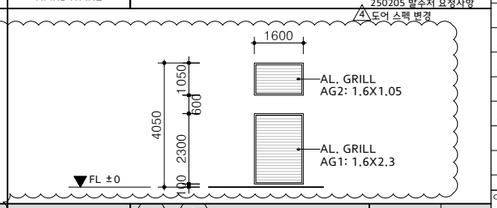

ID	1 AG	2 AG	QT'Y	2 EA
GLAZING	-			
FRAME	AL,BAR / ELECTROSTATIC POWDER COATING			
HARDWARE	-			

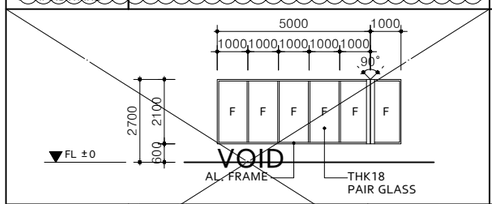

ID	3 AW	ALUMINUM WINDOW	QT'Y	1 EA
GLAZING	THK18 PAIR GLASS			
FRAME	AL,BAR / ELECTROSTATIC POWDER COATING			
HARDWARE	-			

REV.	DESCRIPTION	DRAWN	DATE
4	CD Rev.4	OH,J.S	2025.02.14
3	CD Rev.3	OH,J.S	2025.01.08
2	CD Rev.2	OH,J.S	2024.11.29
1	CD Rev.1	OH,J.S	2024.10.18
0	CONSTRUCTION DRAWING	OH,J.S	2024.07.30
B	DD Rev.B	OH,J.S	2024.06.28
A	DESIGN DEVELOPMENT	OH,J.S	2024.04.15

CLIENT: HYUNDAI

ARCHITECTS & ENGINEERS: JUNGLIM ARCHITECTURE

PROJECT TITLE: PUNE HMI PROJECT

DRAWING TITLE: [SUB SECURITY OFFICE] DOOR, WINDOW PLAN & SCHEDULE

SCALE	DRAWN	CHECKED	REVIEWED	APPROVED	APPROVED
A1:1/100 A3:1/200	OH,J.S	HONG,G.D	LEE,S.L	HEC INDIA	PARK,T.S
DATE: 14 FEB,2025					

MAIN CONTRACTOR: HEC KOREA LLP

DRAWING NO.: WA-IPB-646-A-6101 REV.: 4

A1 SIZE (841mm x 594mm)