



SIDE VIEW

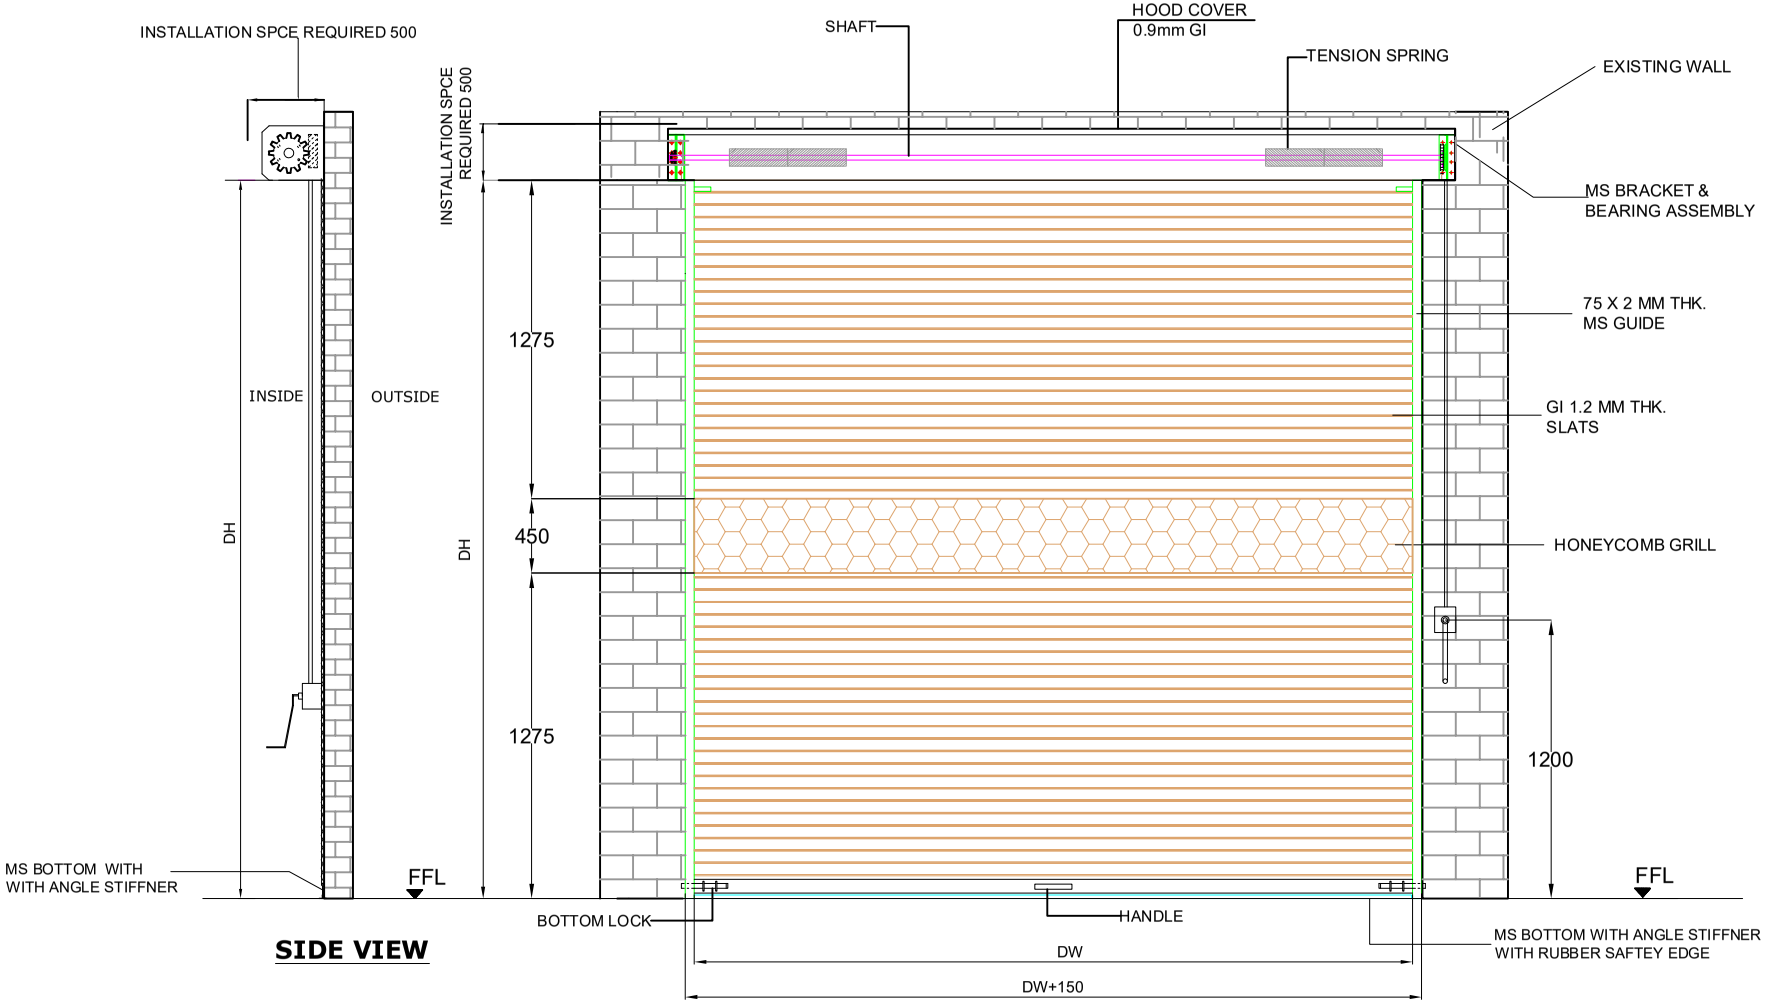


Curve Type MS Shutter SLATS

M.S. BOTTOM RAIL PROFILE 2MM

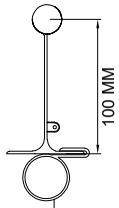

HEAVY RUBBER GAS KIT



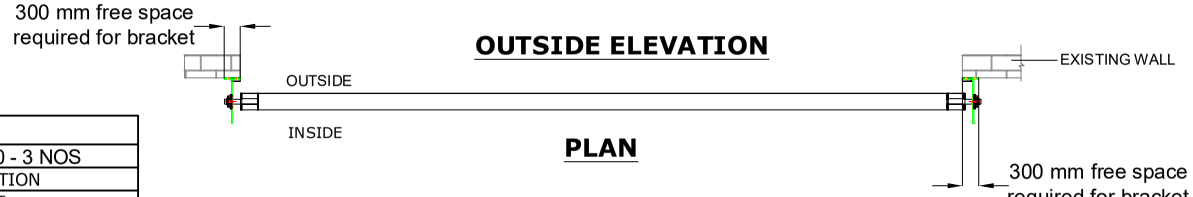

OUTSIDE ELEVATION

PLAN

	TECHNICAL SPECIFICATIONS	
	SHUTTER SIZE - DW 3000 x DH 3000 - 3 NOS	
SR NO	DESCRIPTION	SPECIFICATION
1.	SOLID SLAT & QTY	1.2 mm THK GI. SLAT
2.	M.S.GUIDE TYPE & SIZE	U GUIDE OF 75X35X2 THK
3.	HOOD COVER 0.9 mm GI	1/SHUTTER
4.	BOTTOM	MS BOTTOM 2 mm THK WITH ANGLE STIFFNER WITH RUBBER SAFTEY EDGE
5.	WIND LOCK	NOT CONSIDERED
6.	SAFETY BREAK	NOT APPLICABLE
7.	HAND CRANK	CONSIDERED
8.	CHAIN	NOT APPLICABLE
9.	HAND CRANK	RH SIDE
10.	SHUTTER MTG LOCATION	INSIDE
11.	SHUTTER MOUNTING BASE	RCC WALL (IN CLIENT SCOPE)
12.	APPROVED RAL SHADE	AS CLIENT APPROVED RAL

RAL CODE	SHADE	COLOUR
RAL 5002	ULTRAMARINE BLUE	
RAL 7035	LIGHT GREY	
RAL 7001	SILVER GREY	

NOTE:-

1. ALL CIVIL WORK WILL BE IN CLIENT SCOPE.
2. SURFACE FINISH: POWDER COATING OF APPROVED RAL.
3. MOUNTING: RCC WALL

TOLERANCE - ±10mm

CLEAR WIDTH (DW)	CLEAR HEIGHT (DH)	QTY
3000	3000	3NOS

REV.NO	REVISION	DATE	REVISED BY

This drawing & designing is the property of NIHVA TECHNOLOGIES. Not to be sold or copied to any other concern.

TITLE :-
GEAR OPERATED ROLLING SHUTTER

NIHVA TECHNOLOGIES PVT. LTD.

	NAME	DATE
DRAWN	SUJATA	30/06/2023
CHECK		
APPROVAL		

CLIENT - SHREE PRE FAB STEEL PVT LTD
PROJECT -
SITE -GUJARAT
DWG. NO. : NIHVA/23-24/CLT/0142 REV-00
If any queries contact : design1@nihva.com
SCALE: NTS WT: SHEET: 01 OF 01
ALL DIMENSION ARE IN mm