




ELEVATION

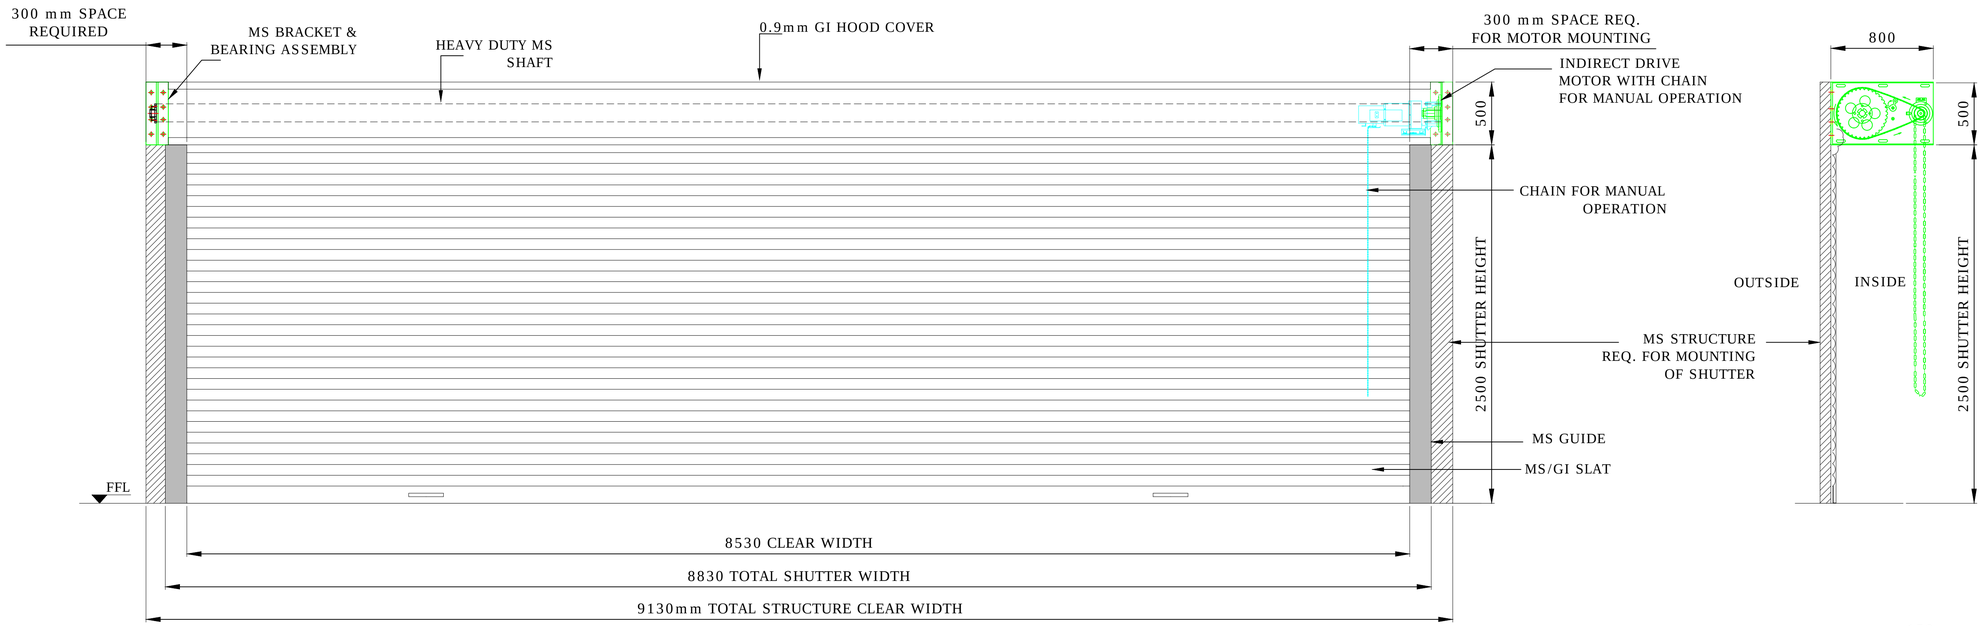




PLAN

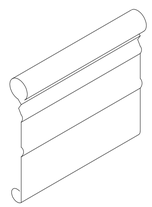

SLAT PROFILE

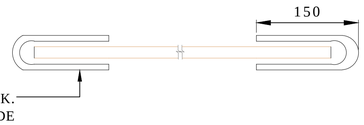


| DIMENSION : | | |
|---|---|---|
| CLEAR WIDTH | CLEAR HEIGHT | QUANTITY |
| 8530 | 2500 | 1 |

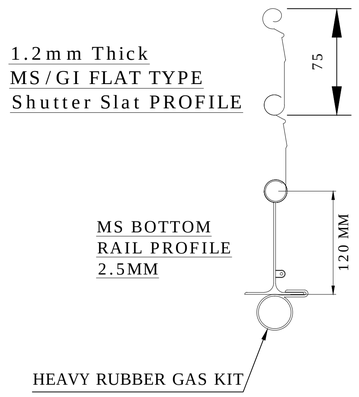MATERIAL :

THICKNESS :

NOTE-
1.ONE COAT OF RED OXIDE WILL BE GIVEN TO SHUTTER (ONLY MS PART). PAINT OF APPROVED RAL SHADE WILL BE GIVEN TO THE SHUTTER.
2. HOOD COVER WILL BE IN GI.
3.THREE PHASE SUPPLY SHOULD BE GIVEN TO THE SHUTTER.
4. REQUIRED STRUCTURE FOR SHUTTER SHALL BE IN CLIENT'S SCOPE.
5. ALL CIVIL WORK WILL BE IN CLIENT'S SCOPE.
6. TOLERANCE FOR GRILL SIZE SHALL BE PLUS/MINUS 15mm

NIHVA TECHNOLOGIES PVT. LTD.
NIHVA TECHNOLOGIES PVT. LTD. PUNE
Email:- info@nihva.com
Website:- www.nihva.com

TITLE:

# MOTORIZED ROLLING SHUTTER

CLIENT'S APPROVAL :

| | | |
|---|---|---|
| CLIENT - JLL | | |
| PROJECT - INORBIT MALL | | |
| SITE LOCATION - WADGAONSHERI,PUNE | | |
| DWG. NO. :NIHVA/17-18/VDR/0084 | | |
| SCALE: NTS | WT: | SHEET:1 OF 1 |
| DRAWN BY: OMKAR | | DATE: 03-08-2017 |
| CHECK : SHEKHAR | | DATE: 03-08-2017 |
| APPROVED : SHEKHAR | | DATE: 03-08-2017 |

If any queries contact : projects@nihva.com

NOTE: ALL DIMENSIONS ARE IN mm

THIS DRAWING & DESIGN IS THE PROPERTY OF NIHVA TECHNOLOGIES. NOT TO BE SOLD OR COPY TO ANY OTHER CONCERN.