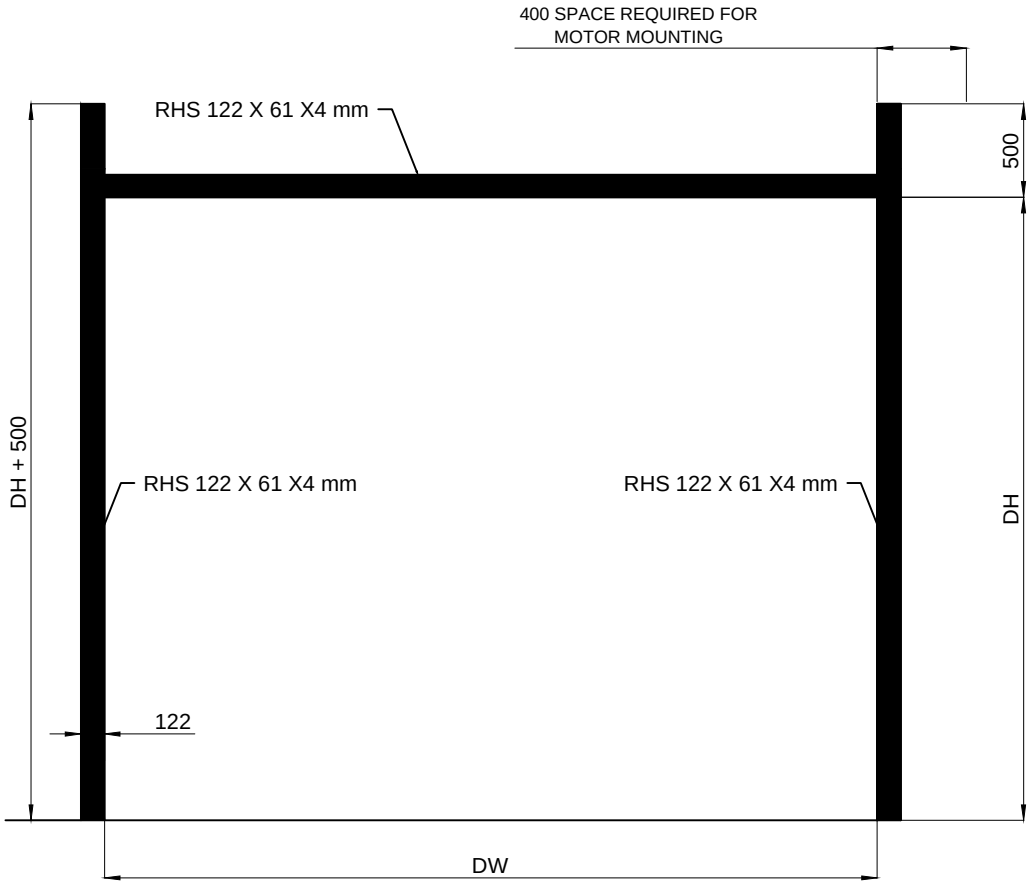

STRUCTURE FOR HSD

5000	3000	04 NOS
4000	3300	04 NOS
3500	3620	02 NOS
CLEAR WIDTH(DW)	CLEAR HEIGHT(DH)	QUANTITY

NOTE -
1.STRUTURE REQUIRED FOR HSD IS IN CLIENT'S SCOPE.
2.RAL CODE - 7035 - LIGHT GRAY FOR M.S STRUCTURE.

This drawing & design is the property of NIHVA TECHNOLOGIES. Not to be sold or copied to any other concern.

TITLE	HIGH SPEED DOOR RP300 & STRUCTURE			NIHVA TECHNOLOGIES PVT. LTD. PUNE
	NAME	SIGN	DATE	Tel : 020 66304033 Email:- info@nihva.com Website:- www.nihva.com
DRAWN	P.A		05.11.19	CLIENT :- WOOSHIN
CHECK	G.J		05.11.19	PROJECT :-
APPV'ED				LOCATION :- PUNE
If any queries contact : design@nihva.com				DWG. NO. :- NIHVA/19-20/0147 REV.:- 00
ALL DIMENSION ARE IN mm				SCALE: NTS WT: SHEET: 01 OF 01