
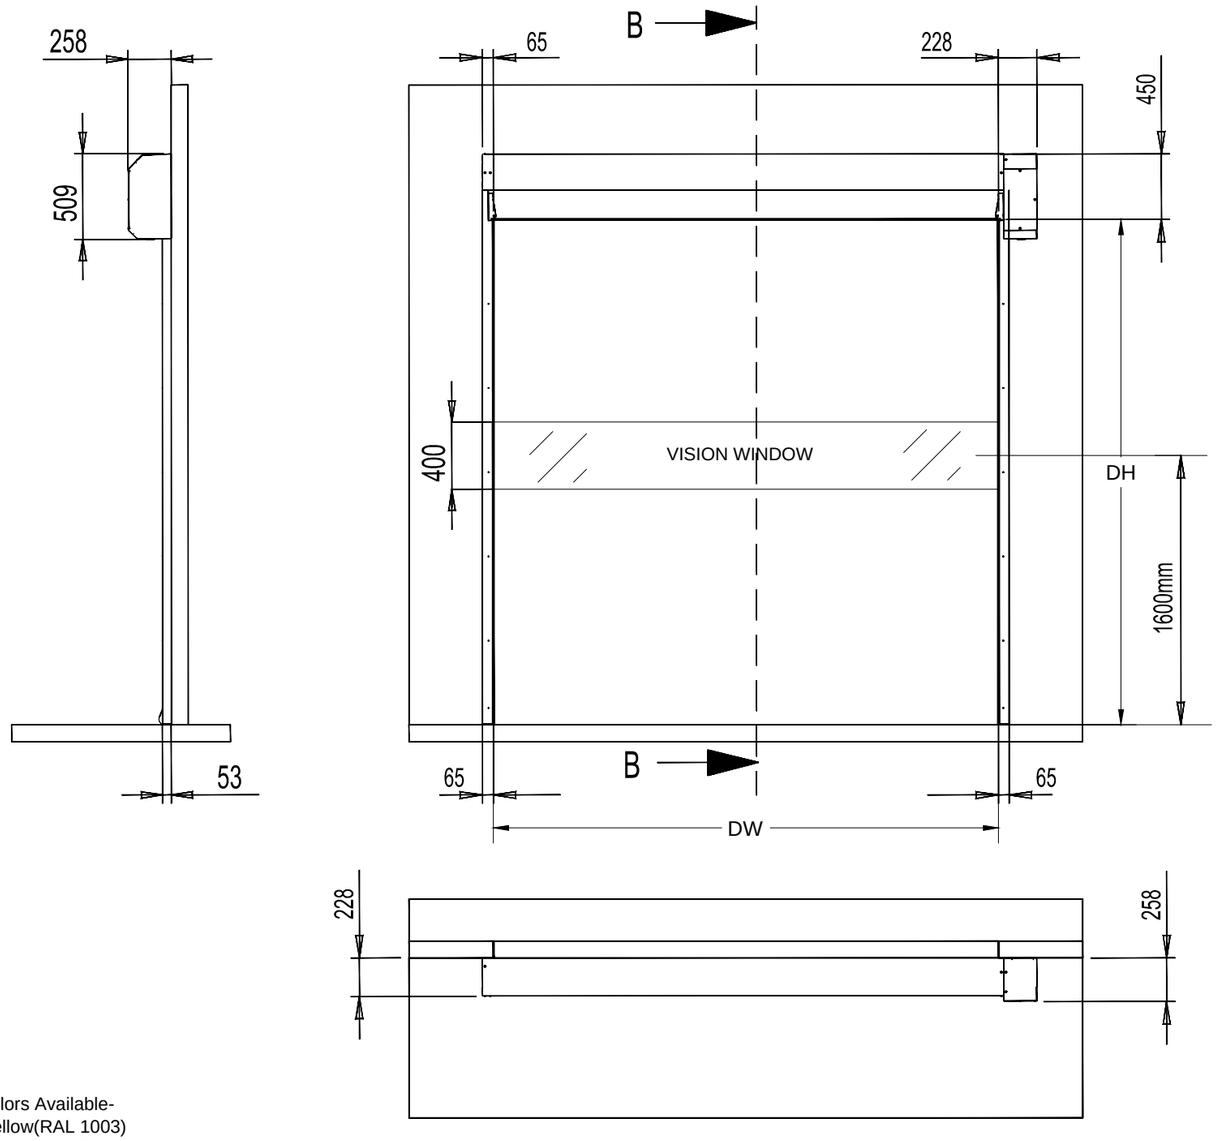


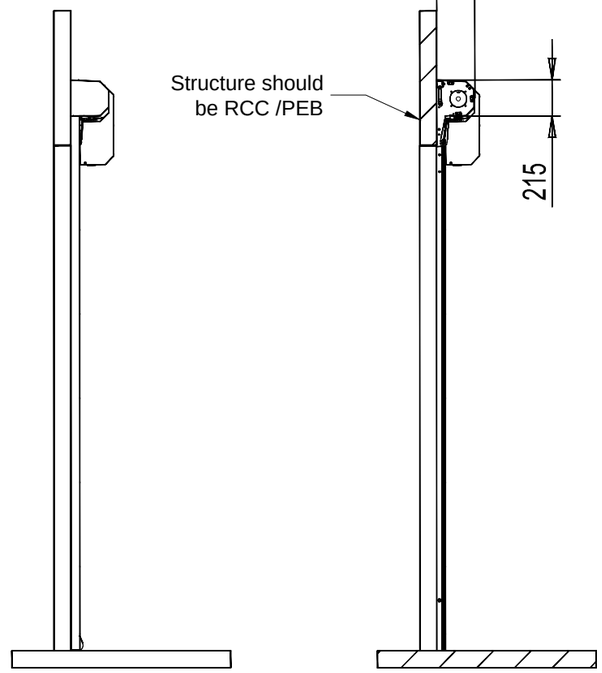

SECTION B-B

Curtain Colors Available-
1.Signal yellow(RAL 1003)
2.Flame Red (RAL 3000)
3.Moss Green (RAL 6005)
4.Jet Black (RAL 9005)
5.Pure orange (RAL 2004)
6. Ultramarine Blue(RAL 5002)
7. Light Grey (RAL 7035)
8. White (RAL 9010)

Note-
1. All Civil work will be in clients scope.
2. Client has to choose color for door curtain or else standard color will be considered as Grey RAL7035.
3. Client has to choose motor side (Right/left) according to the site conditions. Standard door comes with Right side Motor mounting.

DOOR DIMENSION				
SR NO	DW	DH	MOTOR LOCATION	QUANTITY
1	2500	2500	RIGHT HAND SIDE	03
2	3000	3000	RIGHT HAND SIDE	01

This drawing & designing is the property of NIHVA TECHNOLOGIES. Not to be sold or copied to any other concern.

TITLE: HIGH SPEED DOOR HS9020G

NIHVA TECHNOLOGIES PVT. LTD.

NIHVA TECHNOLOGIES PVT. LTD. PUNE
Tel : 020 66304033
Email:- info@nihva.com
Website:- www.nihva.com

	NAME	SIGN	DATE
DRAWN	OMKAR		28/03/18
CHECK	PRADEEP		28/03/18
APPROVAL	PRADEEP		28/03/18

CLIENT - Mastpro Consulting Engineers Pvt. Ltd.
PROJECT - Mars International India Pvt. Ltd.
SITE - Khed City, Pune
If any queries contact : design@nihva.com
DWG. NO. : NIHVA/17-18/0405 REV- 00
ALL DIMENSION ARE IN mm
SCALE: NTS WT: SHEET: 01 OF 01