

PROPOSED PLAN LAYOUT

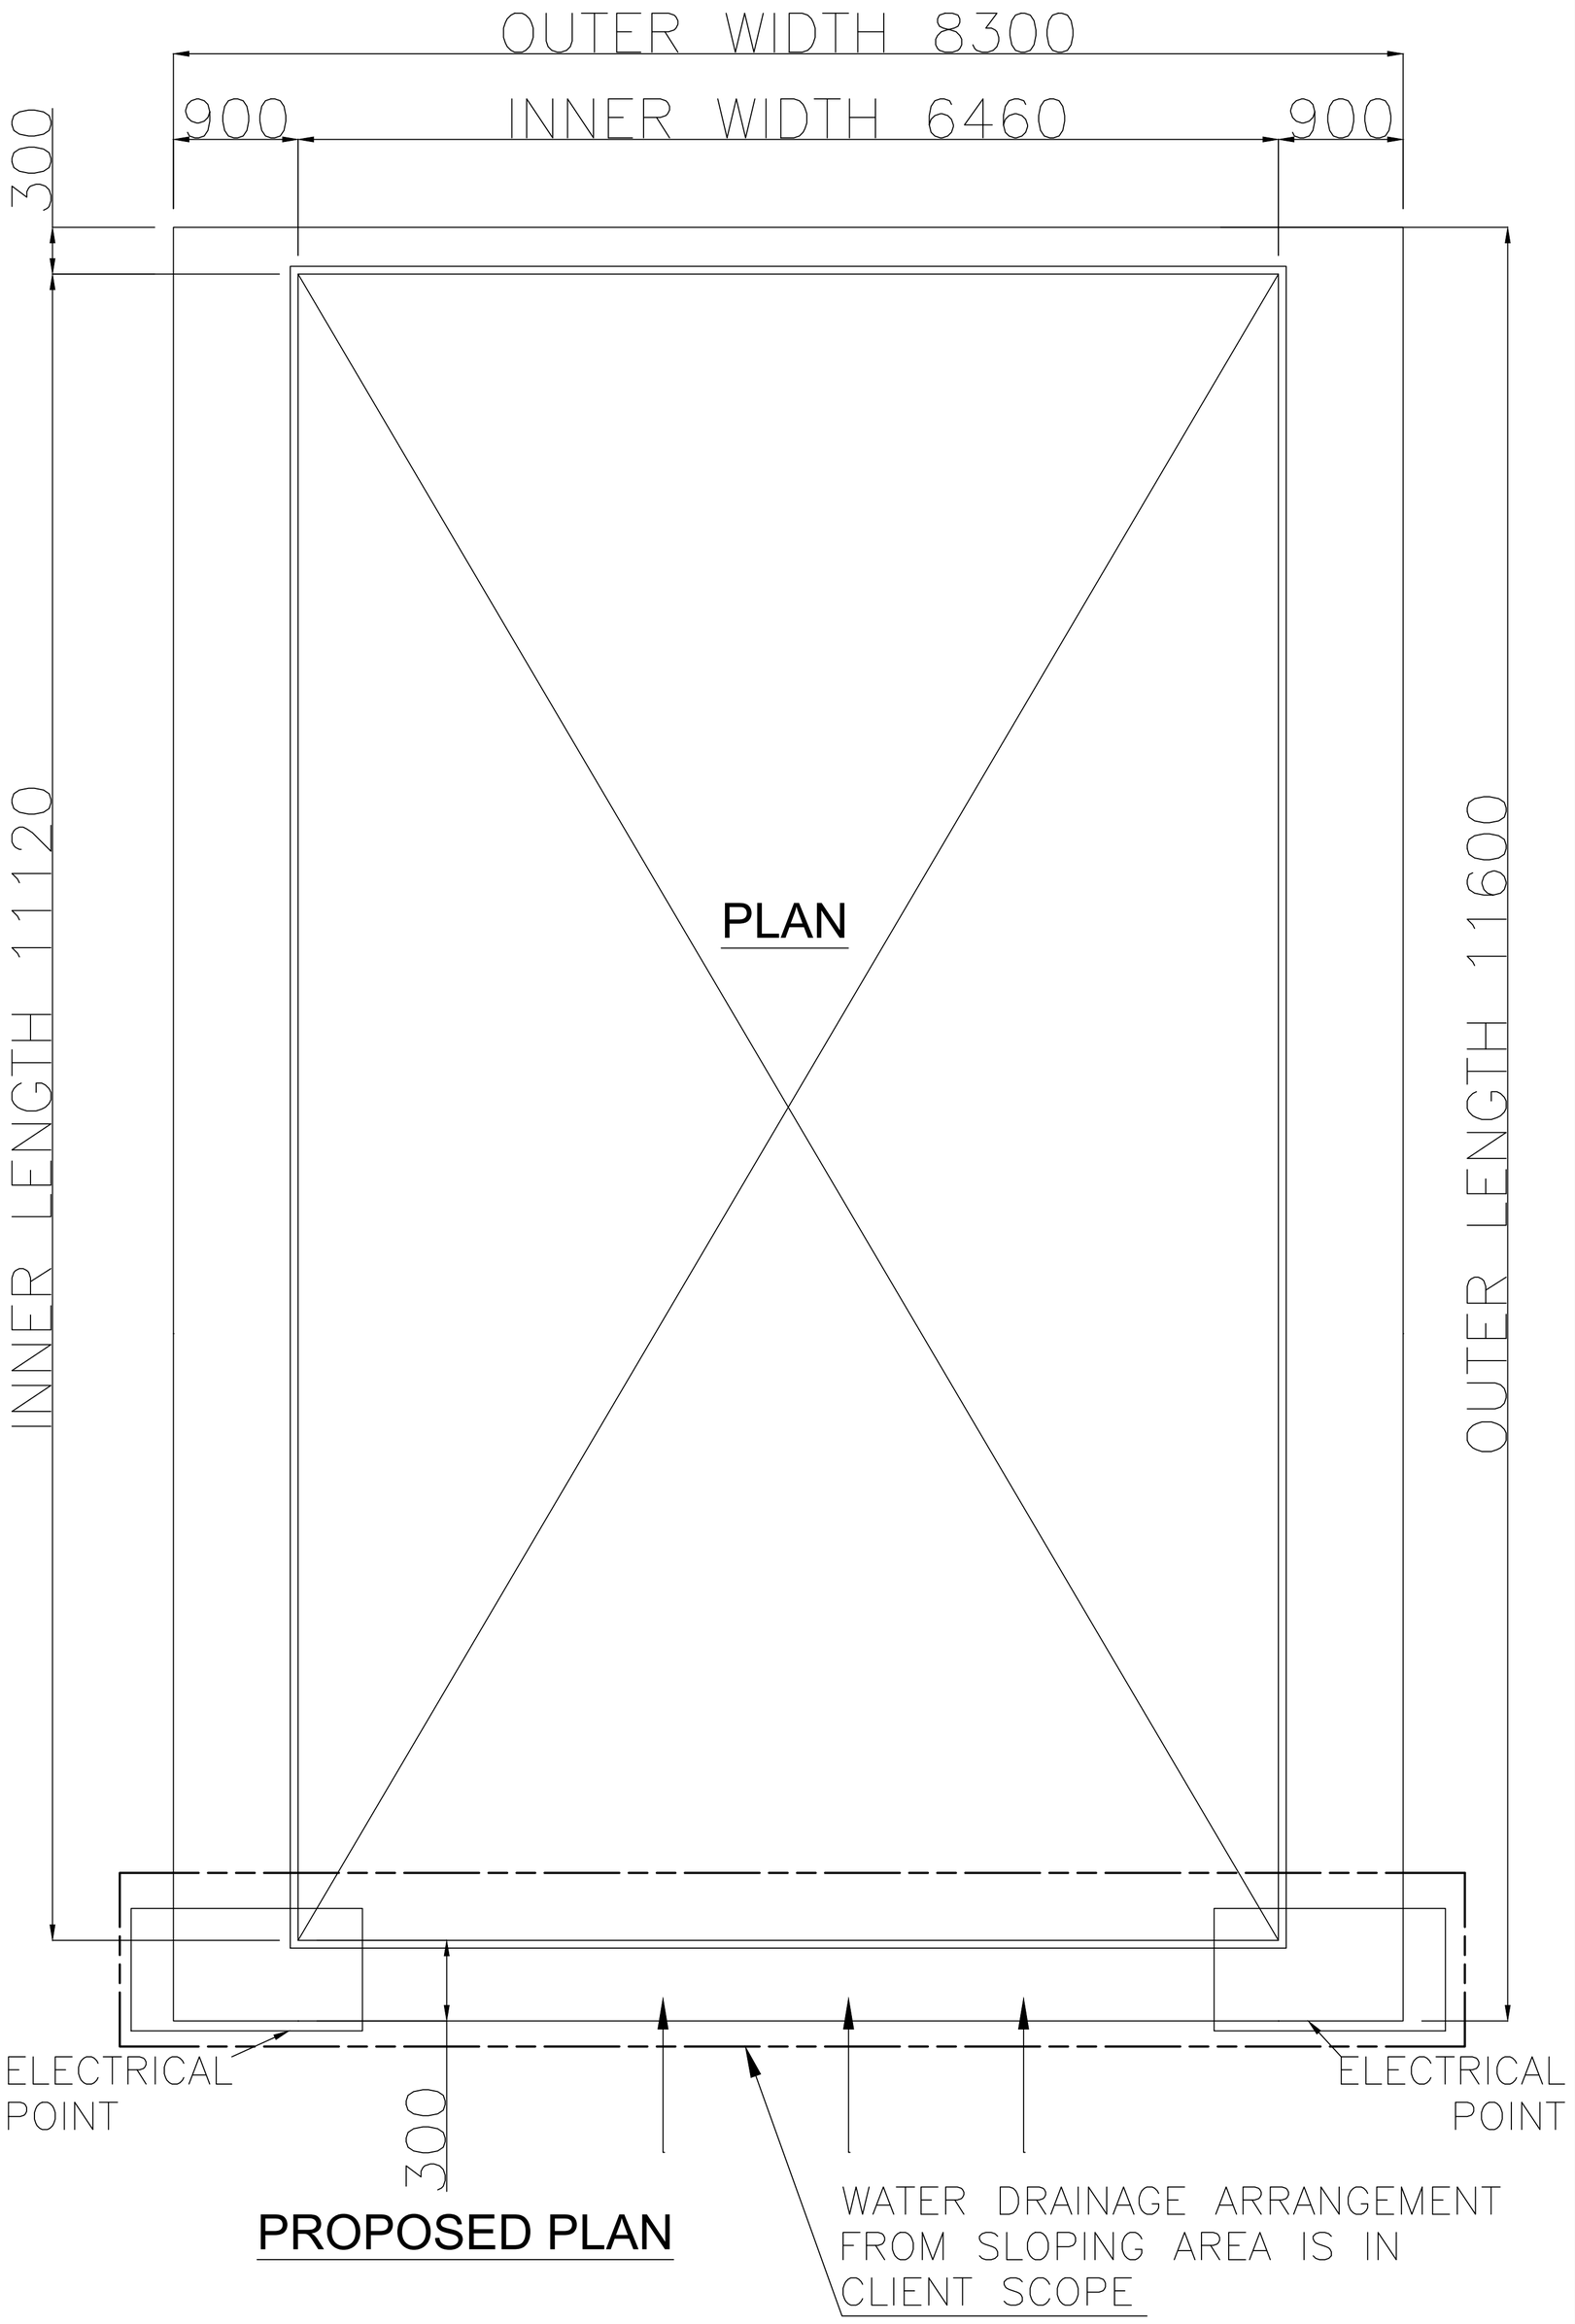

PLAN

PROPOSED PLAN

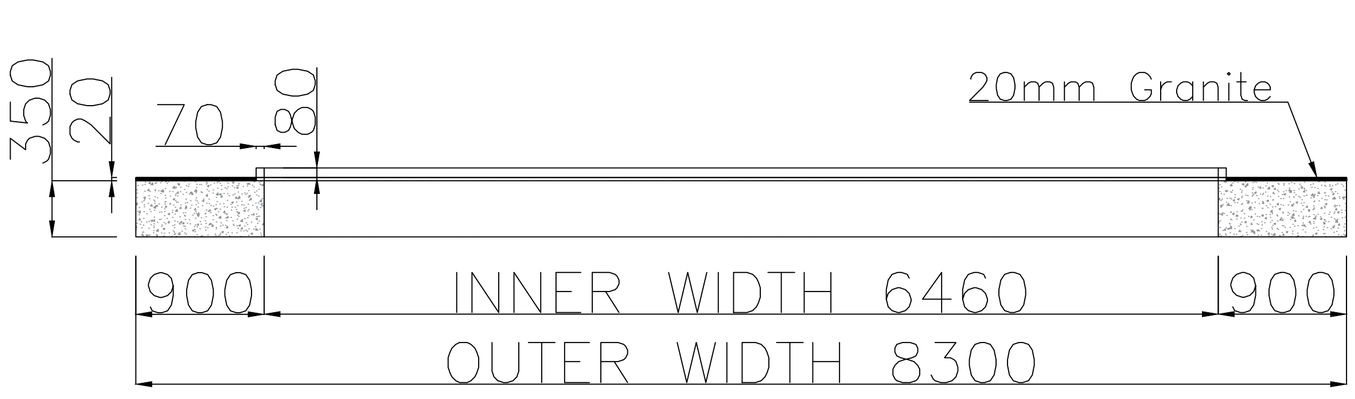

SECTION VIEW

1. THE STRUCTURE AROUND THE CUT OUT SHOULD BE OF CONCRETE FOR FOR PROPER FASTENING OF ROOF.
2. TOP SURFACE SHOULD BE OF GRANITE 20MM FOR SMOOTH FUNCTIONING OF ROOF.
3. ROOF EXTENSION IS SHOWN FOR ONLY REFERENCE. IT CAN BE MODIFIED AS PER THE WORK UNDERTAKEN.
4. GRADIENT OF 80MM NEED TO BE PROVIDED ALONG THE OUTER LENGTH TO AVOID WATER STAGNANCY IN GUIDE RAIL.
5. AL PROFILE - POWDER COATED
6. GASKET - EPDM
7. MOTOR - ITALIAN/GERMAN MAKE
8. ELECTRICAL REQUIREMENT - .
9. ALL DIMENSION IN MM.
10. ALL CIVIL WORK IS IN CLIENT SCOPE

This drawing & design is the property of NIHVA TECHNOLOGIES. Not to be sold or copied to any other concern.

TITLE
PROPOSED PLAN LAYOUT
(IN CLIENT SCOPE)

NIHVA
NIHVA TECHNOLOGIES PVT. LTD.

	NAME	SIGN	DATE
DRAWN	MAHESH S.		30.11.22
CHECK	MAHESH S.		30.11.22
APPRD.	VIJAY T.		30.11.22

CLIENT - MR. MANISH SHAHA		
LOCATION - AHMEDABAD_IN		
PRODUCT - RETRACTABLE ROOF		
If any queries contact : projectsautomation@nihva.com	NIHVA\22-23\02XX	REV- 0
ALL DIMENSION ARE IN mm	SCALE: NTS	SHEET: 01 OF 01