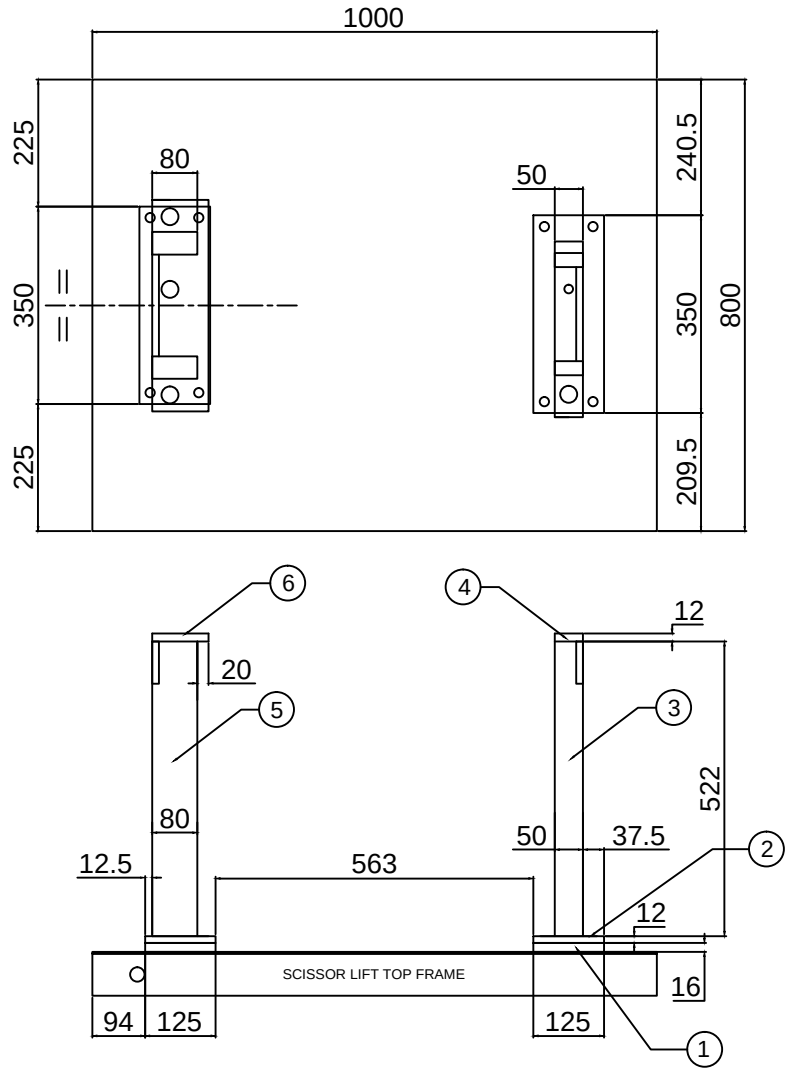

SR NO	DESCRIPTION	QTY
1	FLAT 125 X 16 X 350L	2 NOS
2	FLAT 125 X 12 X 350L	2 NOS
3	R.TUBE 50 X 25 X 3 X 522L	2 NOS
4	FLAT 50 X 12 X 311L	2 NOS
5	R.TUBE 80 X 40 X 3 X 522L	2 NOS
6	FLAT 100 X 12 X 375L	2 NOS

This drawing & design is the property of NIHVA TECHNOLOGIES. Not to be sold or copied to any other concern.

TITLE
FIXTURE MOUNTING FRAME

NIHVA TECHNOLOGIES PVT. LTD.

NIHVA TECHNOLOGIES PVT. LTD. PUNE
Tel : 020 66304033
Email:- info@nihva.com
Website:- www.nihva.com

	NAME	SIGN	DATE
DRAWN	P.A		11.03.2020
CHECK	G.J		11.03.2020
APPRD.			

CLIENT -
PROJECT -
SITE LOCATION -

If any queries contact : design@nihva.com
DWG. NO. : NIHVA/19-20/VDR/369
REV- 0
ALL DIMENSION ARE IN mm
SCALE: NTS
WT:
SHEET: 01 OF 01