


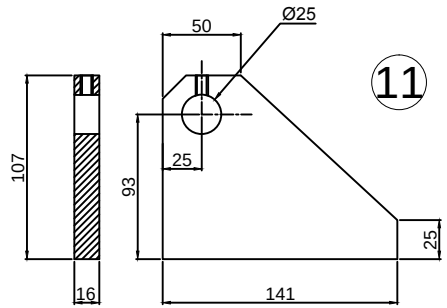


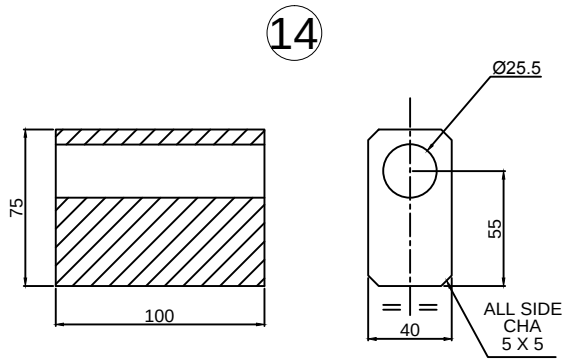

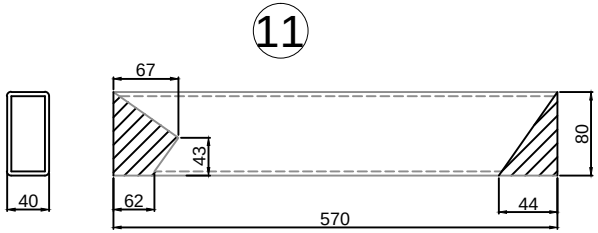

TOP SIDE

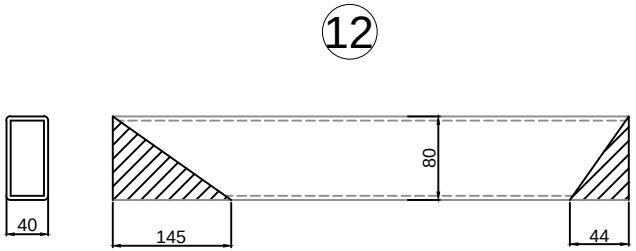

TOP SIDE

This drawing & design is the property of NIHVA TECHNOLOGIES. Not to be sold or copied to any other concern.

TITLE			
BASE FRAME DETAILS			
	NAME	SIGN	DATE
DRAWN	PRADEEP		23.04.2018
CHECK	PRADEEP		23.04.2018
APPRD.	PRADEEP		23.04.2018
If any queries contact : design@nihva.com			
ALL DIMENSION ARE IN mm			

NIHVA
NIHVA TECHNOLOGIES PVT. LTD.
NIHVA TECHNOLOGIES PVT. LTD. PUNE
Tel : 020 66304033
Email:- info@nihva.com
Website:- www.nihva.com

CLIENT -			
PROJECT - DLMP1004			
SITE LOCATION -			
DWG. NO. : NIHVA/18-19/DLMP1004_007_001			
SCALE: NTS	WT:	REV- 00	