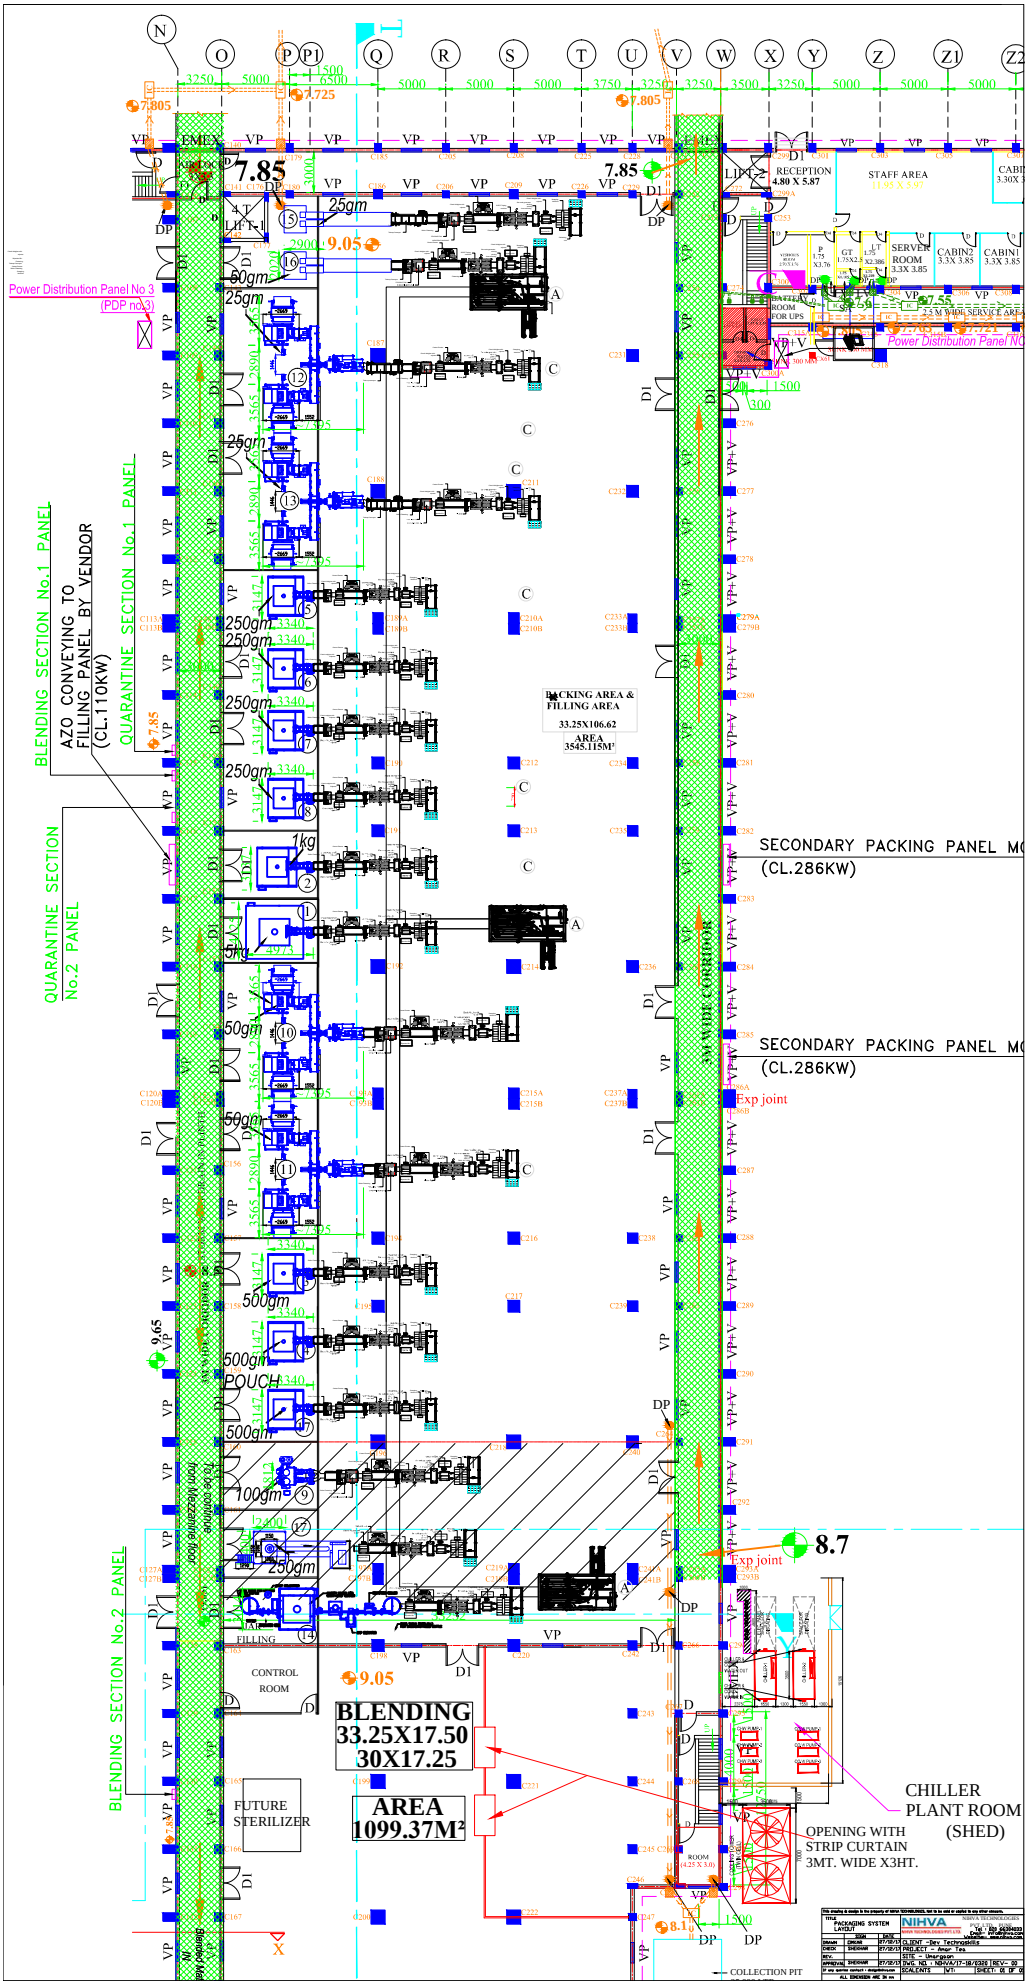

BLENDING SECTION No.1 PANEL
AZO CONVEYING TO FILLING PANEL BY VENDOR (CL.110KW)
QUARANTINE SECTION No.1 PANEL
QUARANTINE SECTION No.2 PANEL
BLENDING SECTION No.2 PANEL
Power Distribution Panel No 3 (PDP no.3)
Power Distribution Panel NO
SECONDARY PACKING PANEL MC (CL.286KW)
SECONDARY PACKING PANEL MC (CL.286KW)
Exp joint
Exp joint
PACKING AREA & FILLING AREA
33.25X106.62
AREA 3545.115M²
30 WIDE CORRIDOR
RECEPTION 4.80 X 5.87
STAFF AREA
SERVER ROOM 3.3X 3.85
CABIN2 3.3X 3.85
CABIN1 3.3X 3.85
BATTERY ROOM FOR UPS
25gm
50gm
250gm
500gm
1kg
5kg
100gm
POUCH
FILLING
CONTROL ROOM
BLENDING 33.25X17.50 30X17.25
AREA 1099.37M²
FUTURE STERILIZER
CHILLER PLANT ROOM (SHED)
OPENING WITH STRIP CURTAIN 3MT. WIDE X3HT.
COLLECTION PIT
7.85
9.05
9.65
8.7
8.1
7.805
7.725
7.55