




PLAN

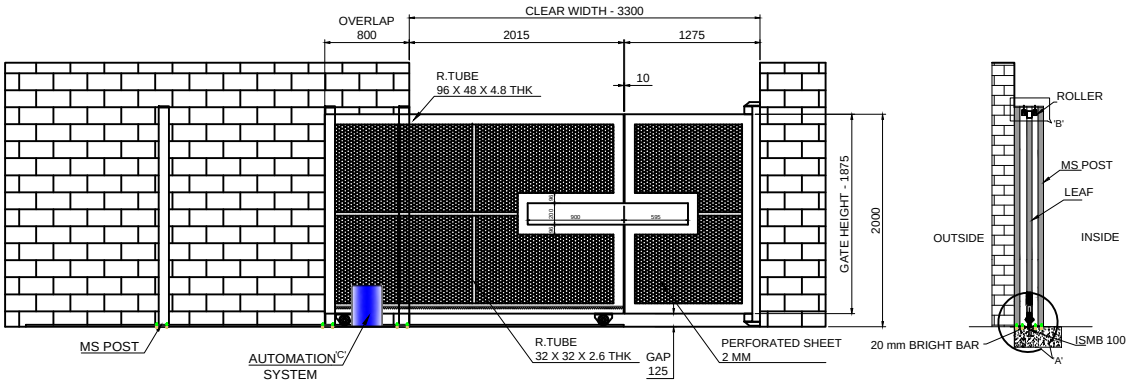

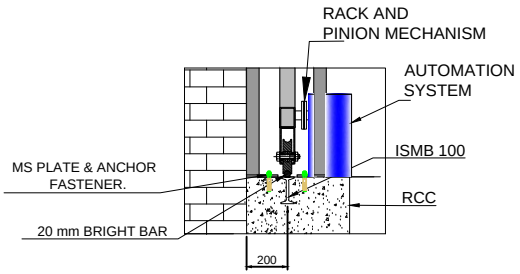

DETAIL VIEW OF A

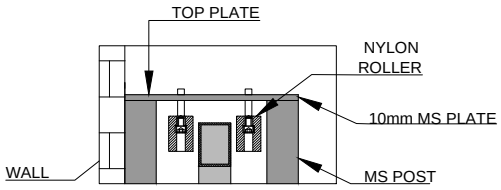

DETAIL VIEW OF B

SR.NO	RAL CODE	RAL COLOR
04	RAL 7035	LIGHT GREY
03	RAL 5002	ULTRAMARINE BLUE
02	RAL 9002	GREY WHITE
01	RAL 1004	GOLDEN YELLOW

DIMENSION :

CLEAR WIDTH	CLEAR HEIGHT	QUANTITY
2015 mm	1875mm	1 NO
1200 mm	1875mm	1 NO

MATERIAL: MS

THICKNESS :

NOTE-
1. ALL REQUIRED CIVIL WORK WILL BE IN CLIENTS SCOPE.

TOLERANCE:- ± 05mm

NIHVA
NIHVA TECHNOLOGIES PVT. LTD.
Website:- www.nihva.com
NIHVA TECHNOLOGIES PVT. LTD. PUNE
Email:- info@nihva.com
TEL :020 66304033

TITLE:
AUTOMATIC SINGLE LEAF SLIDING GATE & MANUAL WICKET GATE

CLIENT'S APPROVAL :

CLIENT - DHAMALE

PROJECT -

SITE LOCATION - NIGADI

DWG. NO. : NIHVA/19-20/0088 | REV. : 00

SCALE: NTS | WT: | SHEET:1 OF 1

DRAWN	P.A		17.09.2019
CHECK	G.J		17.09.2019
APPROVED			

IF ANY QUERIES CONTACT:- design@nihva.com

NOTE: ALL DIMENSIONS ARE IN mm

THIS DRAWING & DESIGN IS THE PROPERTY OF NIHVA TECHNOLOGIES. NOT TO BE SOLD OR COPIED TO ANY OTHER CONCERN.