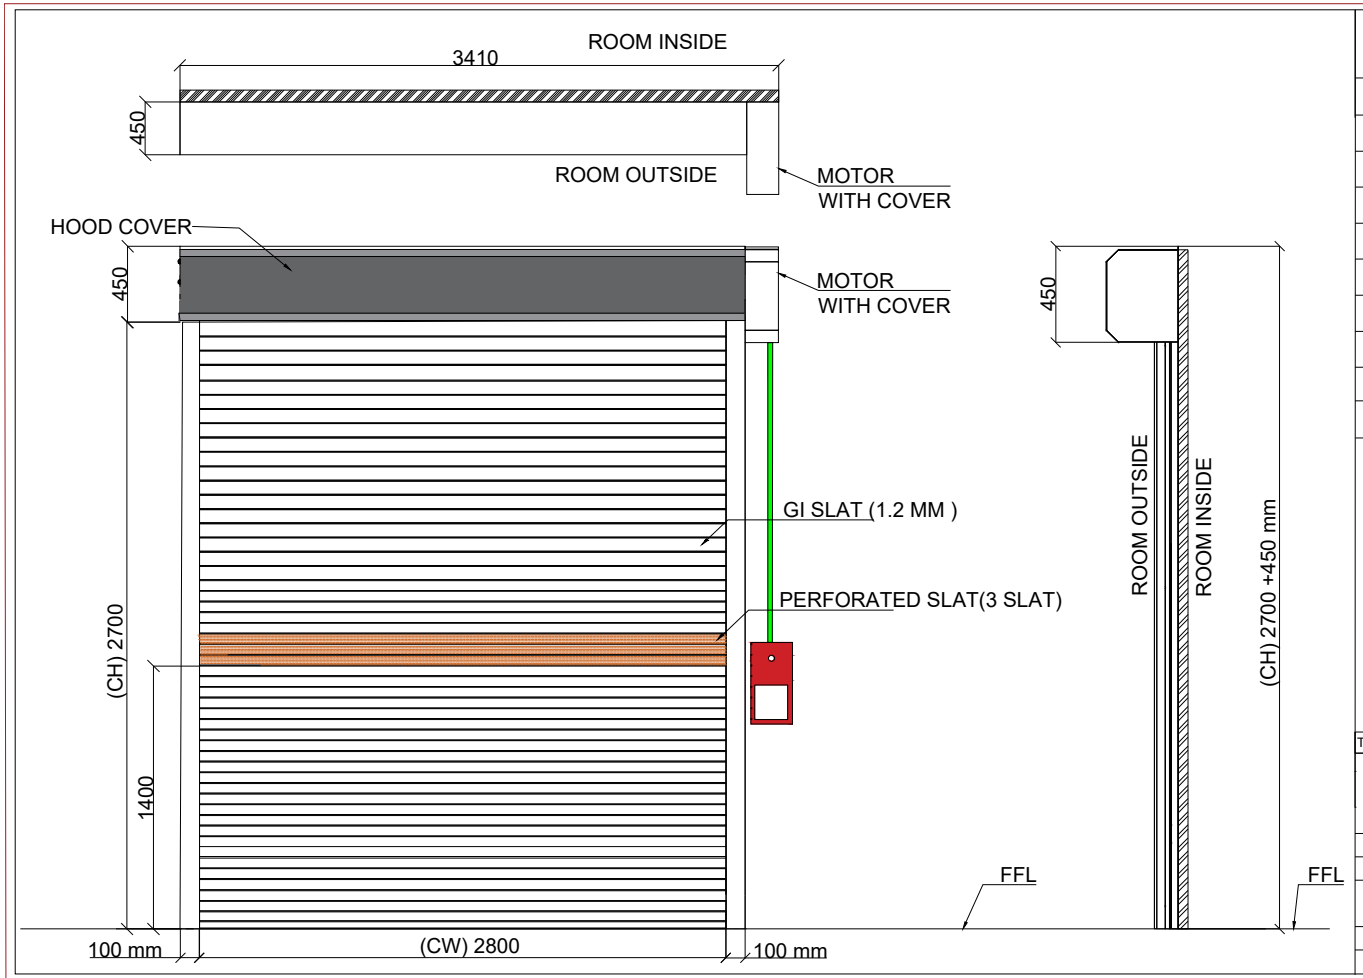


TECHNICAL SPECIFICATION:-

SR.	SPECIFICATION	DETAILS
1.	DESCRIPTION & DRIVE	MOTORIZED ROLLING SHUTTER (DIRECT DRIVE)
2.	LOCATION AREA	INSIDE AREA / OUTSIDE AREA
3.	MOUNTING SURFACE	SIDE BRACKETS: OPTIONAL = STEEL&SIDE
4.	SLAT	GI SLAT- 1.2 MM THICK (75 MM WIDTH)
5.	SLAT	PERFORATED 3 SLAT FROM GROUND LEVEL AT 1400 MM
6.	BOTTOM PROFILE	MS PLATE100 x 2.5 MM THICK WITH ANGLE STIFFENER.
7.	GUIDE PROFILE	M.S." T " SHAPED PROFILE 100X3 MM THICK.
8.	HOOD COVER & MOTOR COVER	MADE OF GI SHEET THICKNESS 0.9 MM.
9.	SURFACE FINISH	POWDER COATED IN RAL 9002

SHUTTER SIZES :-

SR.	CLEAR WIDTH	CLEAR HEIGHT	QTY.
01	2800 mm	2700 mm	03

NOTE :-

1. All DIMENSIONS ARE IN MM.
2. QTY - 3NOS WITH MOTOR AT R.H SIDE

This drawing & designing is the property of NIHVA TECHNOLOGIES. Not to be sold or copied to any other concern.

TITLE :- MOTORIZED ROLLING SHUTTER(DIRECT DRIVE)

NIHVA TECHNOLOGIES PVT. LTD. PUNE
Tel : 020 66304033
Email:- info@nihva.com
Website:- www.nihva.com

	NAME	DATE
DRAWN	B.S.	09/02/2026
CHECK & APPROVAL	V.T.	09/02/2026

PROJECTION METHOD

PRODUCT - ROLLING SHUTTER
PROJECT NAME - POONA SURFACE COATING
FORMAT NO - NIHVA-DD-F-03
DWG. NO. : NTPL-00 | REV-00
SCALE: NTS | WT:245 KG | SHEET: 01 OF 01
ALL DIMENSION ARE IN mm
If any queries contact : design@nihva.com