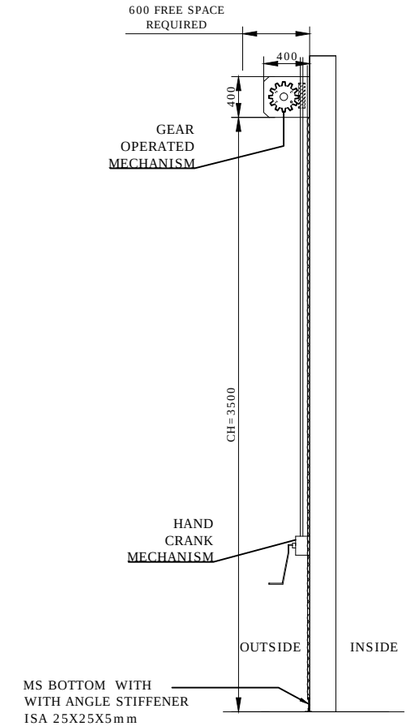
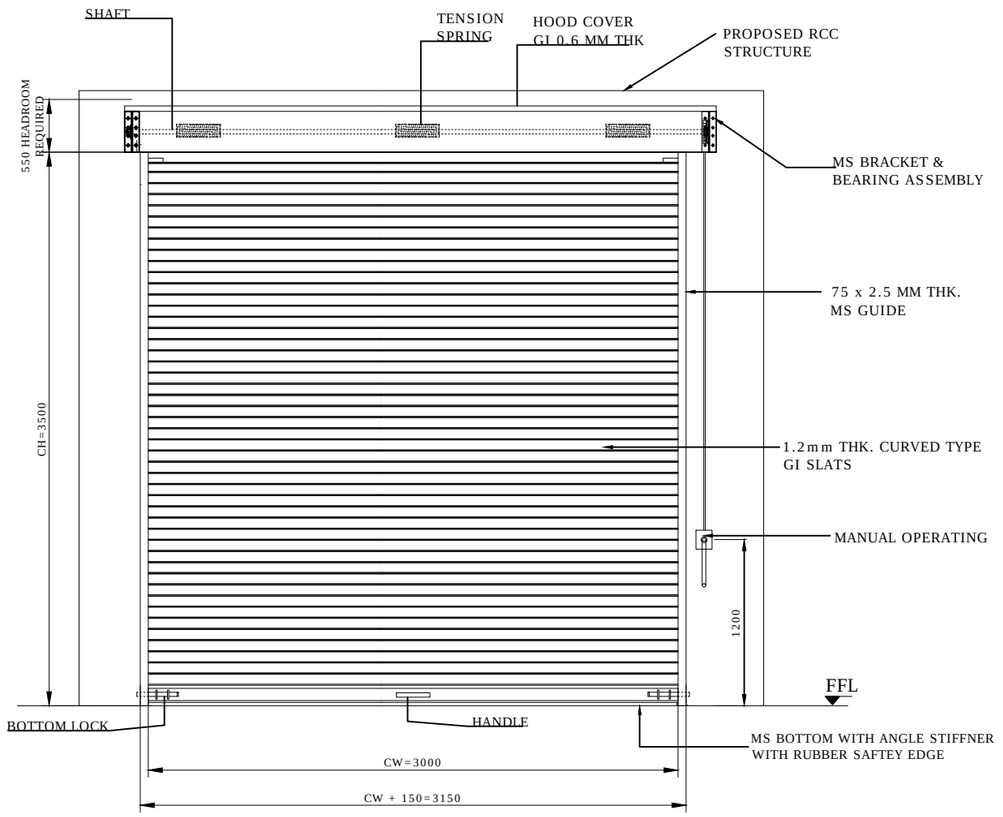
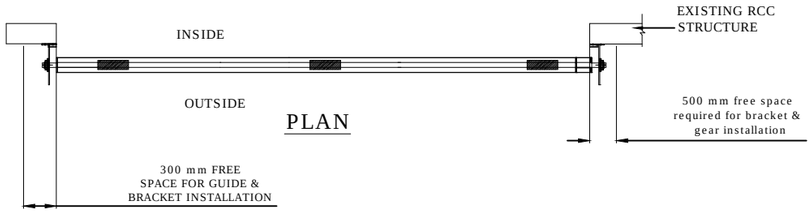


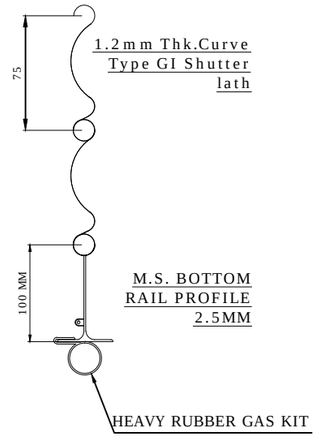

SIDE VIEW



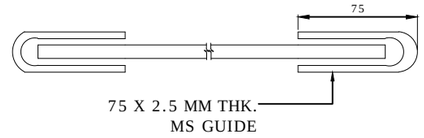

OUTSIDE ELEVATION




PLAN




M.S. BOTTOM RAIL PROFILE 2.5MM




| RAL CODE | RAL COLOR | APPROVED |
|---|---|---|
| RAL 9010 | PURE WHITE | |
| RAL 9002 | GREY WHITE | |
| RAL 7035 | LIGHT GREY | |
| RAL 5002 | ULT. M. BLUE | |

REV 01 (18-02-2022)
1. QUANTITY OF SHUTTER CHANGED TO 4 NOS.

REV 02 (19-02-2022)
1. CHANGED MOUNTING OF SHUTTER ON CONCRETE WALL.

REV 03 (22-02-2022)
1. FIXED THE MOUNTING OF LEVER ON RIGHT SIDE.
2. CHANGED THE QUANTITY OF SHUTTERS TO 1 NOS.

NOTE-
1. ALL CIVIL WORK WILL BE CLIENT'S SCOPE.
2. IF STRUCTURE REQUIRED FOR SHUTTER IS IN CLIENT'S SCOPE.
3. SURFACE FINISH: POWDER COATING OF APPROVED RAL CODE.
4. MOUNTING ON OUTSIDE CONCRETE STRUCTURE.
5. MOUNTING OF LEVER WILL BE ON RIGHT SIDE.

| SR NO | ( CW ) CLEAR WIDTH | ( CH ) CLEAR HEIGHT | QUANTITY |
|---|---|---|---|
| 1 | 3000 | 3500 | 01 NO |

TOLERANCE - ±10mm

This drawing & design is the property of NIHVA TECHNOLOGIES. Not to be sold or copied to any other concern.

TITLE
GEAR OPERATED ROLLING SHUTTER

| | NAME | SIGN | DATE |
|---|---|---|---|
| DRAWN | G.I.P | | 15.02.2022 |
| CHECK | A.K. | | 15.02.2022 |
| APPRD. | V.T. | | 15.02.2022 |

If any queries contact : design@nihva.com

ALL DIMENSION ARE IN mm

NIHVA TECHNOLOGIES PVT. LTD.
Website:- www.nihva.com
NIHVA TECHNOLOGIES PVT. LTD. PUNE
Tel : 020 66304033
Email:- info@nihva.com

CLIENT - QUALITY INFRASTRUCTURE PVT LTD
PROJECT -GEAR OPERATED ROLLING SHUTTER
SITE LOCATION -GUJARAT
DWG. NO. : NIHVA/21-22/CLT/353 | REV- R3
SCALE: NTS | WT: | SHEET: 01 OF 01