


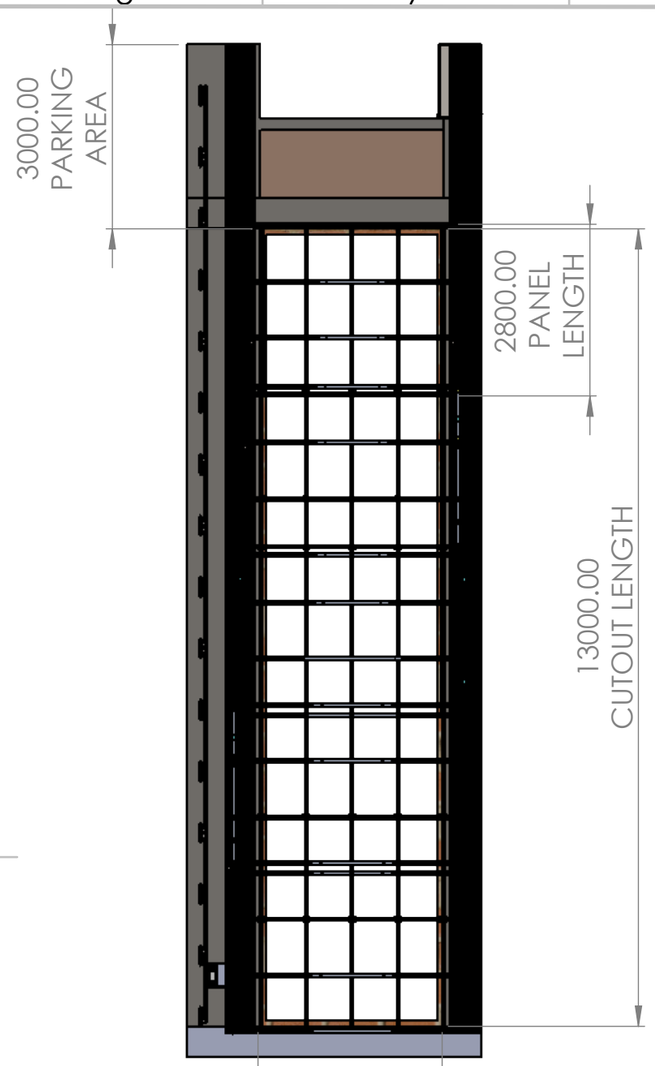


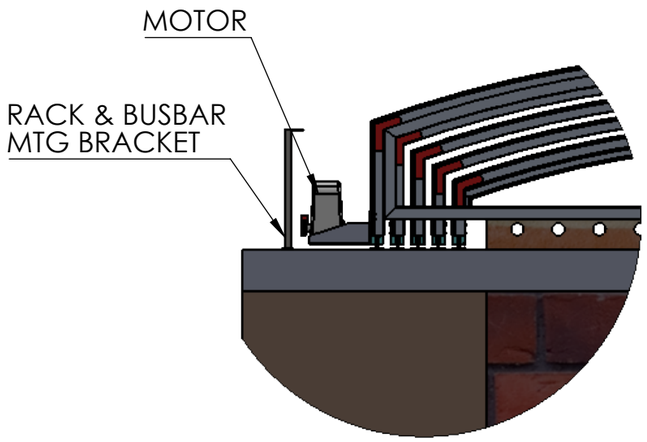


DETAIL B
SCALE 1 : 30

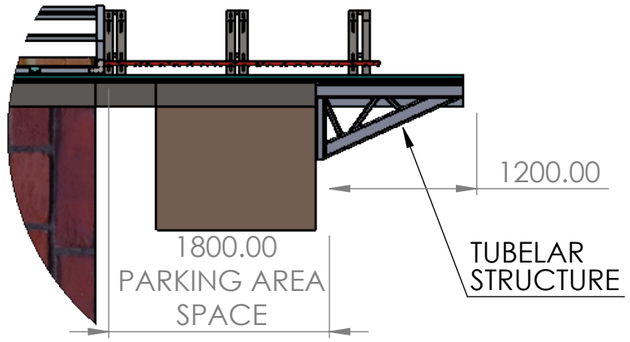


DETAIL D
SCALE 1 : 50

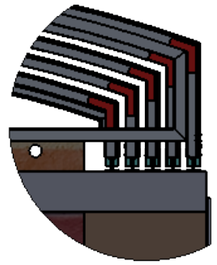

DETAIL C
SCALE 1 : 30

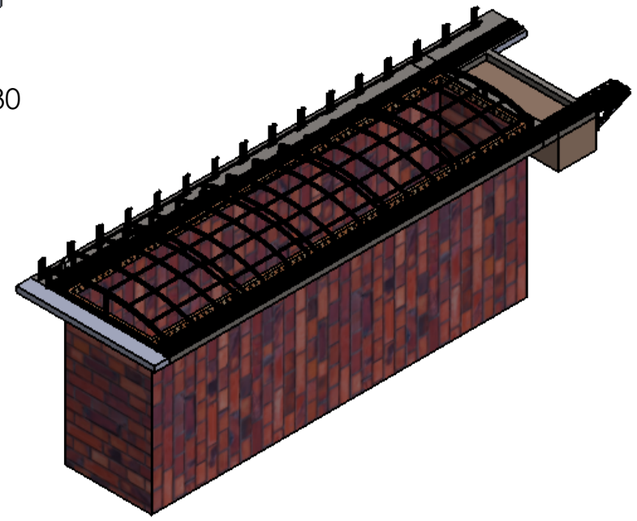

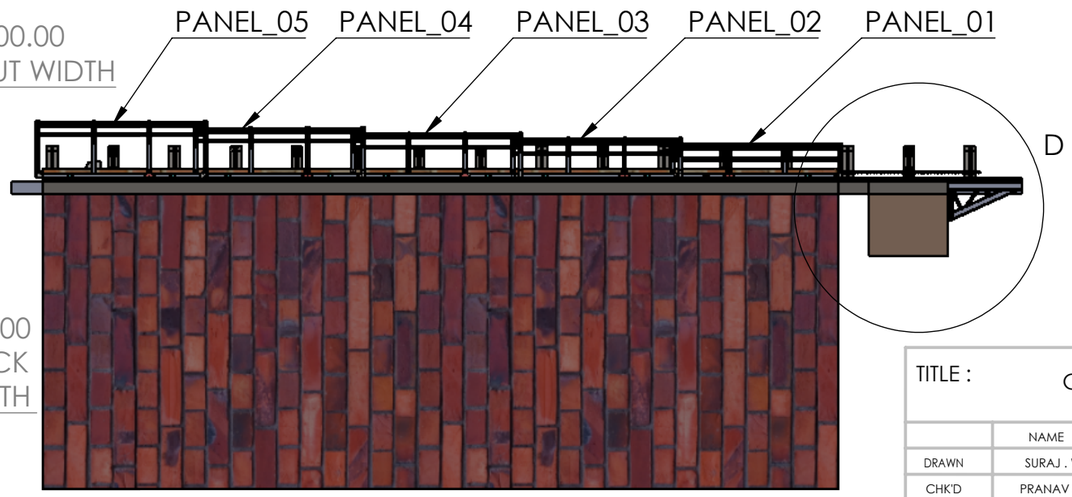

TITLE :	GA DRAWING	NIHVA Technologies Pvt. Ltd.	NIHVA TECHNOLOGIES PVT LTD
	NAME	SIGNATURE	DATE
DRAWN	SURAJ . W		27-03-2025
CHK'D	PRANAV M.		27-03-2025
APPV'D	VIJAY T.		27-03-2025
CLIENT NAME :	MANUSH BHAI GUJARAT		
PRODUCT NAME :	RETRACTABLE ROOF		
SITE LOCATION :	GUJARAT		
DWG NO.	GA	A3	
		REVISION : 0	
	DIMENSIONS ARE IN MILLIMETERS	SCALE:	SHEET 1 OF 1