


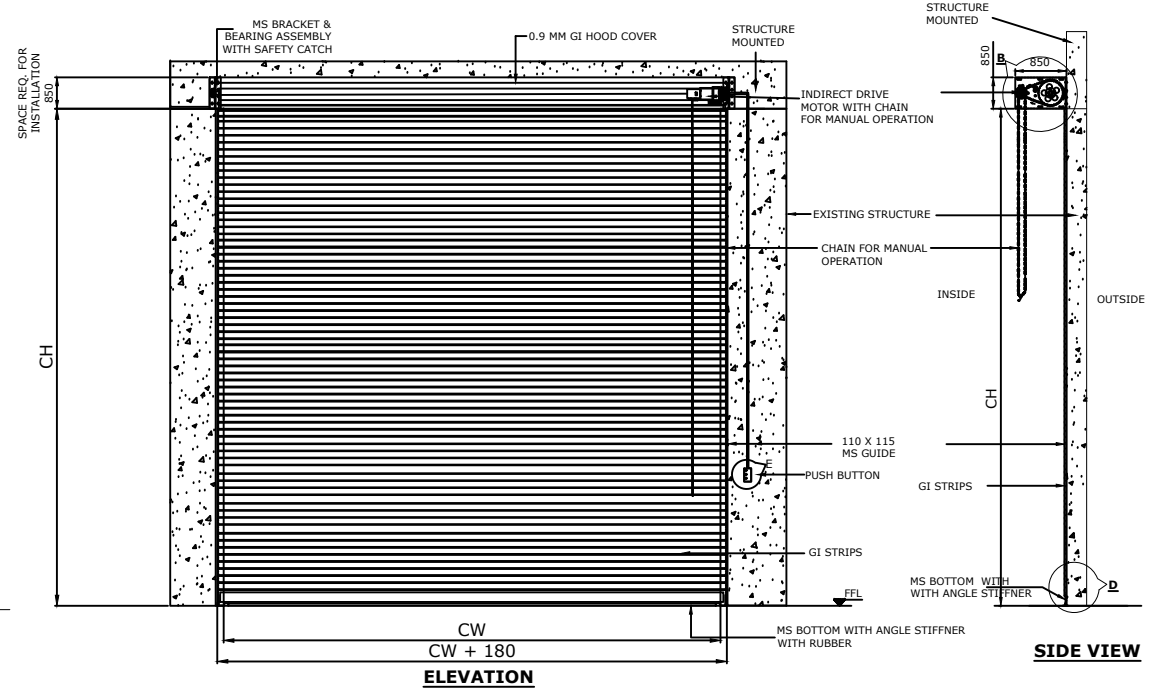


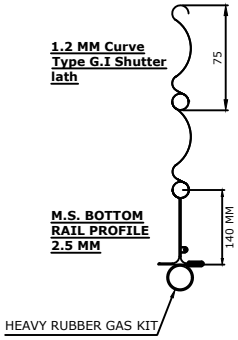


DETAILS : D

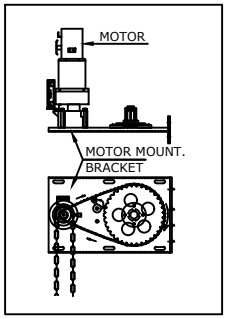


DETAILS : A & B

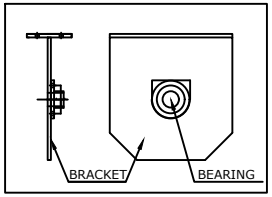

DETAILS : C

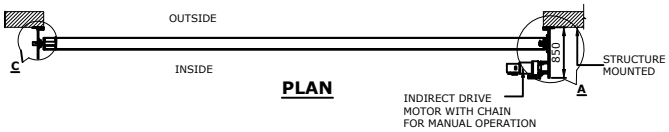

PLAN

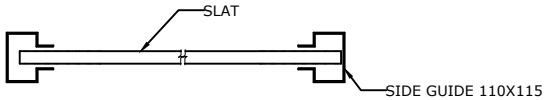

NOTE:
(1) REQUIRED TECHNICAL M.S. STRUCTURE & ALL CIVIL WORK FOR SHUTTER IN CLIENT SCOPE (STRUCTURE DRAWING WILL BE SHARED SEPARATELY).
(2) SHUTTER WILL BE INSTALLED AT SITE AFTER READINESS OF STRUCTURE AS PER DRAWING PROVIDED.
(3) TOTAL OPENING AVAILABLE WILL BE 150 MM LESS THAN CLEAR HEIGHT PROVIDED.

CLEAR WIDTH (CW)	CLEAR HEIGHT (CH)	QUANTITY	RAL COLOR POWDER COATING
6000	6200	2	RAL -
6000	8200	4	RAL -

This drawing & design is the property of NIHVA TECHNOLOGIES. Not to be sold or copied to any other concern.

TITLE: MOTORIZED ROLLING SHUTTER

NIHVA TECHNOLOGIES PVT. LTD.

NIHVA TECHNOLOGIES PVT. LTD. PUNE
Tel : 020 66304033
Email:- info@nihva.com
Website:- www.nihva.com

	NAME	SIGN	DATE
DRAWN	A.J.		18.11.2020
CHECK	K.P.		18.11.2020
APPRD.			

CLIENT -
PROJECT -
SITE LOCATION -
If any queries contact : projectsupport@nihva.com
DWG. NO. : NIHVA/20-21/0069 REV- R00
ALL DIMENSION ARE IN mm
SCALE: NTS WT: SHEET: