

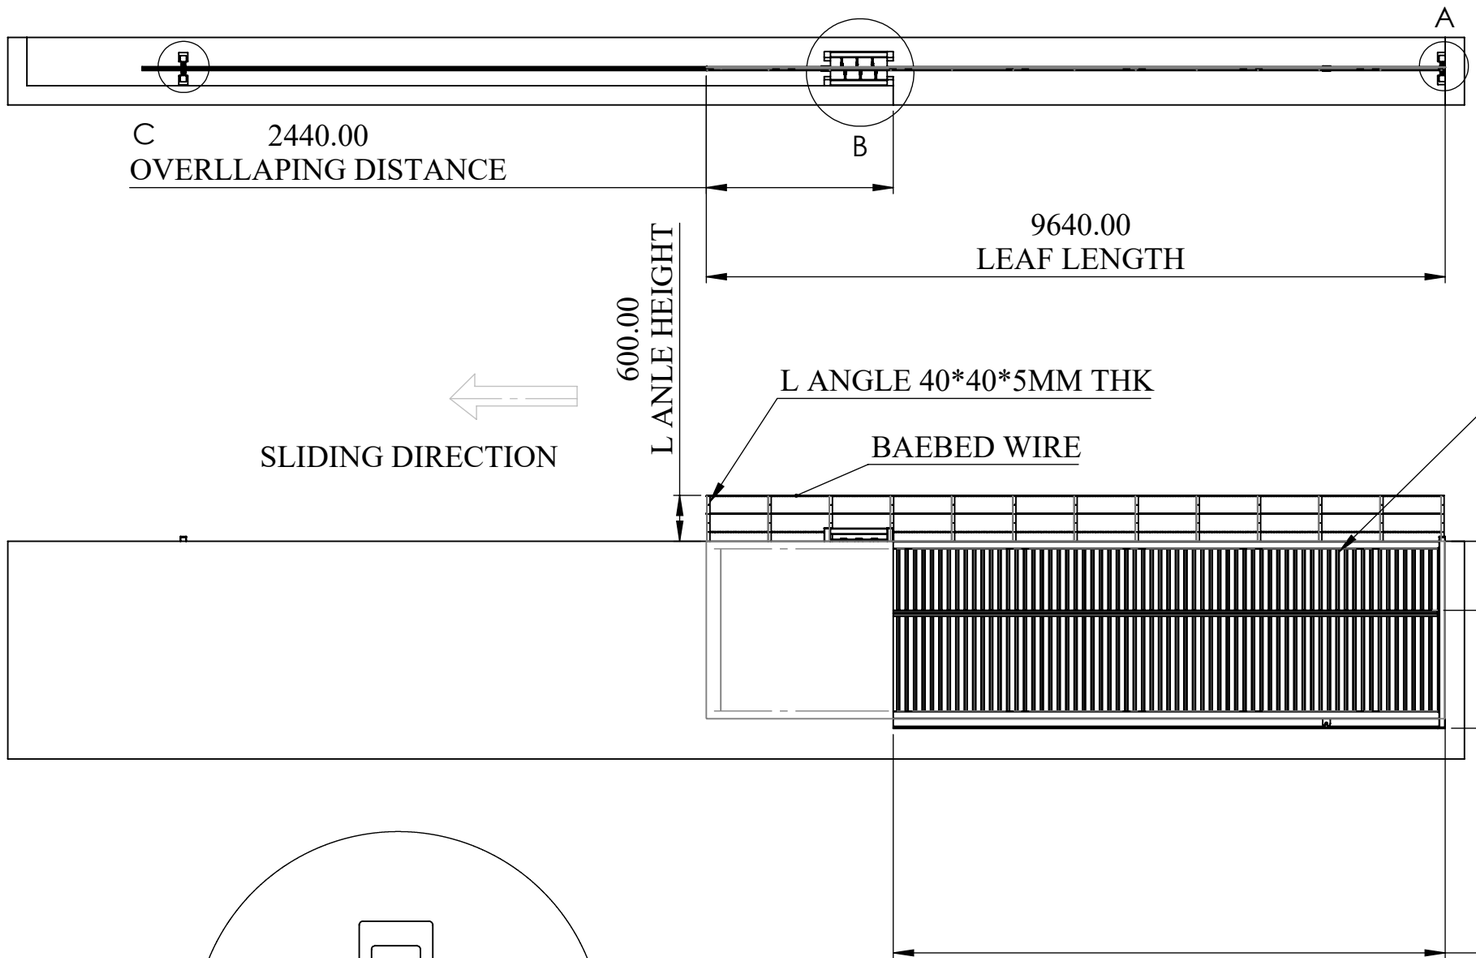


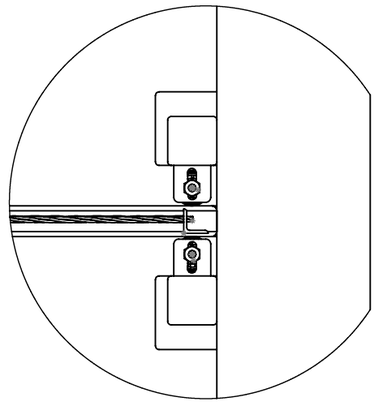

DETAIL A
SCALE 1 : 10


RECT MS TUBE
100*50*5MM THK

POST 1 AND NYLON
BEARING ASM

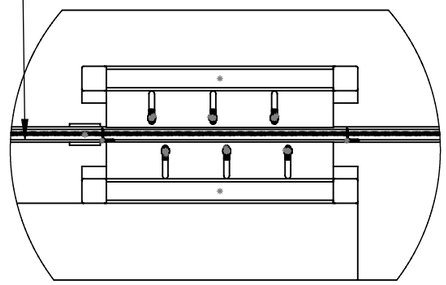

DETAIL B
SCALE 1 : 20

POST 2 AND NYLON
BEARING ASM

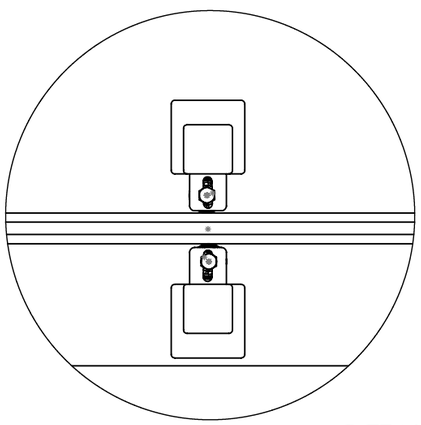

DETAIL C
SCALE 1 : 10

POST NO 3 &
NYLON ROLLER BERAING
ASM

GA DRAWING
TYPE NO 01

TITLE - GATE				NIHVA TECHNOLOGIES PVT.LTD.PUNE
DWG NO - NTPL-000-PM-001-00-00-00				Website - www.nihva.com
	NAME	SIGNATURE	DATE	PROJECT NO - NTPL-000-PM
DRAWN	V.W		02-05-2025	PRODUCT - SINGLE SLIDING GATE
CHK'D	S.W.		02-05-2025	SITE LOCATION -
APPV'D	V.T.		02-05-2025	
if any queries contact - supportautomation@nihva.com				REVISION - / QTY - 1
ALL DIMENSION ARE IN mm		A3		SCALE / SHEET 1 OF 1