


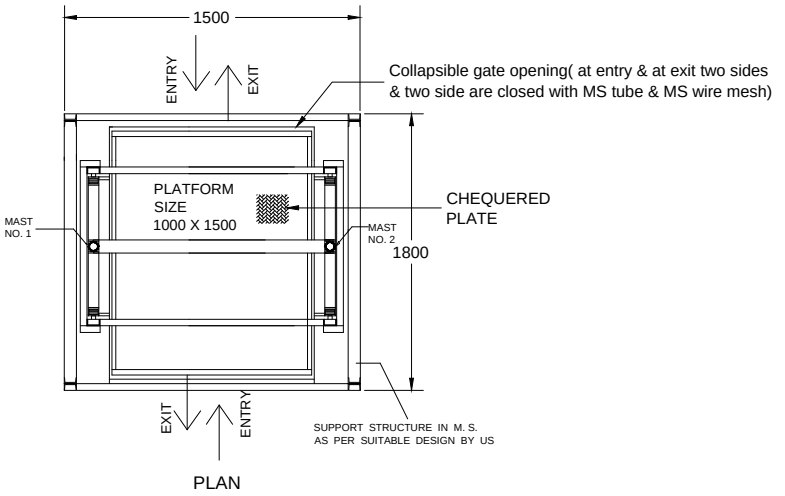


| | |
|---|---|
| CAPACITY | 1000 KGS |
| NO. OF FLOORS | GROUND + 1 FLOOR |
| PLATFORM SIZE | 1000 mm X 1500 mm |
| LOWER HEIGHT | 200 mm |
| LIFT HEIGHT | 3000 mm |
| OPERATION | 3 HP A. C. POWERPACK |
| NO. OF HYD. CYLINDERS | 2 NOS |
| LIFTING SPEED | 50-60 mm/s |
| NO. OF HYD. CYLINDERS | 2 NOS |
| COLOR OF EQUIPMENT | GOLDEN YELLOW RAL 1003 |
| POWER SUPPLY | 440VAC,3PH,50HZ |

This drawing & design is the property of NIHVA TECHNOLOGIES. Not to be sold or copied to any other concern.

TITLE

GOODS LIFT
G.A. DRG

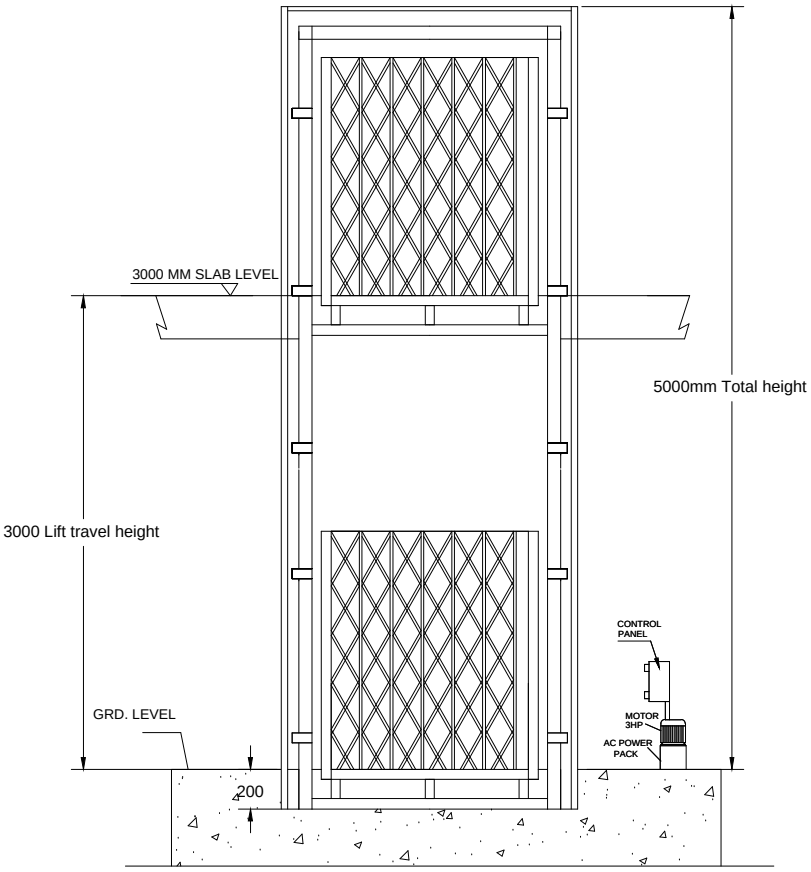CLIENT APPROVAL

ALL DIMENSION ARE IN mm

| | SIGN | DATE |
|---|---|---|
| DRAWN | OMKAR | 30/03/17 |
| CHECK | SAGAR P. | 30/03/17 |
| REV. | | |
| APPRD. | R.K. | 30/03/17 |
| MFG | | |
| Ref. No. | | |

NIHVA TECHNOLOGIES PVT. LTD.

NIHVA TECHNOLOGIES PVT. LTD. PUNE
Tel : 020 66304033
Email:- info@nihva.com
Website:- www.nihva.com

CLIENT - FERRERO INDIA PVT. LTD.

PROJECT -

SITE - BARAMATI

DWG. NO. - NIHVA/16-17/198

SCALE: NTS | WT: | SHEET: 01 OF 01

If any queries contact : projects@nihva.com