

Abbrevation's:
WOW-Wall Opening Width
WOH-Wall Opening Height
CH- Clear Height
UC-Under Cut
FFL-Finished Floor Level

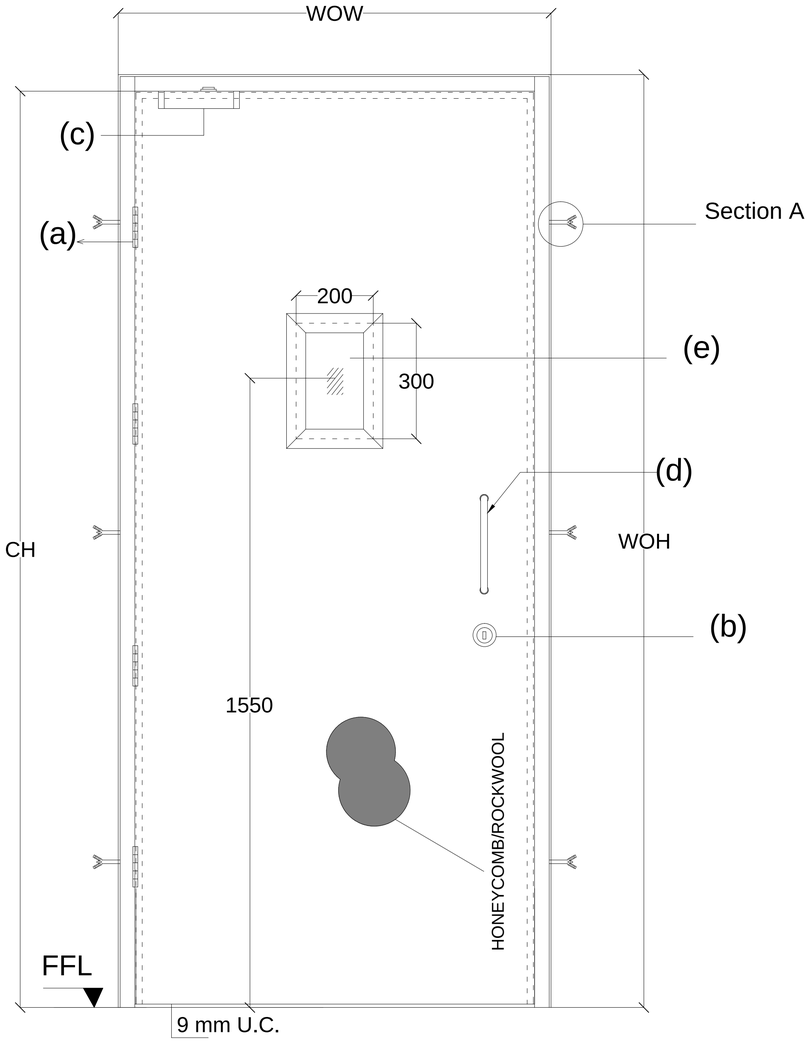

ELEVATION



TOP VIEW

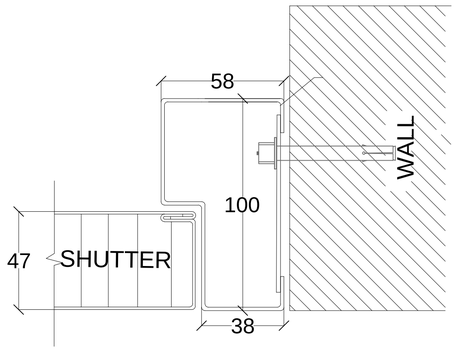

ASSESORIES DETALES

(a) HINGES: SS hinges 100x75x3mm

(b) LOCK : Mortise dead Lock with cylinder(One side key & thumb turn on other side)with escutcheon.

(c) DOOR CLOSER : B4W

(d) HANDLE : D Handle (300x22) pair.

(e) VISION PANEL - 5mm THK. GLASS OF SIZE-200X300mm

Shutter thickness : 47 mm
Frame Sheet thick : 1.20mm
Shutter sheet thick : 0.80mm
Fixing : On Soliid Brick plasterd wall with Anchors

NOTE:- *All Dimensions are in mm.
*Tolerance:-All Linear Dimensions ±3mm,Others ±0.5mm.
*The Drawing Is For Location of Hardware only. Drawing Does Not Represent The Hardware For More Clarity, Please Go Through Hardware Broucher.

Fire door size

WOW	WOH	TYPE 1	TYPE 2	TYPE 3	TYPE 4	QUANTITY
1200	2125					1

NOTE- CLIENT SHOULD SELECT DOOR TYPE FROM DOOR HANDLING SHEET & COLOR OF DOOR.

This drawing & designing is the property of NIHVA TECHNOLOGIES. Not to be sold or copied to any other concern.

TITLE STEEL DOOR

NIHVA TECHNOLOGIES PVT. LTD.
NIHVA TECHNOLOGIES PVT. LTD. PUNE
Tel : 020 66304033
Email:- info@nihva.com
Website:- www.nihva.com

	SIGN	DATE
DRAWN	OMKAR	11/07/17
CHECK	SHEKHAR	11/07/17
REV.	00	
APPROVAL		

CLIENT - VAICHAL CONSTRUCTION
PROJECT - TAGMA CENTRE
SITE - CHAKAN
DWG. NO. : NIHVA/17-18/0131

If any queries contact : projects@nihva.com
SCALE: NTS | WT: | SHEET: 01 OF 01
ALL DIMENSION ARE IN mm