


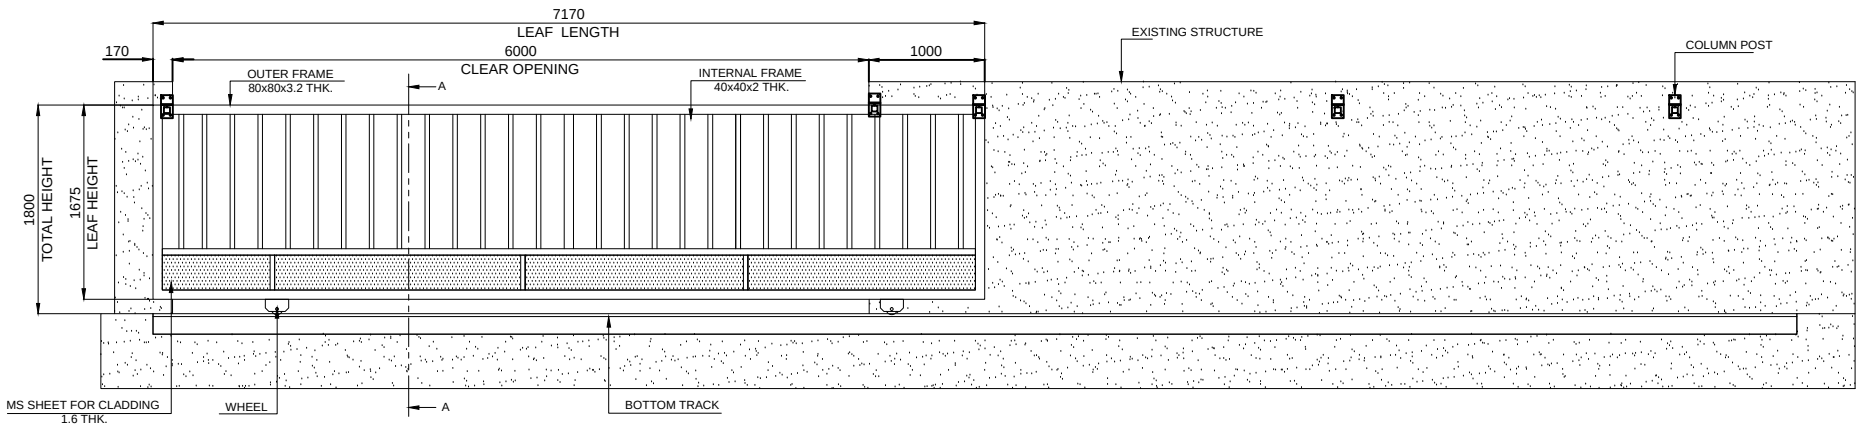


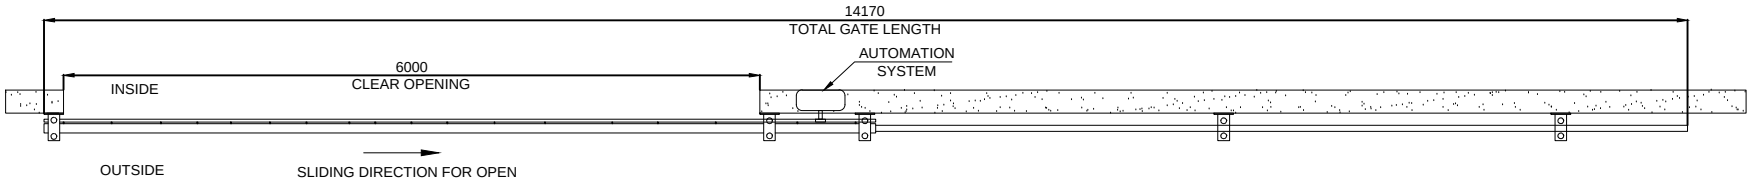

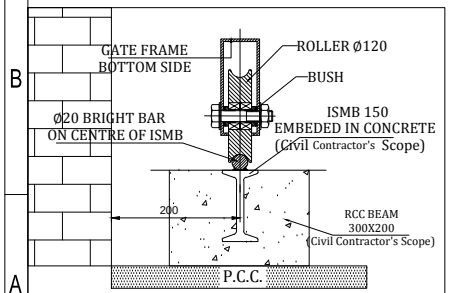


SLIDING ROLLER

DETAIL 'B'

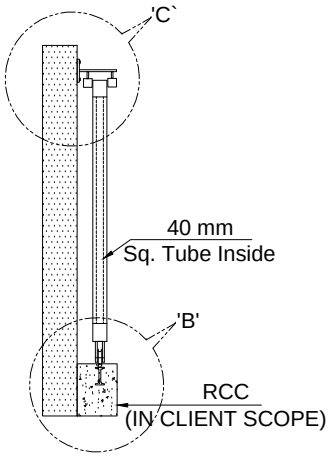

SECTION A-A

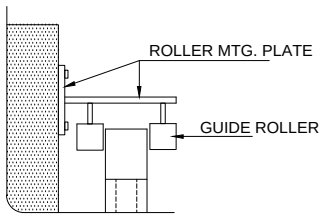

DETAIL 'C'

TOLERANCE - ±10mm

This drawing & design is the property of NIHVA TECHNOLOGIES. Not to be sold or copied to any other concern.

TITLE: MOTORIZED SLIDING GATE			NIHVA TECHNOLOGIES PVT. LTD. PUNE Tel : 020 66304033 Email:- info@nihva.com Website:- www.nihva.com
	NAME	SIGN	DATE
DRAWN	A.K.		27.11.18
CHECK	P.A.		27.11.18
APPRD.	R.D		27.11.18
CLIENT - MERIT Engineers & Consultants			
PROJECT -			
SITE LOCATION - PUNE			
If any queries contact : design@nihva.com	DWG. NO. : NIHVA/18-19/0182		REV- 0
ALL DIMENSION ARE IN mm	SCALE: NTS	WT:	SHEET: 01 OF 01