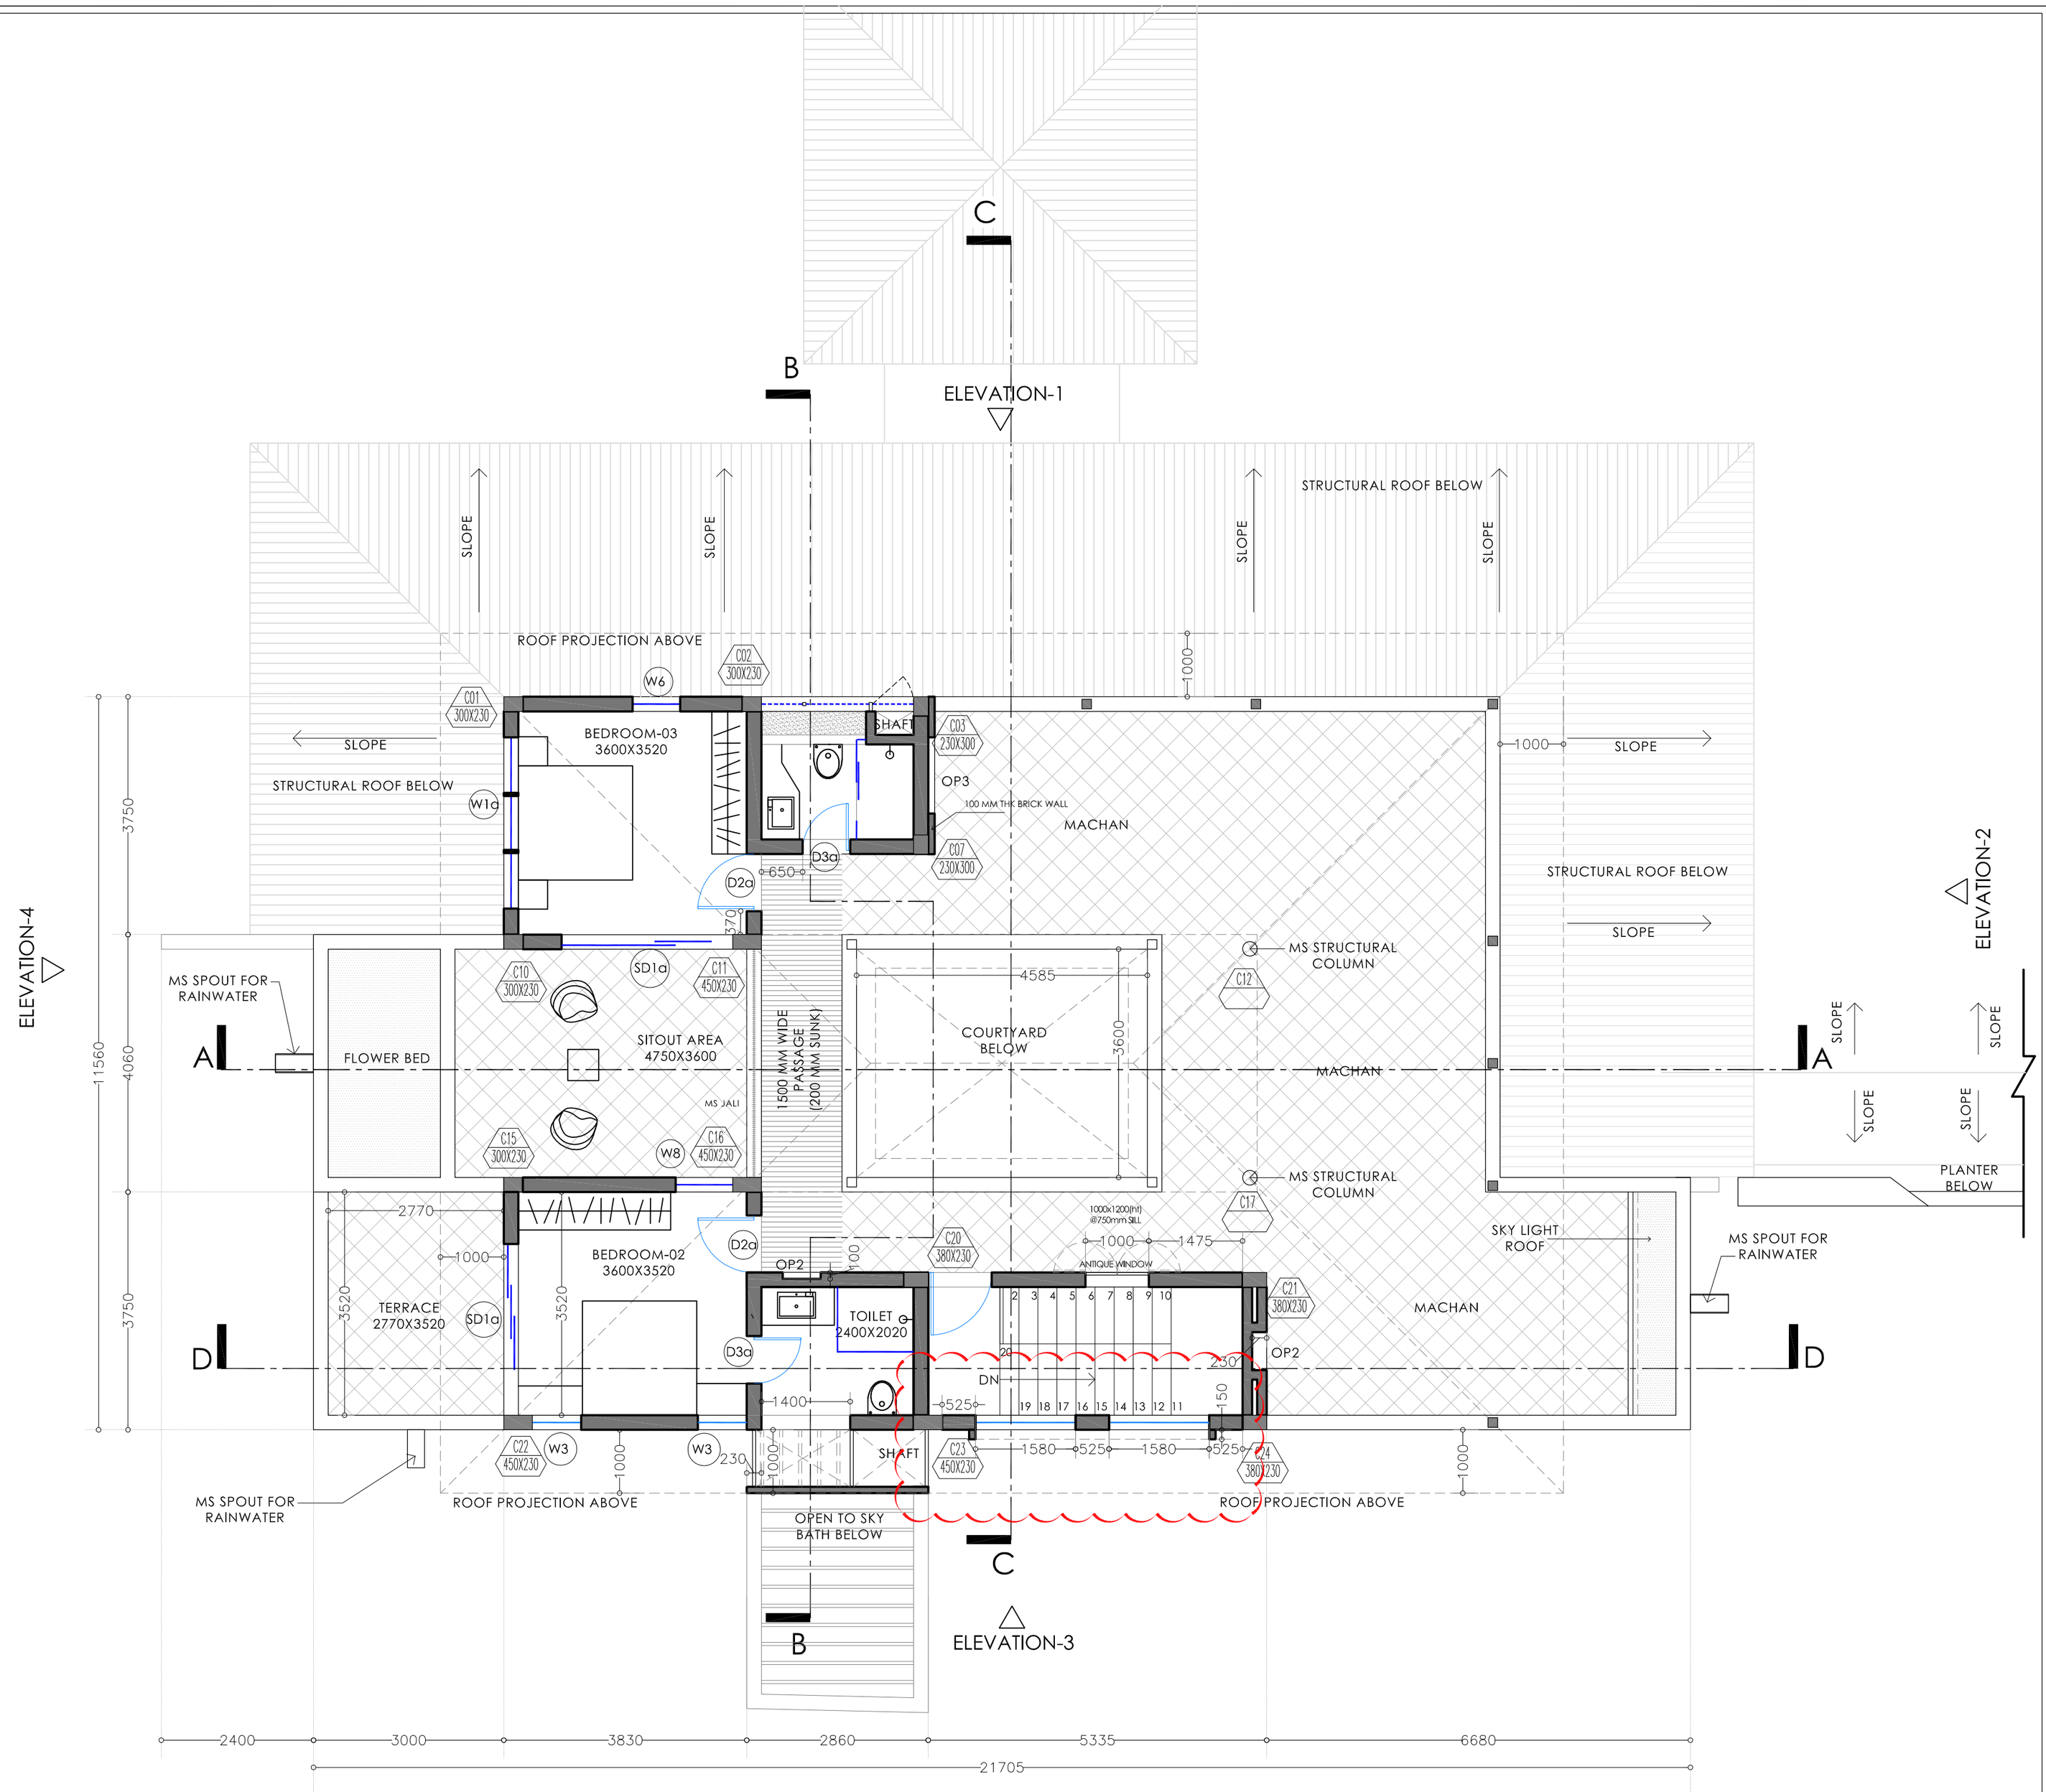


COPYRIGHT NOTE :-

THIS DRAWING IS SOLE PROPERTY OF DESIGN CONSULTANTS ARCHITECTS PVT. LTD. AND THE COPYRIGHT OF THIS DRAWING SHALL REMAIN WITH US. THIS DRAWING MUST NOT WITHOUT OUR CONSENT BE SHOWN TO ANY PERSON OUTSIDE THE RECIPIENT, EMPLOYER OR BE COPIED OR ALTERED OR USED FOR THE PURPOSE OF CONSTRUCTION OR MANUFACTURING ANY ARTICLE SHOWN IN THIS DRAWING. THIS DRAWING ALONG WITH COPIES MADE BY THE RECIPIENT SHALL BE RETURNED ON DEMAND TO US.

NOTES :

1. ALL DIMENSIONS ARE IN Mtr
2. ONLY WRITTEN DIMENSIONS ARE TO BE FOLLOWED
3. ALL LEVELS INDICATED IN THE DRAWING ARE FROM THE FINISHED FLOOR LEVEL
4. IN CASE OF ANY DISCREPANCY PLEASE REFER TO THE ARCHITECTS

DOOR WINDOWS OPENING SCHEDULE

D/W	WIDTH	SILL	LINTEL	NOS	LOCATION
SD1a	2700	-	2100	1	BEDROOM 02
SD1b	2700	-	2100	1	BEDROOM 03
D2a	900	-	2100	2	BEDROOM- 02 & 03 ENTRY
D3a	800	-	2100	2	TOILET

DOOR WINDOWS OPENING SCHEDULE

D/W	WIDTH	SILL	LINTEL	NOS	LOCATION
W1a	2700	1050	2100	1	BEDROOM-03
W3	770	600	BEAM BOTTOM	1	BEDROOM 02
W6	750	900	1650	1	BEDROOM 03
W8	900	300	2100	1	BEDROOM 02
OP2	600	1050	1650	1	PASSAGE
OP3	1200	1200	1650	1	MACHAN

LEGEND: FOUNDATION WALLS & PLINTH BEAMS BELOW PLINTH LEVEL

	230 MM THK BRICK WORK
	115 MM THK BRICK WORK
	RCC COLUMN
	MACHAN
	COURTYARD
	TOILET AREA

ARCHITECTS SIGN AND STAMP

N

NORTH

CLIENT NAME

MR. RAJENDRA KARNE, BARAMATI.

PROJECT NAME

PROPOSED BUNGALOW AT, BARAMATI

DRAWING NAME	DRAWING NO.
FIRST FLOOR PLAN	DC-007 (R2)

SR.NO.	REVISIONS	DATE	DRAWN BY
R1	toilet cantilever extended	29 / 04 / 16	pankaj
R2	STAIRCASE OPENING	30 / 08 / 16	pankaj

STATUS	GOOD FOR CONSTRUCTION
DATE :	20/02/16
SCALE :	1:75 (Size-A2)
DRAWN BY	YOGENDRA
CHECKED BY	PANKAJ

Design Consultants Architects Pvt. Ltd.

Website:www.dcapl.net
E-mail: dc@dcapl.net
Tel.: +91-20-25411470 Fax: +91-20-25422819