


Weitergabe sowie Vervielfältigung dieses Dokuments, Verwertung und Mitteilung seines Inhalts sind verboten, soweit nicht ausdrücklich gestattet. Zuwiderhandlungen verpflichten zu Schadenersatz. Alle Rechte für den Fall der Patent-, Gebrauchsmuster- oder Geschmacksmustereintragung vorbehalten.

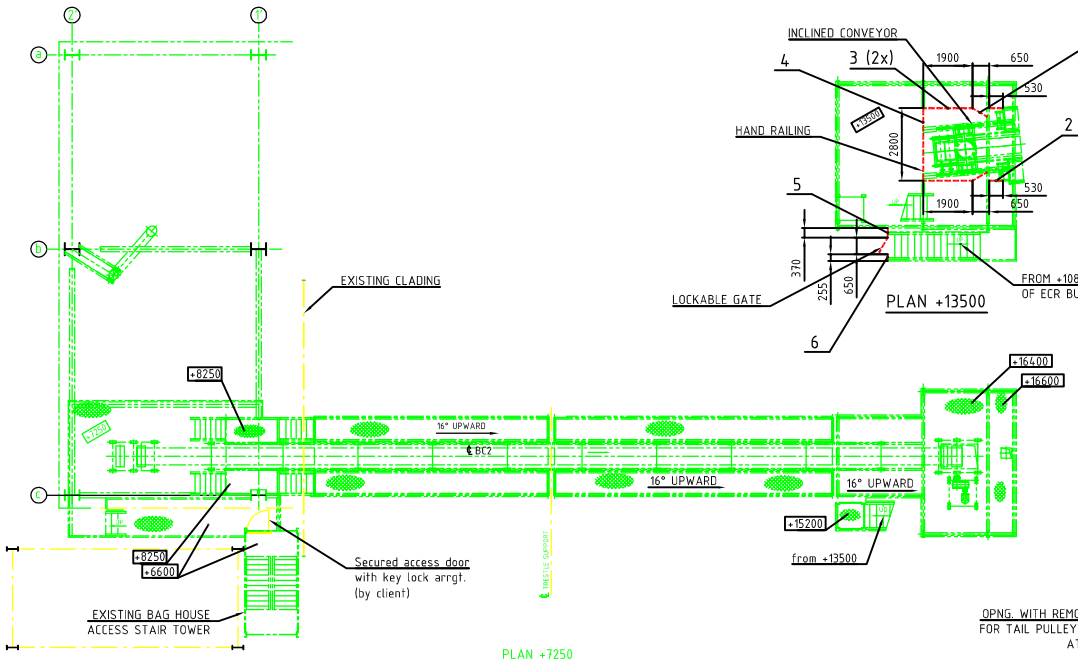


PLAN +7250

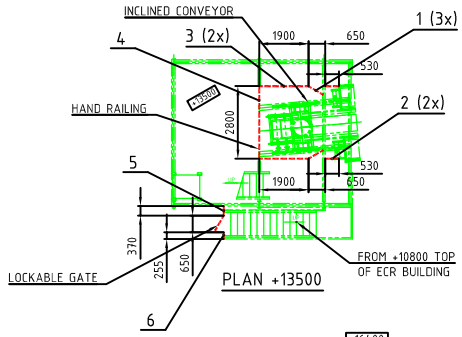


PLAN +13500

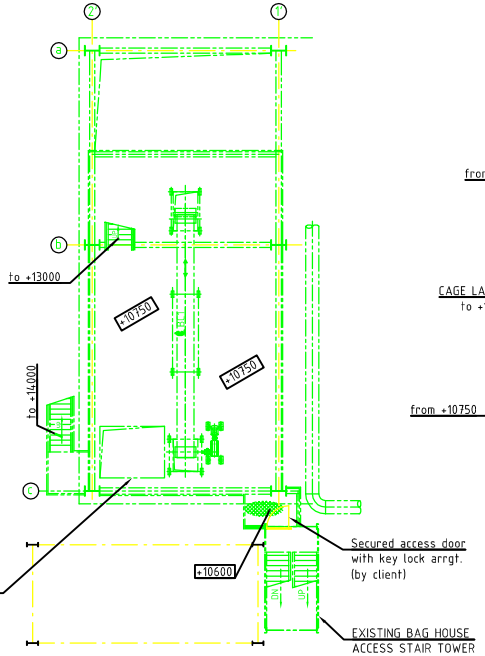


PLAN +10750

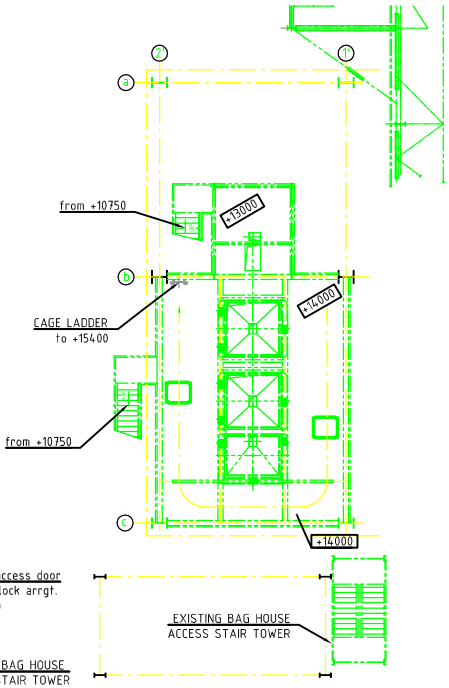


PLAN +14000 & +13000

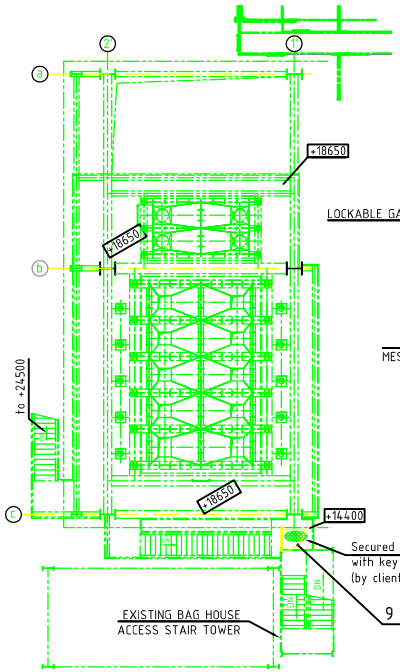

PLAN +18650

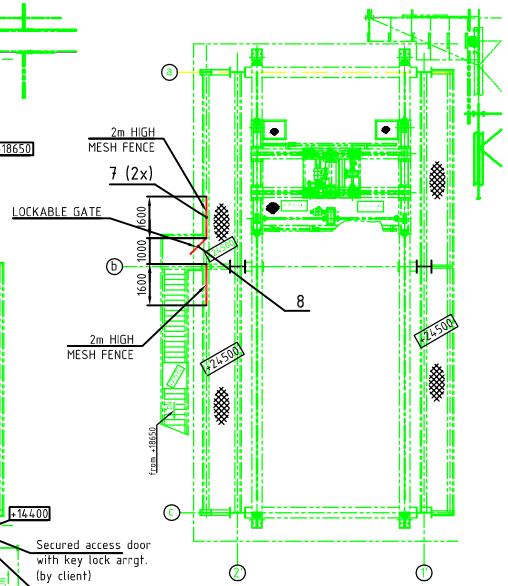

PLAN +24500

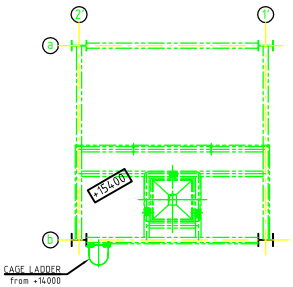

PLAN +15400

ITEM NO.	DESCRIPTION	QTY.
1	LOCKABLE GATE - W=650 x 2 Mtr. HEIGHT	3
2	MESH FENCE - 530 x 2 Mtr. HEIGHT	2
3	MESH FENCE - 1900 x 2 Mtr. HEIGHT	2
4	MESH FENCE - 2800 x 2 Mtr. HEIGHT	1
5	MESH FENCE - 370 x 2 Mtr. HEIGHT	1
6	MESH FENCE - 255 x 2 Mtr. HEIGHT	1
7	MESH FENCE - 1600 x 2 Mtr. HEIGHT	2
8	LOCKABLE GATE - W=1000 x 2 Mtr. HEIGHT	1
9	SECURED ACCESS DOOR WITH KEY LOCK ARRGT. W=850 x 2 Mtr. HEIGHT	3

-STATUS AS ON DATE = 16.01.2015

NOTES
1. EDGES OF ALL PLATFORMS, WALKWAYS ETC. TO BE FITTED WITH STANDARD HANDRAILING UNLESS OTHERWISE NOTED.
2. ALL INTERLOCKED GATES TO BE 2m HIGH.
3. ALL REMOVABLE ACCESS PANELS TO BE REMOVED USING STANDARD TOOL.
4. ALL MOVING PARTS TO BE FULLY GUARDED.
5. FOR LEGEND REFER TO DRAWING NUMBER 1312R-D37-001.
6. 2m HIGH FENCE TO BE ERECTED EITHER SIDE OF ACCESS GATE TO PREVENT BYPASS OF GATE BY CLIMBING OVER HANDRAILING.

REV.NO.	DATE	ZONE	DESCRIPTION	BY	CHECKED
-	-	-	-	-	-
-	-	-	-	-	-
A	16.01.15	-	DRAWING UPDATED	RASI	RAUP

REVISIONS

BASIC ENGINEERING

TATA STEEL LIMITED
JAMSHEDPUR, JHARKHAND

DEPT.		CODE	
AREA		CODE	
SUBJECT		CODE	
TATA DRG. NO.:		REV.	

Consulting Engineers: M. N. DASTUR & COMPANY (P) LTD, KOLKATA

Project-Nr. / Project-No.: TATA - LD 2 S3H6

Benennung / Designation: 165t DUPLEX RH UNIT
TECHNOLOGICAL STRUCTURES
SAFETY FENCING & ACCESS GATES (ALLOY SYS.)

SMS SIEMAG group

	Datum	Name
Drawn	16.12.2014	PKGA
Chkd	17.12.2014	RAUP
Resp.	17.12.2014	RAUP
Dept	1131	
Tel.	1752	

Maßst. / Scale: 1:100 | ISO 128 First angle projection method | Projektionsmethode / | Fertigungsvorschriften / Manufacturing Instructions: SN 200

Werkstoff, Material | Stückgew., Unit weight: Kg

Enlst. aus: A 1312R-D37-008

Zeichnungs-Nr./Drawing-No.: 1312R-D03-182 A

Blatt / Sheet: 1 von / of 5

CAD

SMS Siemag - AutoCAD Vorlage V-4455-1 / 03.09