

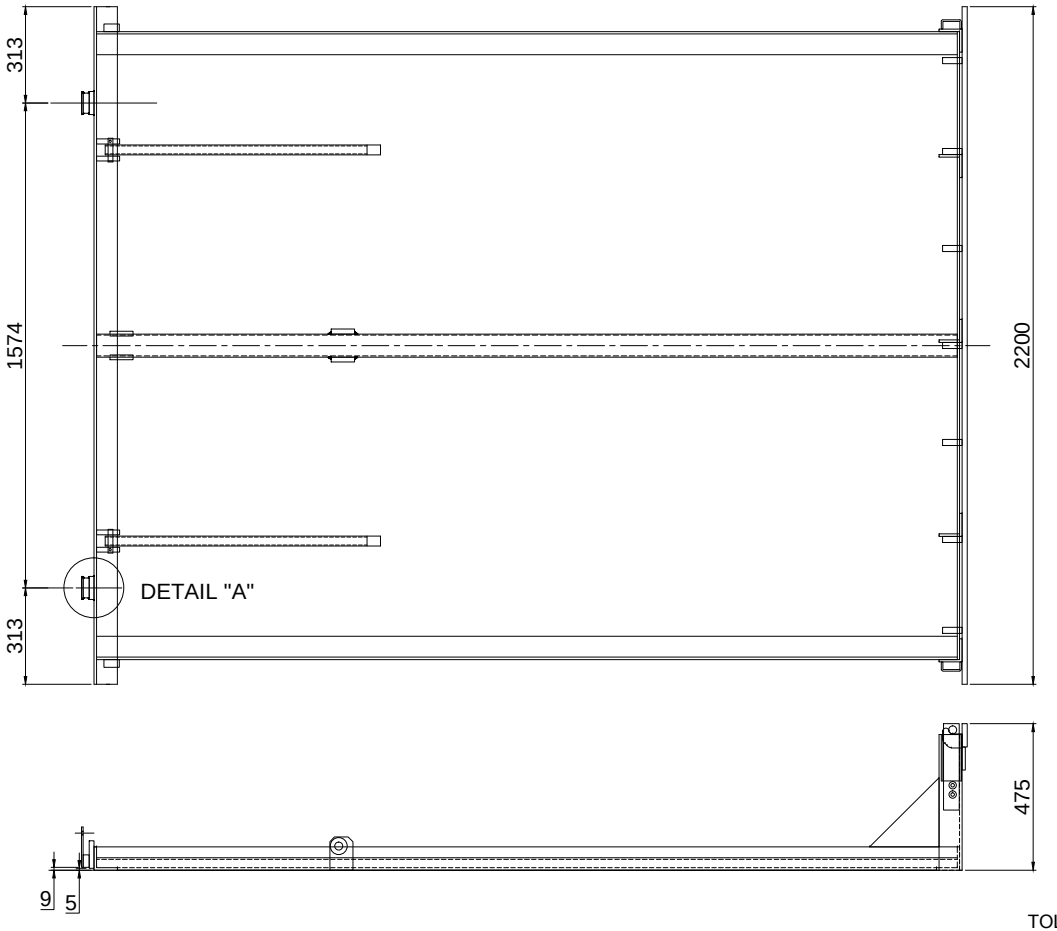


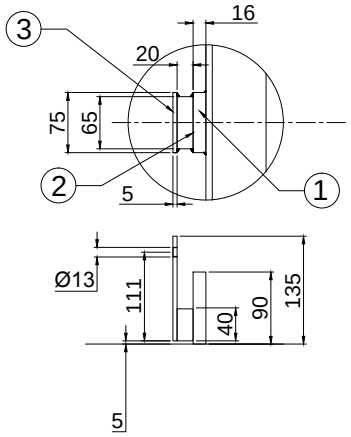

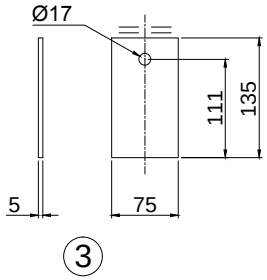

NOTE:~ MTL : MS

1. FLAT 75 X 16 X 90L = 2 NOS
2. FLAT 40 X 20 X 65L = 2 NOS
3. FLAT 75 X 5 X 135L = 2 NOS (SEE DRG)
4. HIGH TENSILE BOLT M12 X 50L = 2 NOS

TOLERANCE - ±5mm

This drawing & design is the property of NIHVA TECHNOLOGIES. Not to be sold or copied to any other concern.

TITLE

FLAP LOCKING ASSLY

NIHVA TECHNOLOGIES PVT. LTD.

NIHVA TECHNOLOGIES PVT. LTD. PUNE
Tel : 020 66304033
Email:- info@nihva.com
Website:- www.nihva.com

	NAME	SIGN	DATE
DRAWN	P.A		
CHECK	SHEKHAR		
APPRD.	SHEKHAR		

If any queries contact : design@nihva.com	DWG. NO. : NIHVA/17-18/	REV- 0
ALL DIMENSION ARE IN mm	SCALE: NTS WT:	SHEET: 01 OF 01

CLIENT -

PROJECT - DLBJ1001

SITE LOCATION -