




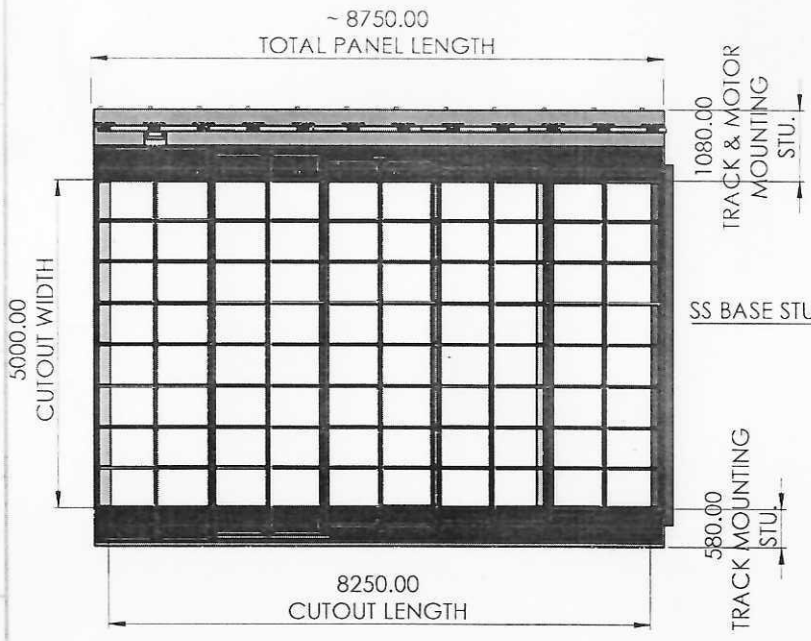


DETAIL A
SCALE 1 : 20

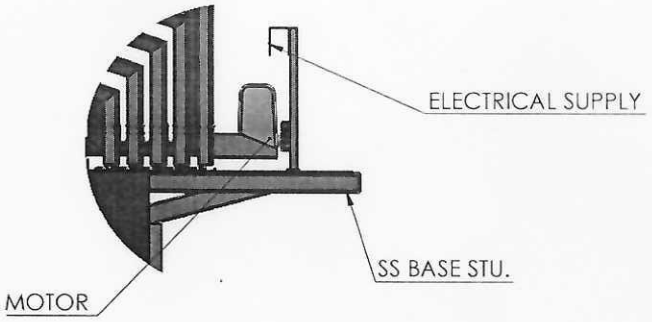


DETAIL B
SCALE 1 : 20

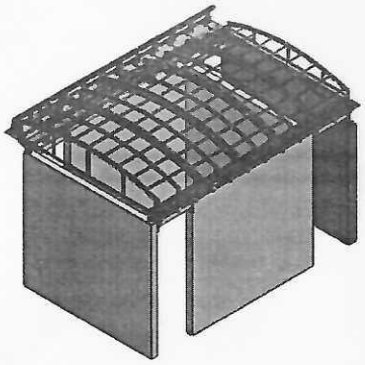


100% CLOSE

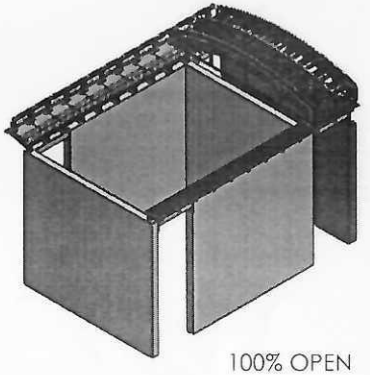

100% OPEN

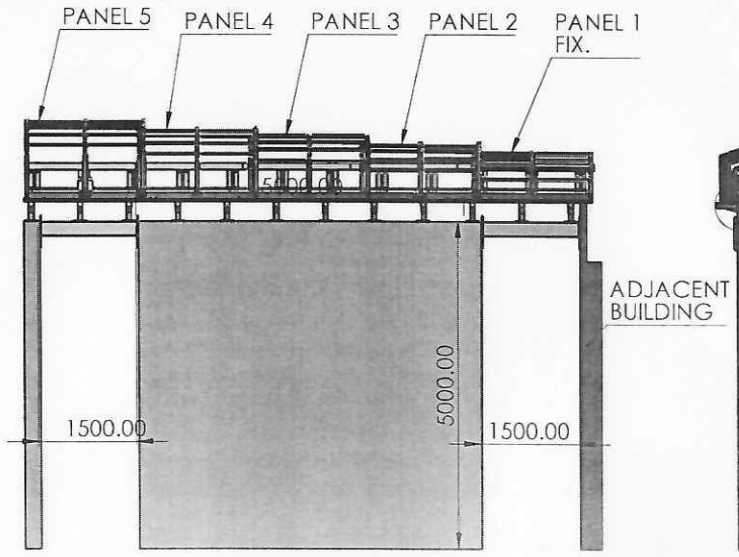

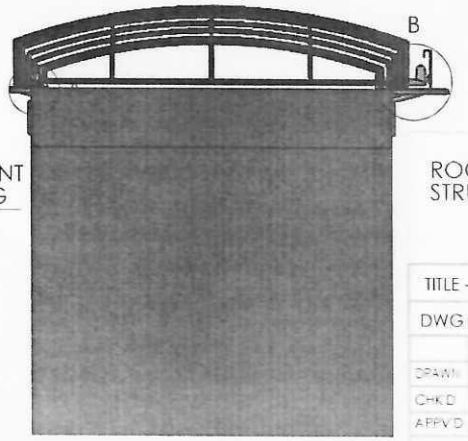

ROOFING SHEET - ALUMINIUM PANEL MIN THICKNESS 1 MM
STRUCTURAL MEMBERS - TRACK MOUNTING BASE FRAME STRUCTURE ABOVE THE WALL MADE UP WITH SS.

TITLE - RETRACTABLE ROOF				NIHVA TECHNOLOGIES PVT LTD PUNE
DWG NO - NTPL-PM-01-00-00-00				
	NAME	SIGNATURE	DATE	PROJECT NO - NTPL-PM-189
DRAWN	J.P.		7-11-2025	PRODUCT - RETRACTABLE ROOF
CHK'D	B.S.	Babale	7-11-2025	SITE LOCATION - PIRVANDRUM
APPV'D	V.T.		7-11-2025	
If any queries contact - Design@nihva.com				REVISION - QTY -
ALL DIMENSION ARE IN mm			A3	SCALE -

7/11/25