
GROUND FLOOR PLAN - @0.00LVL

ELECTRICAL LAYOUT

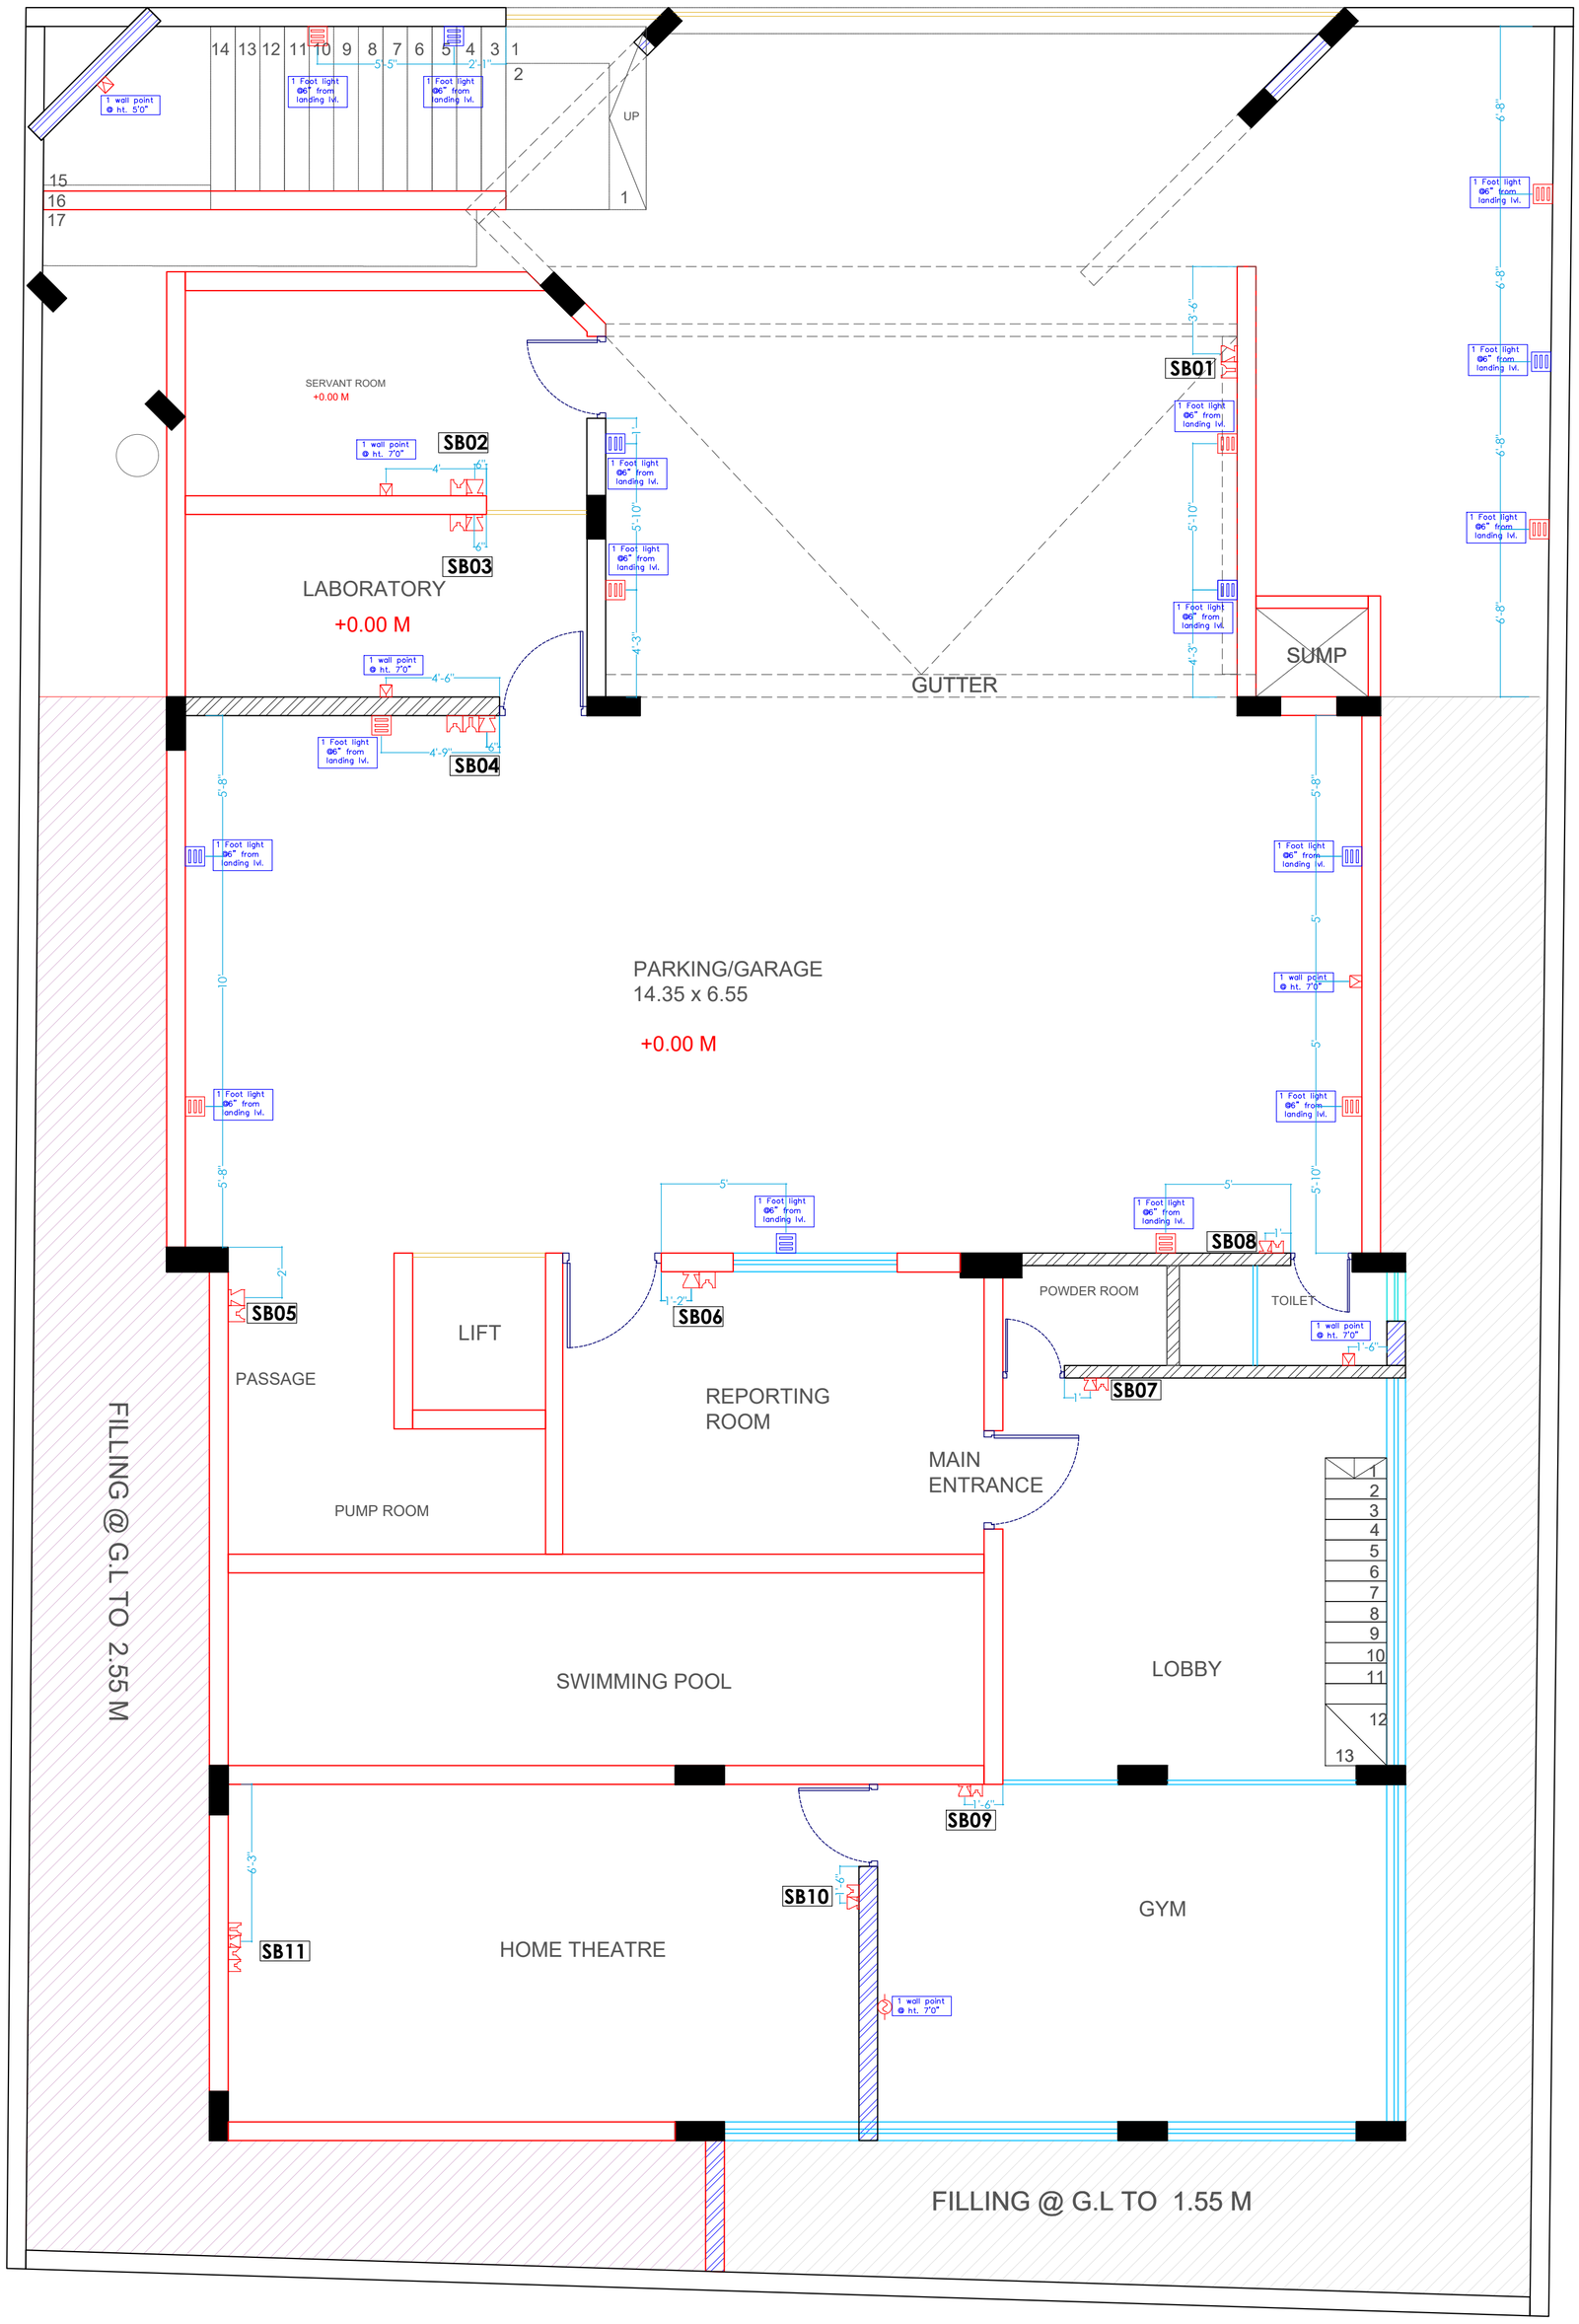


SB01	@3'- 6" BTM. FROM FFL	SB02	@3'- 6" BTM. FROM FFL	SB03	@3'- 6" BTM. FROM FFL
SB04	@3'- 6" BTM. FROM FFL	SB05	@3'- 6" BTM. FROM FFL	SB06	@3'- 6" BTM. FROM FFL
SB07	@3'- 6" BTM. FROM FFL	SB08	@3'- 6" BTM. FROM FFL	SB09	@3'- 6" BTM. FROM FFL
SB10	@3'- 6" BTM. FROM FFL	SB11	@2' BTM. FROM FFL		

Switch board		Cable point	
Light point		CHIMNEY	
Foot light		Speaker point	
6 Amp Plug point		16 amp Plug point	
Exhaust fan		Bell	
Inverter connection		Wall point	
A.C. point		Inverter point	
C.C.T.V.		Chandelier point	
LED CON.POINT		Entrance Gate Motor	
Hanging Lamp		Entrance Gate Lamp	
Wall fan		Video locker screen	
Drinking water		CCTV screen	

PROJECT : PROPOSED INTERIOR DRAWING FOR DR.NIKAM AT KARAD.	JOB NO : P153	DRN BY : Sarthavi Shah	1. This Drawing is a copyright of PRANEEL MULICK ASSOCIATE. and should not be retained, copied or used Without their authority. 2. Do not scale the drawing. 3. This Drawing to be read along with other relevant drawings. 4. Any variation between the drawing & specification should be brought to the notice of the architects by the contractors in writing prior to the construction.	architecture interior design space planning	MULICK ASSOCIATE, SANGAM GAS, NEAR HOTEL SANGAM P.B.HIGHWAY. KARAD.415110 PH : 9970266774. Email: praneelmulick@gmail.com
	DWG NO : P153-ID-ELE	CHK BY : Praneel Mulick			
TITLE : GROUND FLOOR PLAN - SWITCH BOARD AND WALL POINT LOCATION	SCALE : 1:100	ISSUE DATE : 06-02-26			mulick associate

FIRST FLOOR PLAN - @2.70LVL

ELECTRICAL LAYOUT

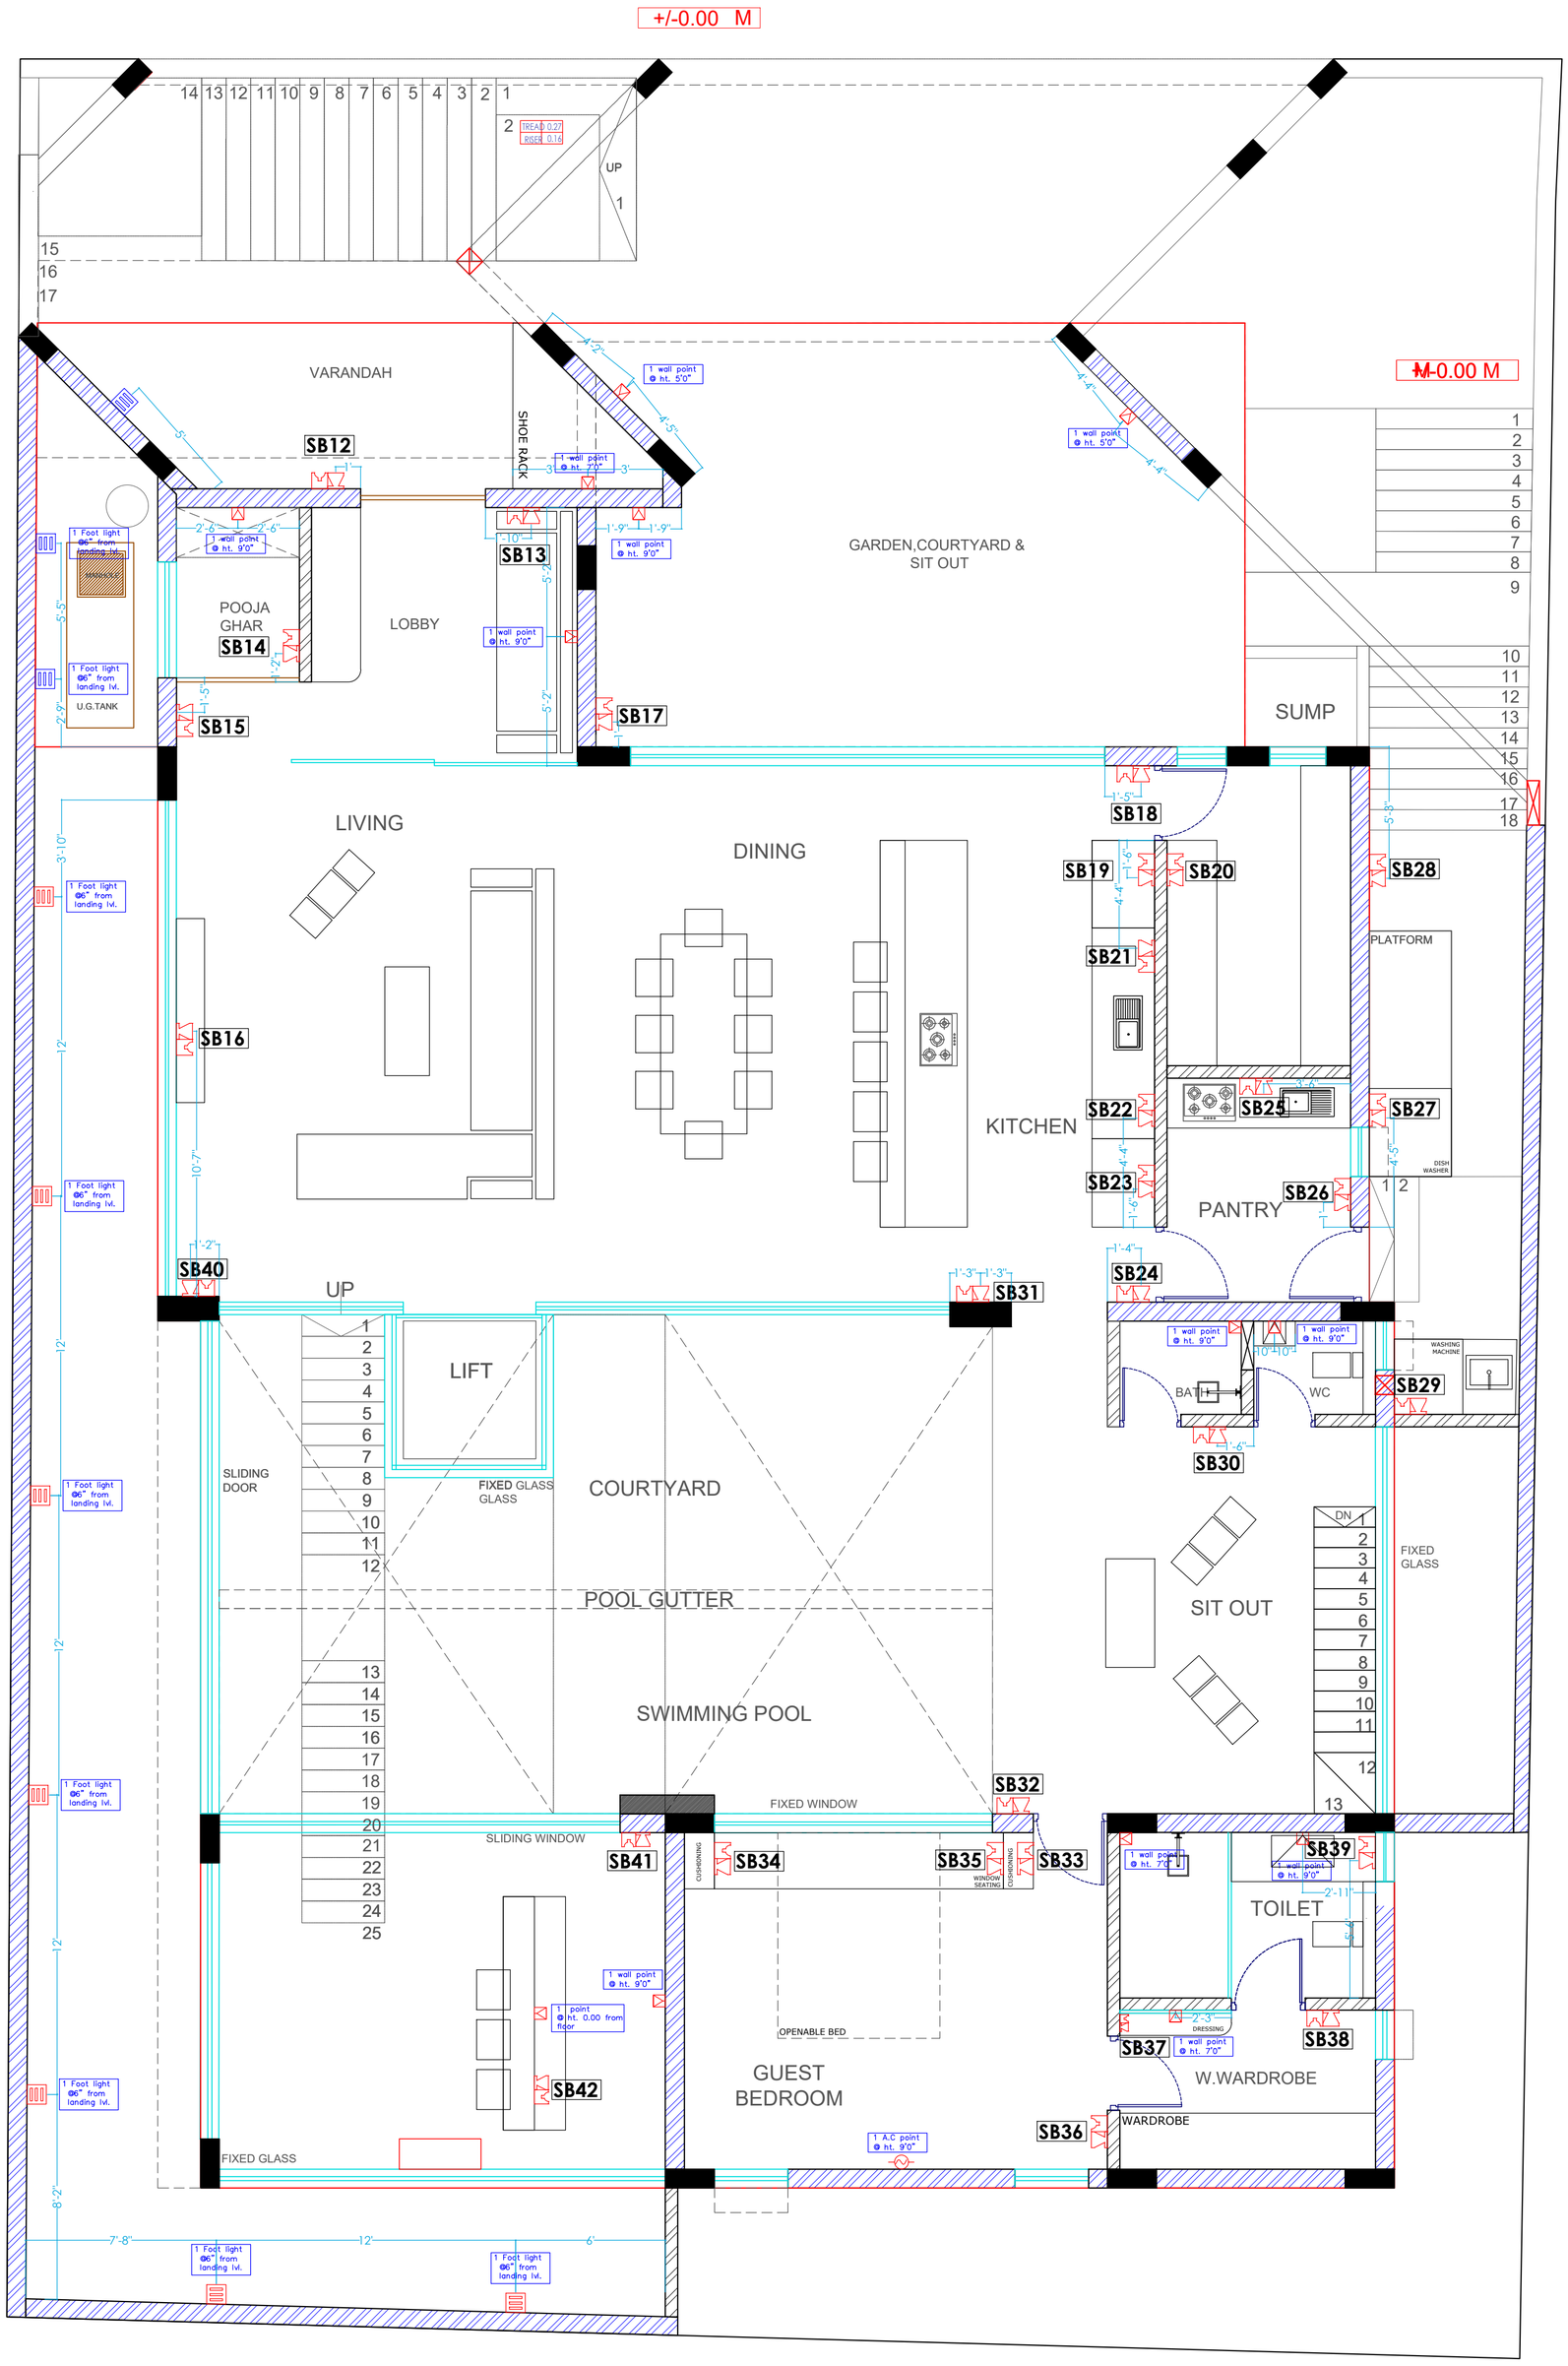

SB12	@3'- 6" BTM. FROM FFL	**SB13**	@3'- 6" BTM. FROM FFL	**SB14**	@3'- 6" BTM. FROM FFL
SB15	@3'- 6" BTM. FROM FFL	**SB16**	@0.00 @FFL.	**SB17**	@3'- 6" BTM. FROM FFL
SB18	@3'- 6" BTM. FROM FFL	**SB19**	@5'- 6" BTM. FROM FFL	**SB20**	@3'- 6" BTM. FROM FFL
SB21	@6" FROM COUTER TOP	**SB22**	@6" FROM COUTER TOP	**SB23**	@6" FROM COUTER TOP
SB24	@3'- 6" BTM. FROM FFL	**SB25**	@6" FROM COUTER TOP	**SB26**	@3'- 6" BTM. FROM FFL
SB27	@3'- 6" BTM. FROM FFL	**SB28**	@3'- 6" BTM. FROM FFL	**SB29**	@6" FROM COUTER TOP
SB30	@3'- 6" BTM. FROM FFL	**SB31**	@3'- 6" BTM. FROM FFL	**SB32**	@3'- 6" BTM. FROM FFL
SB33	@3'- 6" BTM. FROM FFL	**SB34**	@2'- 6" BTM. FROM FFL	**SB35**	@2'- 6" BTM. FROM FFL
SB36	@3'- 6" BTM. FROM FFL	**SB37**	@2' BTM. FROM FFL	**SB38**	@3'- 6" BTM. FROM FFL
SB39	@3'- 6" BTM. FROM FFL	**SB40**	@3'- 6" BTM. FROM FFL	**SB41**	@3'- 6" BTM. FROM FFL
SB42	@0.00 BTM. FROM FFL				

	Switch board		Cable point
	Light point		CHIMNEY
	Foot light		Speaker point
	6 Amp Plug point		16 amp Plug point
	Exhaust fan		Bell
	Inverter connection		Wall point
	A.C. point		Inverter point
	C.C.T.V.		Chandelier point
	LED CON.POINT		Entrance Gate Motor
	Hanging Lamp		Entrance Gate Lamp
	Wall fan		Video locker screen
	Drinking water		CCTV screen

PROJECT : PROPOSED WORKING DRAWING FOR DR.NIKAM AT KARAD.	JOB NO : P153	DRN BY : Sarthavi Shah	1. This Drawing is a copyright of PRANEEL MULICK ASSOCIATE. and should not be retained, copied or used Without their authority. 2. Do not scale the drawing. 3. This Drawing to be read along with other relevant drawings. 4. Any variation between the drawing & specification should be brought to the notice of the architects by the contractors in writing prior to the construction.
TITLE : FIRST FLOOR PLAN - SWITCH BOARD AND WALL POINT LOCATION	DWG NO : P153-ID-ELE	CHK BY : Praneel Mulick	
	SCALE : 1:100	ISSUE DATE : 06-02-26	


architecture
interior design
space planning

MULICK ASSOCIATE, SANGAM GAS, NEAR HOTEL SANGAM P.B.HIGHWAY. KARAD.415110
PH : 9970266774.
Email: praneelmulick@gmail.com

mulick associate

SECOND FLOOR PLAN - @6.81LVL

ELECTRICAL LAYOUT

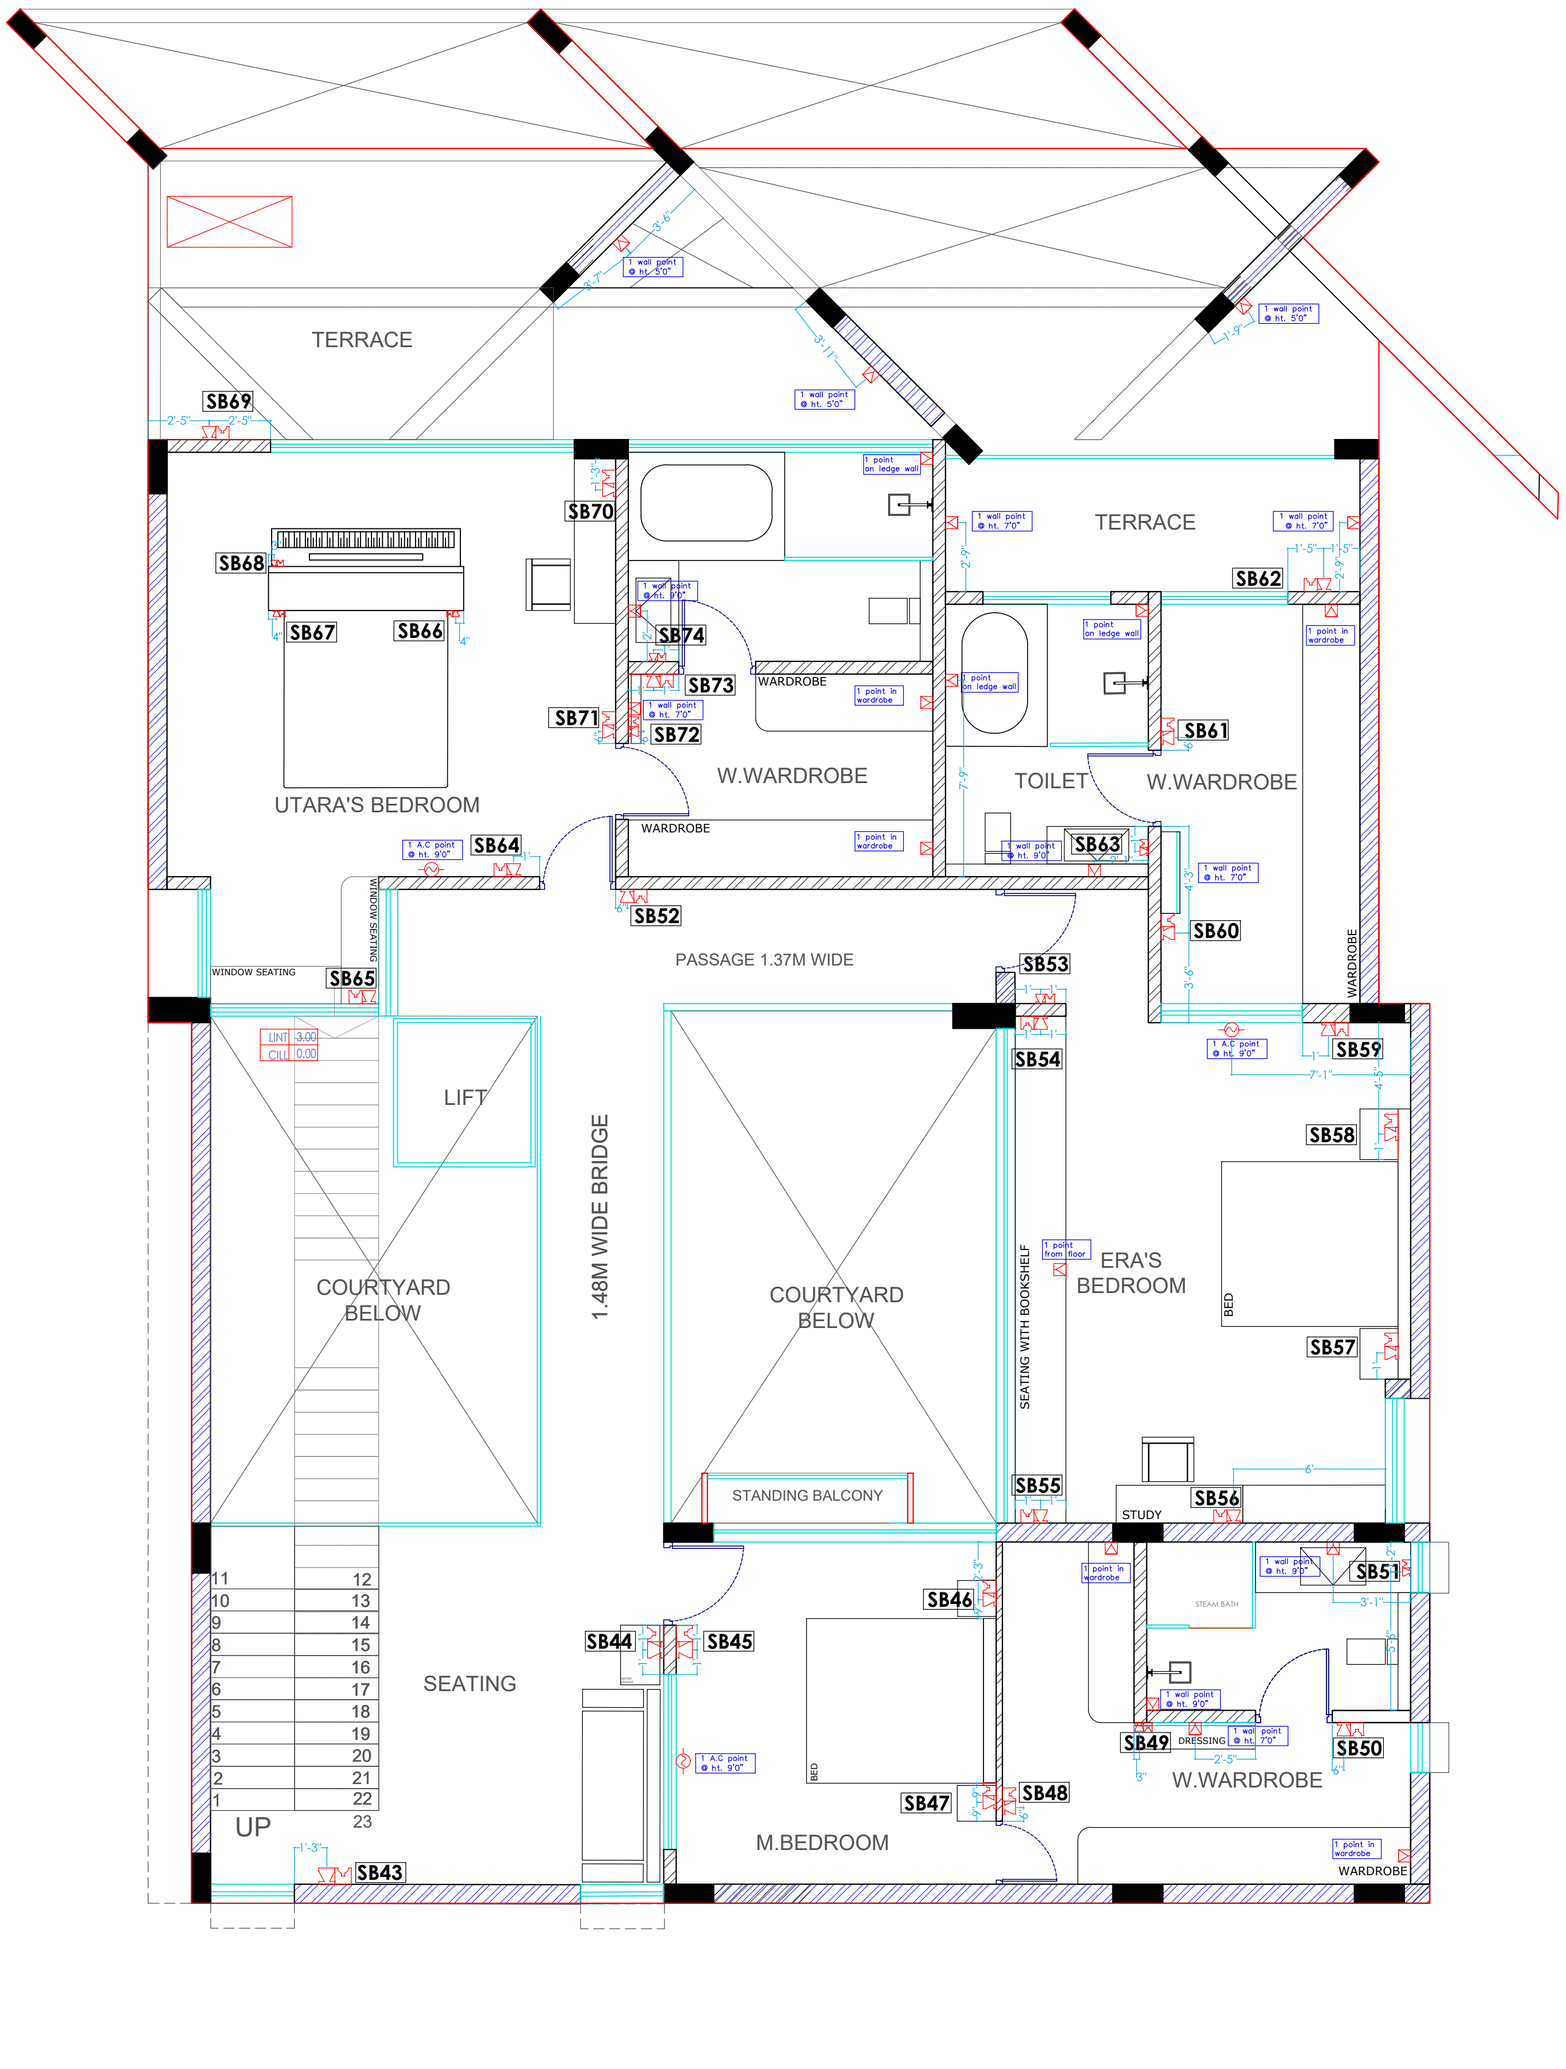

SB43	@3'- 6" BTM. FROM FFL	**SB44**	@3'- 6" BTM. FROM FFL	**SB45**	@3'- 6" BTM. FROM FFL
SB46	@2'- 6" BTM. FROM FFL	**SB47**	@2'- 6" BTM. FROM FFL	**SB48**	@3'- 6" BTM. FROM FFL
SB49	@2' BTM. FROM FFL	**SB50**	@3'- 6" BTM. FROM FFL	**SB51**	@3'- 6" BTM. FROM FFL
SB52	@3'- 6" BTM. FROM FFL	**SB53**	@3'- 6" BTM. FROM FFL	**SB54**	@ 2' FROM WINDOW SEATING
SB55	@ 2' FROM WINDOW SEATING	**SB56**	@ 6" BELOW STUDY TABLE	**SB57**	@2'- 6" BTM. FROM FFL
SB58	@2'- 6" BTM. FROM FFL	**SB59**	@3'- 6" BTM. FROM FFL	**SB60**	@2' BTM. FROM FFL
SB61	@3'- 6" BTM. FROM FFL	**SB62**	@3'- 6" BTM. FROM FFL	**SB63**	@3'- 6" BTM. FROM FFL
SB64	@3'- 6" BTM. FROM FFL	**SB65**	@0.00 BTM. FROM FFL	**SB66**	@0.00 BTM. FROM FFL
SB67	@0.00 BTM. FROM FFL	**SB68**	@0.00 BTM. FROM FFL	**SB69**	@3'- 6" BTM. FROM FFL
SB70	@ 6" BELOW STUDY TABLE	**SB71**	@3'- 6" BTM. FROM FFL	**SB72**	@2' BTM. FROM FFL
SB73	@3'- 6" BTM. FROM FFL	**SB74**	@3'- 6" BTM. FROM FFL		

Switch board	Cable point
Light point	CHIMNEY
Foot light	Speaker point
6 Amp Plug point	16 amp Plug point
Exhaust fan	Bell
Inverter connection	Wall point
A.C. point	Inverter point
C.C.T.V.	Chandelier point
LED CON.POINT	Entrance Gate Motor
Hanging Lamp	Entrance Gate Lamp
Wall fan	Video locker screen
Drinking water	CCTV screen

PROJECT : PROPOSED WORKING DRAWING FOR DR.NIKAM AT KARAD.

TITLE : SECOND FLOOR PLAN - SWITCH BOARD AND WALL POINT LOCATION

JOB NO : P153 | DRN BY : Sarthavi Shah

DWG NO : P153-ID-ELE | CHK BY : Praneel Mulick

SCALE : 1:100 | ISSUE DATE : 06-02-26

1. This Drawing is a copyright of PRANEEL MULICK ASSOCIATE. and should not be retained, copied or used Without their authority.
2. Do not scale the drawing.
3. This Drawing to be read along with other relevant drawings.
4. Any variation between the drawing & specification should be brought to the notice of the architects by the contractors in writing prior to the construction.


architecture
interior design
space planning

MULICK ASSOCIATE, SANGAM GAS, NEAR HOTEL SANGAM P.B.HIGHWAY. KARAD.415110
PH : 9970266774.
Email: praneelmulick@gmail.com

mulick associate

SECOND FLOOR PLAN - @10.41LVL

ELECTRICAL LAYOUT

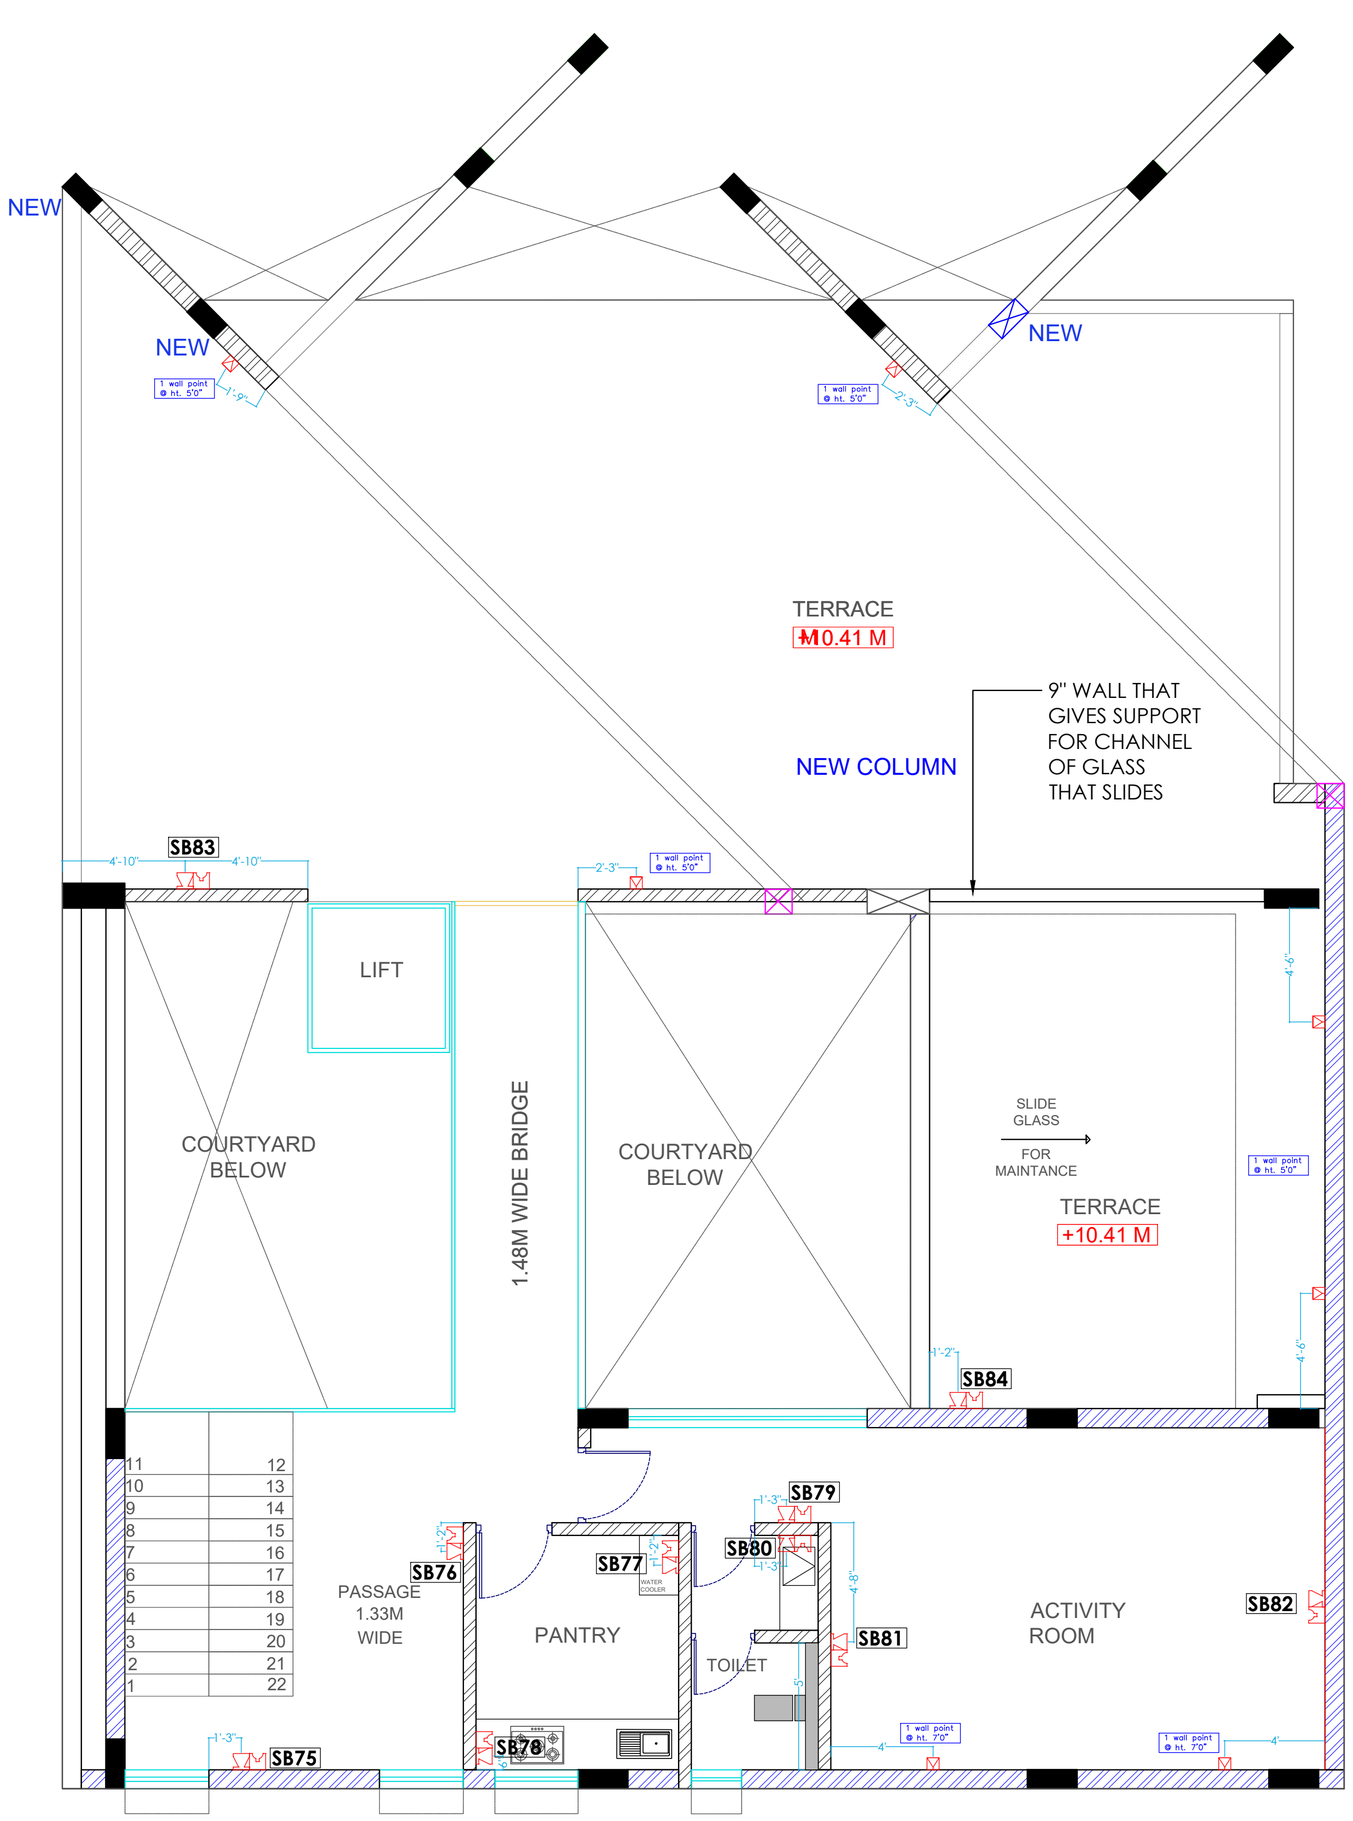

SB75	@3'- 6" BTM. FROM FFL	**SB76**	@3'- 6" BTM. FROM FFL	**SB77**	@3'- 6" BTM. FROM FFL
SB78	@3'- 6" BTM. FROM FFL	**SB79**	@3'- 6" BTM. FROM FFL	**SB80**	@3'- 6" BTM. FROM FFL
SB81	@3'- 6" BTM. FROM FFL	**SB82**	@3'- 6" BTM. FROM FFL	**SB83**	@3'- 6" BTM. FROM FFL
SB84	@3'- 6" BTM. FROM FFL				

PROJECT : PROPOSED WORKING DRAWING FOR DR.NIKAM AT KARAD.	JOB NO : P153	DRN BY : Sarthavi Shah	1. This Drawing is a copyright of PRANEEL MULICK ASSOCIATE, and should not be retained, copied or used Without their authority. 2. Do not scale the drawing. 3. This Drawing to be read along with other relevant drawings. 4. Any variation between the drawing & specification should be brought to the notice of the architects by the contractors in writing prior to the construction.
	DWG NO : P153-ID-ELE	CHK BY : Praneel Mulick	
TITLE : THIRD FLOOR PLAN - SWITCH BOARD AND WALL POINT LOCATION	SCALE : 1:100	ISSUE DATE : 06-02-26	

architecture
interior design
space planning

MULICK ASSOCIATE, SANGAM GAS,
NEAR HOTEL SANGAM
P.B.HIGHWAY. KARAD.415110
PH : 9970266774.
Email: praneelmulick@gmail.com

mulick associate