

PRODUCED BY AN AUTODESK EDUCATIONAL PRODUCT

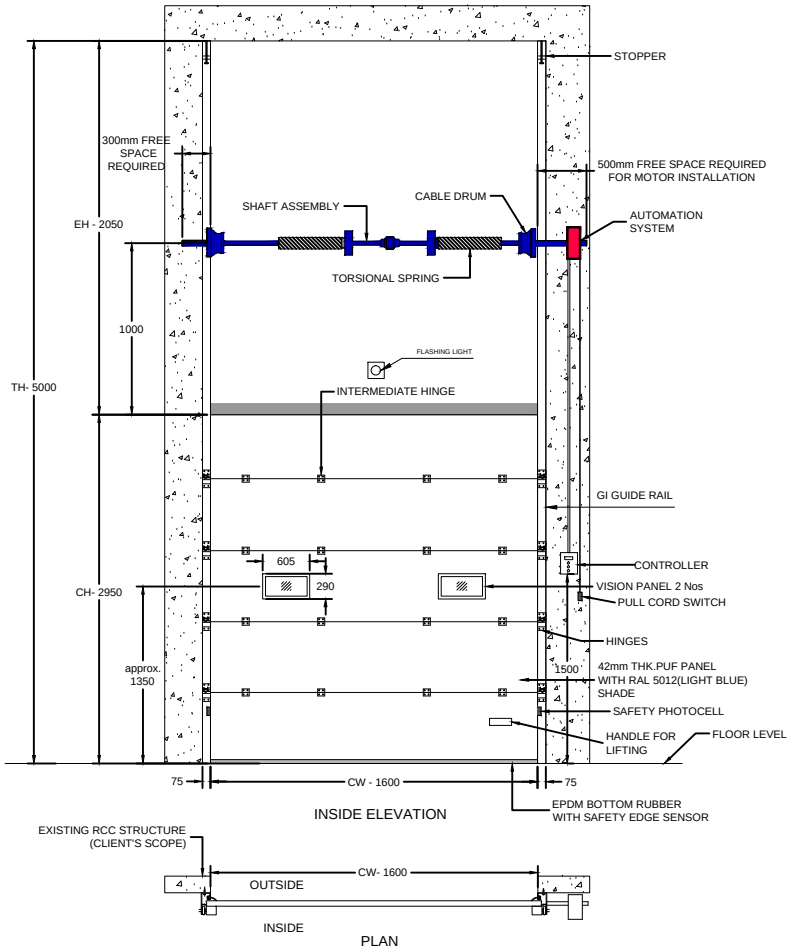


INSIDE ELEVATION

PLAN

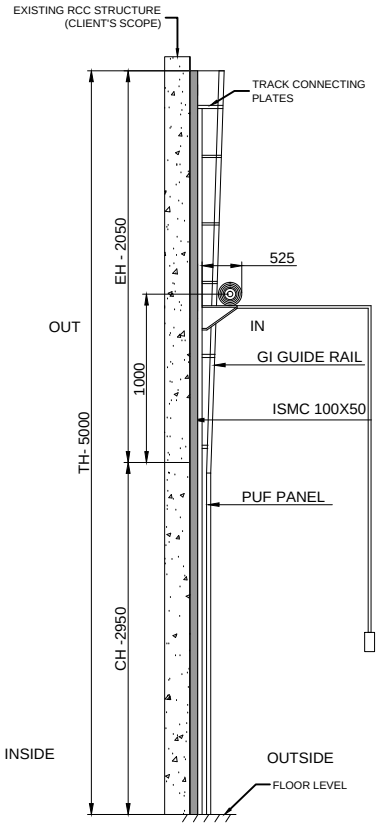

SIDE VIEW

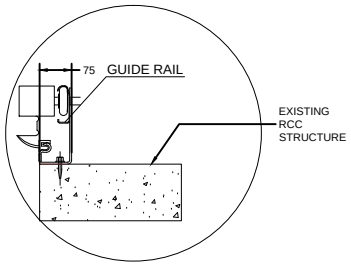

TRACK DETAILS

DIMENSION :

CLEAR WIDTH	CLEAR OPEN HEIGHT	QUANTITY
1600 mm	2300 mm	1

TECHNICAL DATA :

COMPONENTS	MATERIALS	SPECIFICATIONS
DOOR PANELS	GI & PUF	42mm CFC- FREE POLYURETHANE WITH 0.5mm THK, GI PRECOATED PANELS.
DOOR HINGE	——	HEAVY DUTY HINGES FOR INTERLOCKING OF PANELS
SHAFT ASSEMBLY	STD.	TORSIONAL SPRING WITH SHAFT & BEARING PLATES
FINISH		ENAMEL PAINT WITH APPROVED SHADE RAL 5012 LIGHT BLUE

ACCESSORIES-
1. SAFETY PHOTOCELL- 1 PAIR /DOOR
2. FLASH LIGHT- 2 SIDE OF DOOR
3. PULL CORD SWITCH- 1 SINGLE SIDE

IMPORTANT NOTES:

1. REQUIRED STRUCTURE FOR DOOR SHALL BE IN CLIENT'S SCOPE.
2.SINGLE PHASE POWER SUPPLY REQUIRED AT DOOR LOCATION.
3.ALL CIVIL WORK SHALL BE CLIENT'S SCOPE.

NOTE : REQ. CANOPY FOR SPRING & SHAFT - CLIENT SCOPE

REV NO	DATE	DRAWN	REMARK
R01	11.02.20	P.A	1. CLEAR HEIGHT CHANGE

TOLERANCE: ± 10mm

SR NO	CLEAR WIDTH	CLEAR OPEN HEIGHT	QTY	TH	EH
01	1600 mm	2300 mm	1	5000	2700

This drawing & design is the property of NIHVA TECHNOLOGIES. Not to be sold or copied to any other concern.

TITLE: SECTIONAL DOOR (VERTICAL LIFTING)

NIHVA TECHNOLOGIES PVT. LTD. PUNE
Tel : 020 66304033
Website:- www.nihva.com Email:- info@nihva.com

	NAME	SIGN	DATE
DRAWN	P.A		10.02.20
CHECK	G.J		10.02.20
APPROVAL			

CLIENT - CREATIVE CARVE PVT.LTD.
PROJECT -
SITE - PUNE
If any queries contact : design@nihva.com
DWG. NO. : NIHVA/19-20/0208/R01
REV: R01
ALL DIMENSION ARE IN mm
SCALE: NTS
WT:
SHEET: 01 OF 01

PRODUCED BY AN AUTODESK EDUCATIONAL PRODUCT

PRODUCED BY AN AUTODESK EDUCATIONAL PRODUCT