

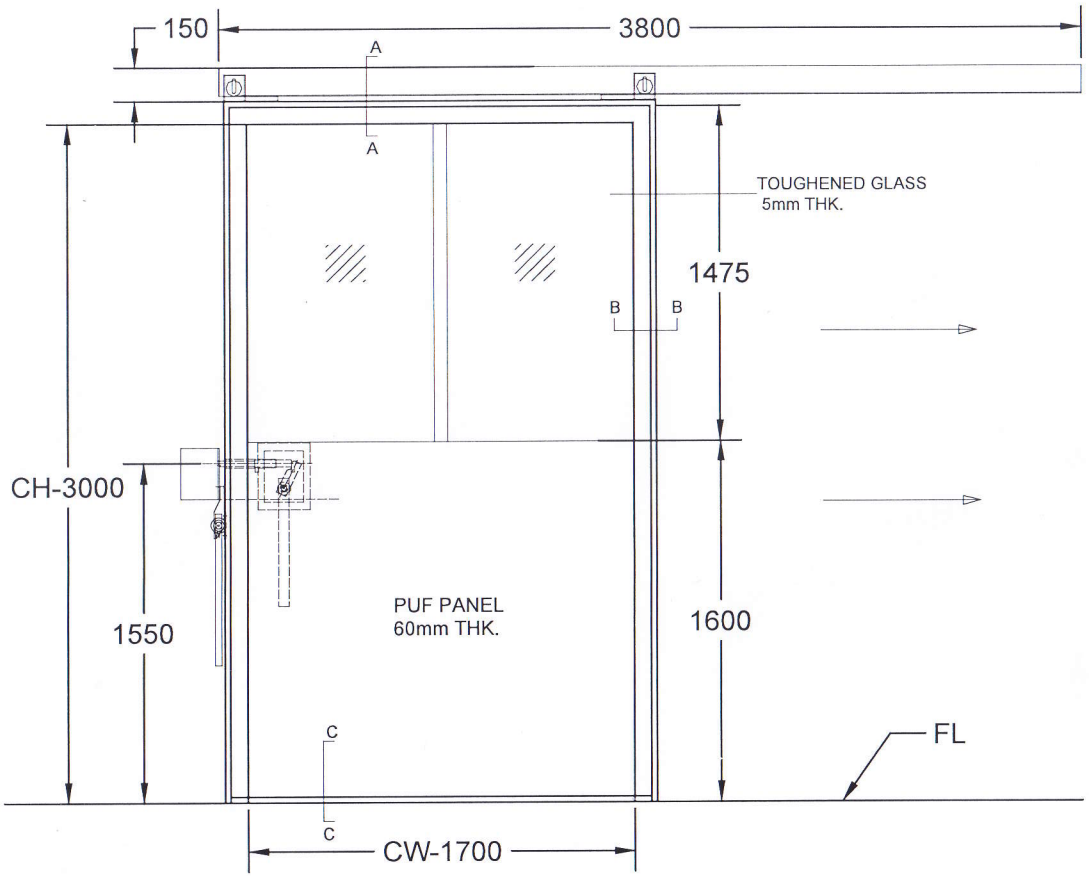



ELEVATION

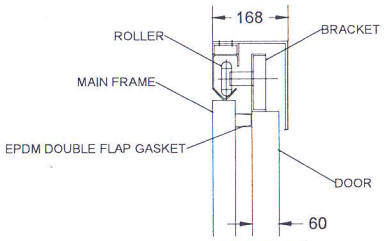

SECTION 'AA'

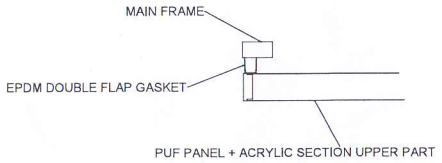

SECTION 'BB'

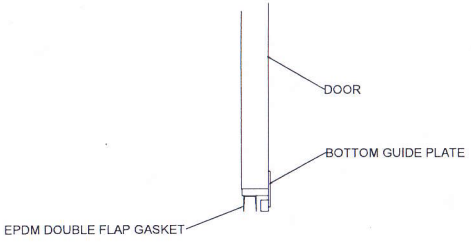

SECTION 'CC'

CLEAR WIDTH	CLEAR HEIGHT	QUANTITY	LOCATION
1700	3000	01	G.L. SOLVENT MIX ROOM

7/10/17

Dandekar & Associates Pune

DOOR TYPE- R.H.S

REVISION 1- DETAILED SECTIONS DRAWN AS PER REQUEST.


REVISION 2 - A. DOOR HANLING TYPE HAS BEEN REVISED. B. INSTEAD ACRYLIC SHEET TOUGHENED GLASS INSTALLED.


COLOR OF DOOR - RAL 9002(GREY WHITE)

This drawing & design is the property of NIHVA TECHNOLOGIES. Not to be sold or copied to any other concern.


TITLE	SLIDING DOOR 1		NIHVA TECHNOLOGIES PVT. LTD.
	SIGN	DATE	
DRAWN	OMKAR	06/10/17	CLIENT -PACKTIME INNOVATION PVT.LTD.
CHECK	SHEKHAR	06/10/17	PROJECT -
REV.			SITE - CHAKAN
APPROVAL	SHEKHAR	06/10/17	DWG. NO. : NIHVA/17-18/0197/R02
If any queries contact : projects@nihva.com			SCALE: NTS / WT: / SHEET: 01 OF 01
ALL DIMENSION ARE IN mm			

NIHVA TECHNOLOGIES PVT. LTD. PUNE
Tel : 020 66304033
Email:- info@nihva.com
Website:- www.nihva.com

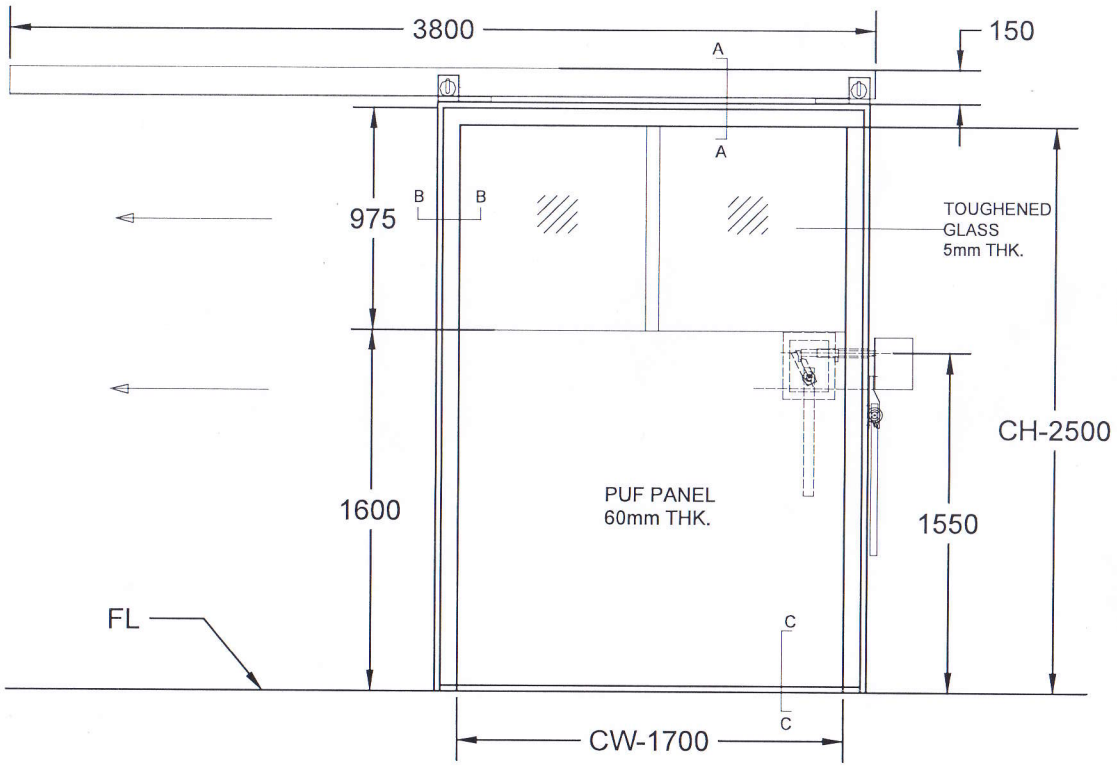


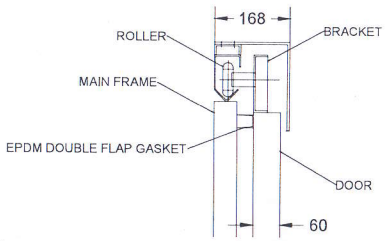

SECTION 'AA'

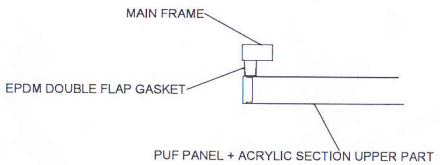

SECTION 'BB'

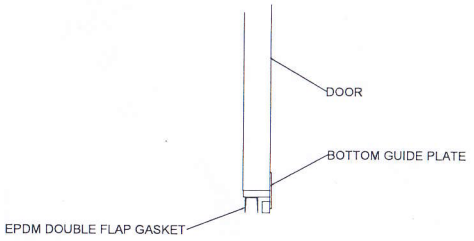

SECTION 'CC'

CLEAR WIDTH	CLEAR HEIGHT	QUANTITY	LOCATION
1700	2500	01	1ST FLOOR INK STORE ROOM

DOOR TYPE- L.H.S

COLOR OF DOOR - RAL 9002(GREY WHITE)

7/10/17

Dandekar & Associates Pune

This drawing & design is the property of NIHVA TECHNOLOGIES. Not to be sold or copied to any other concern.

TITLE	SLIDING DOOR 2		NIHVA TECHNOLOGIES PVT. LTD. PUNE
	SIGN	DATE	NIHVA TECHNOLOGIES PVT. LTD. Tel : 020 66304033 Email:- info@nihva.com Website - www.nihva.com
DRAWN	OMKAR	06/10/17	CLIENT -PACKTIME INNOVATION PVT.LTD.
CHECK	SHEKHAR	06/10/17	PROJECT -
REV.			SITE - CHAKAN
APPROVAL	SHEKHAR	06/10/17	DWG. NO. : NIHVA/17-18/0228
If any queries contact : projects@nihva.com			SCALE: NTS WT: SHEET: 01 OF 01
ALL DIMENSION ARE IN mm			